




NOTE : ~ PLEASE MAINTAIN 8 MM GAP BETWEEN TWO LIP BUSHES.

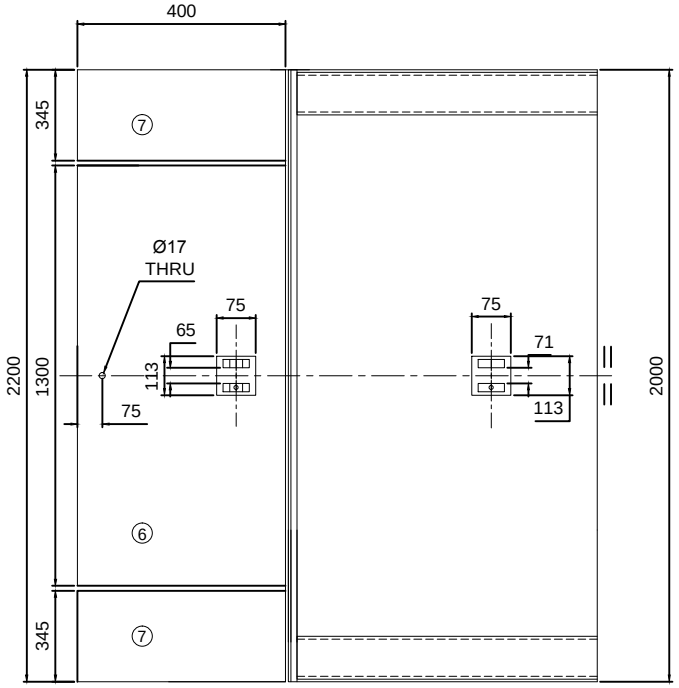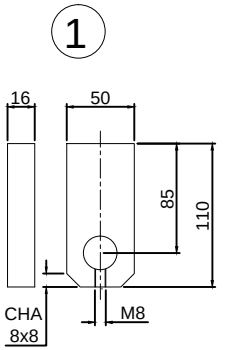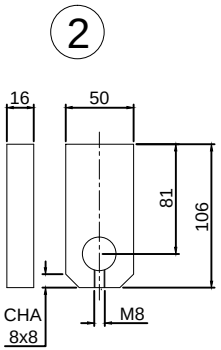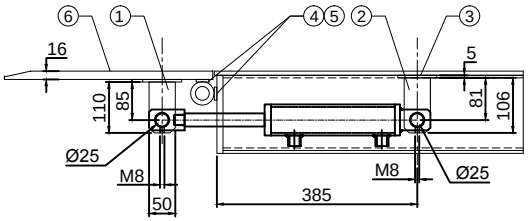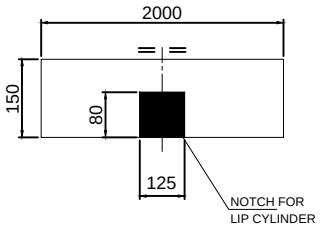


NOTE:~ MTL : MS

| PART NO. | PART NAME | DESCRIPTION | QTY |
|---|---|---|---|
| 1. | FLAT | 50 X 16 X 113L | 2 NOS |
| 2. | FLAT | 50 X 16 X 110L | 2 NOS |
| 3. | FLAT | 75 X 5 X 113L | 2 NOS |
| 4. | FLAT | 25 X 5 X 80L | 16 NOS |
| 5. | FLAT | 25 X 5 X 50L | 10 NOS |
| 6. | CHEQ.SHEET | 400 X 14 X 1300L | 1 NO |
| 7. | CHEQ.SHEET | 400 X 14 X 345L | 2 NOS |

TOLERANCE - ±5mm

This drawing & design is the property of NIHVA TECHNOLOGIES. Not to be sold or copied to any other concern.

TITLE

LIP CYL MOUNTING

NIHVA TECHNOLOGIES PVT. LTD.
NIHVA TECHNOLOGIES PVT. LTD. PUNE
Tel : 020 66304033
Email:- info@nihva.com
Website:- www.nihva.com

| | NAME | SIGN | DATE |
|---|---|---|---|
| DRAWN | PRADEEP | | 05.09.2018 |
| CHECK | PRADEEP | | 05.09.2018 |
| APPRD. | PRADEEP | | 05.09.2018 |

CLIENT -

PROJECT - DLSD1009

SITE LOCATION -

If any queries contact : design@nihva.com

DWG. NO. : NIHVA/18-19/MFG/DLSD1009/006

ALL DIMENSION ARE IN mm

SCALE: NTS | WT: | REV- 0