



NOTE : ~ PLEASE MAINTAIN 5 MM GAP BETWEEN TWO LIP BUSHES.

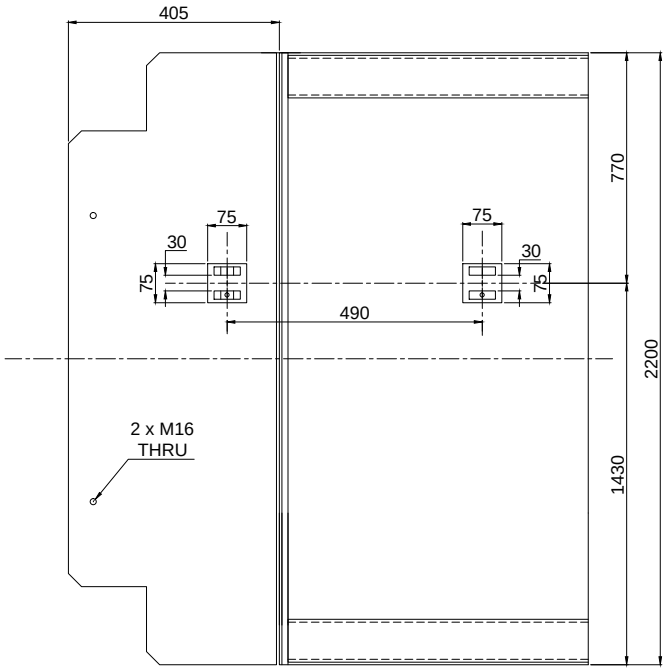

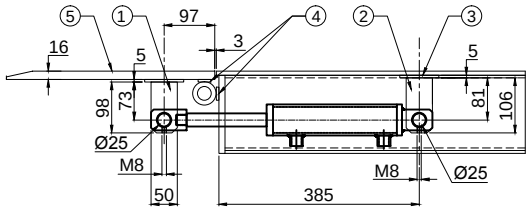


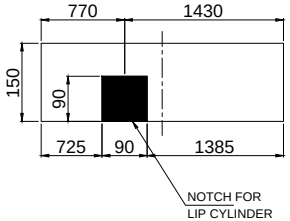

1

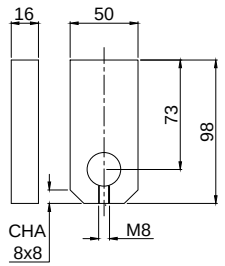

2

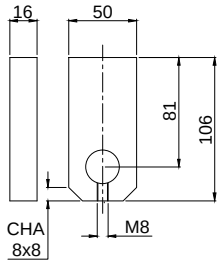

NOTE:~ MTL : MS

1. FLAT 50 X 20 X 102L = 2 NOS (SEE DRG)
2. FLAT 50 X 20 X 110L = 2 NOS (SEE DRG)
3. FLAT 75 X 5 X 75L = 2 NOS
4. FLAT 25 X 5 X 80L = 21 NOS
5. PROFILE LIP 400 X 16 X 2200L = 1 NO (SE DRG)

NOTE : ~ M16 DRILLING & TAPPING WILL BE DONE AT THE TIME OF ASSLY FOR LOCKING THE FLAP WHILE DOCK LEVELER INSTALLING.

TOLERANCE - ±5mm

This drawing & design is the property of NIHVA TECHNOLOGIES. Not to be sold or copied to any other concern.

TITLE: LIP CYL MOUNTING			NIHVA TECHNOLOGIES PVT. LTD. PUNE Tel : 020 66304033 Email:- info@nihva.com Website:- www.nihva.com
NAME	SIGN	DATE	
DRAWN P.A			CLIENT -
CHECK SHEKHAR			PROJECT - DLBJ1001
APPRD. SHEKHAR			SITE LOCATION -
If any queries contact : design@nihva.com			DWG. NO. : NIHVA/17-18/ REV- 0
ALL DIMENSION ARE IN mm			SCALE: NTS WT: SHEET: 01 OF 01