
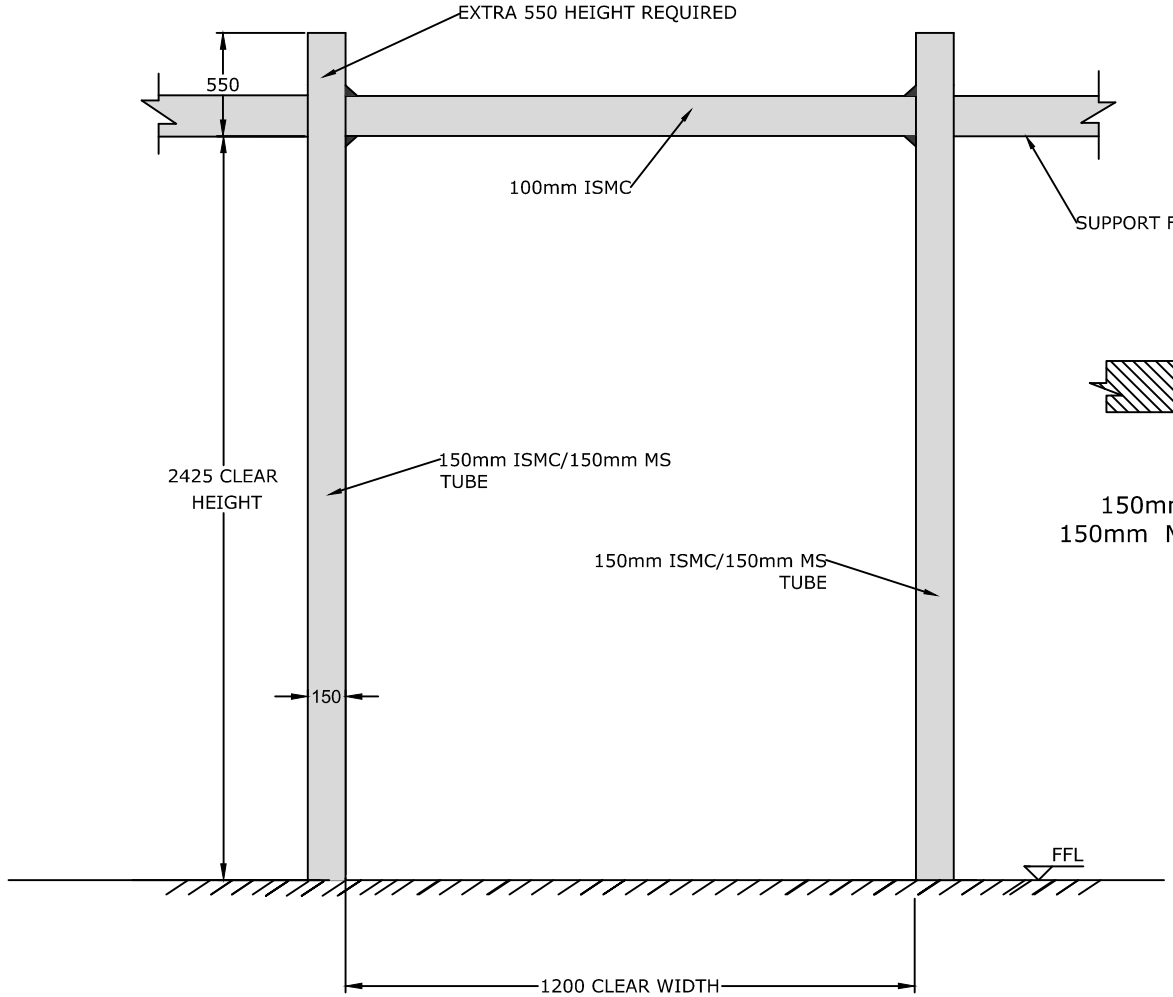


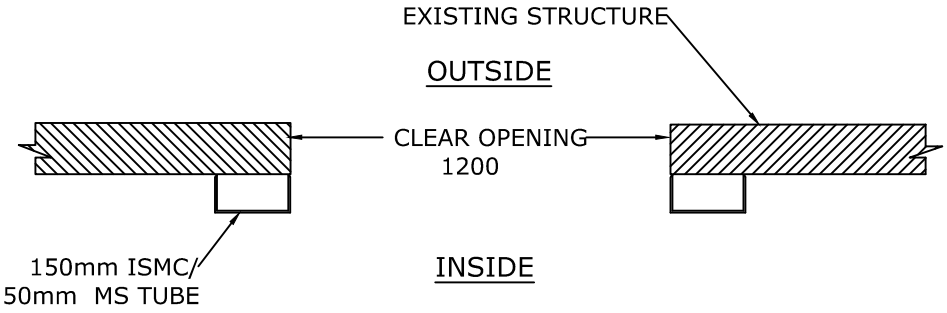

PLAN

CLEAR WIDTH (CW)	CLEAR HEIGHT (CH)	QUANTITY
1200	2425	1

This drawing & designing is the property of NIHVA TECHNOLOGIES. Not be sold or copy to any other concern.

TITLE

STRUCTURE FOR HIGH SPEED DOOR (RR 300 PLUS)

CLIENT APPROVAL

ALL DIMENSION ARE IN mm

	SIGN	DATE
DRAWN	OMKAR	12/08/16
CHECK	ANIL	12/08/16
ENG		
APPRD.		
MFG		
Ref. No.		

NIHVA TECHNOLOGIES PVT. LTD.

NIHVA TECHNOLOGY PVT. LTD. PUNE
Tel : 020 66304033
Email:- info@nihva.com
Website:- www.nihva.com

CLIENT - Tru-Tek systems combine pvt.ltd.

PROJECT-

SITE -

DWG. NO. - NIHVA/16-17/0053

SCALE: NTS | WT: | SHEET: 01

If any queries contact : projects@nihva.com