


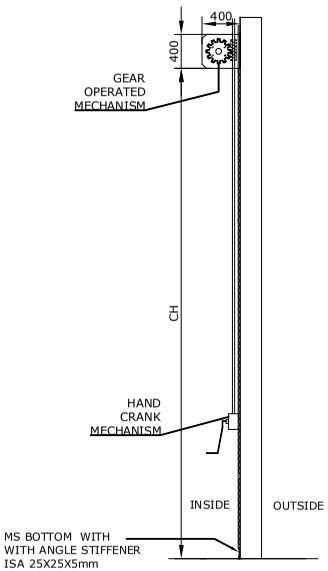


SIDE VIEW

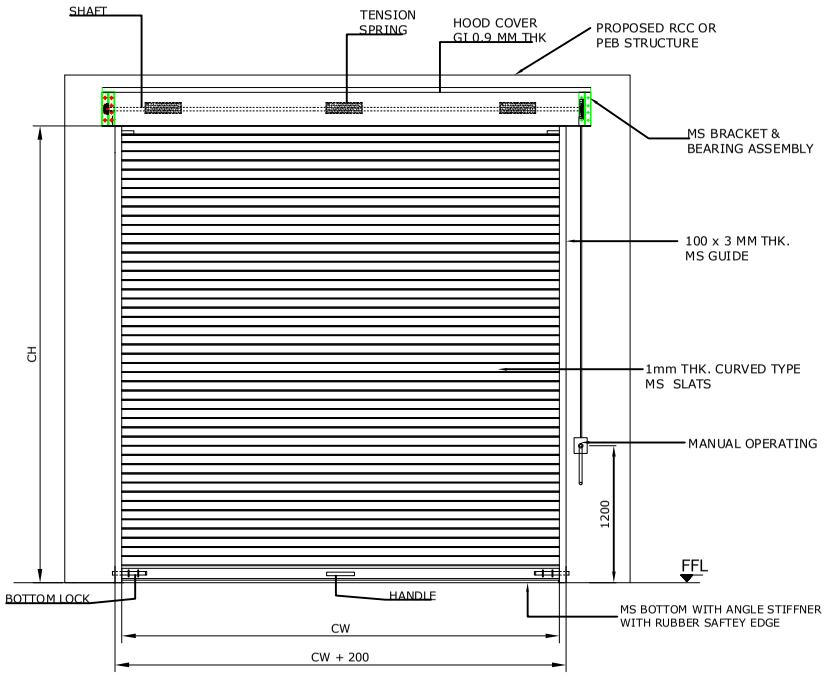

INSIDE ELEVATION

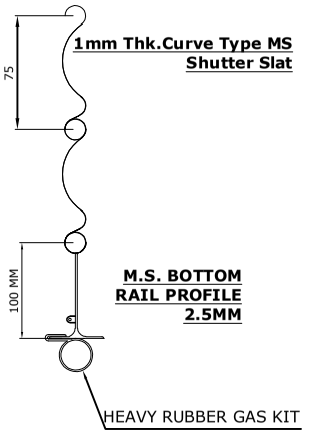

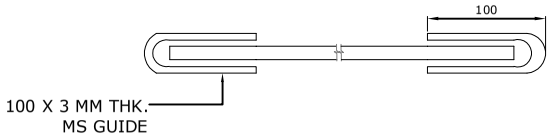



PLAN

NOTE-
1. All dimension are in MM.
2. Surface Finish: RAL CODE 9002
3.Mounting :On concrete column

SR NO	(CW) CLEAR WIDTH	(CH) CLEAR HEIGHT	QUANTITY
1	4500	3670	01 NO

TOLERANCE - ±10mm

This drawing & design is the property of NIHVA TECHNOLOGIES. Not to be sold or copied to any other concern.

TITLE
GEAR OPERATED ROLLING SHUTTER

	NAME	DATE	SIGN
DRAWN	Sujata	25.03.2022	
CHECK	G.I.P	25.03.2022	
APPRD.	P.J	25.03.2022	

If any queries contact : design@nihva.com

ALL DIMENSION ARE IN mm

NIHVA
NIHVA TECHNOLOGIES PVT. LTD.
NIHVA TECHNOLOGIES PVT. LTD. PUNE
Tel : 020 66304033
Website:- www.nihva.com
Email:- info@nihva.com

CLIENT -

PROJECT -GEAR OPERATED ROLLING SHUTTER

SITE LOCATION -

DWG. NO. : NIHVA/21-22/VDR/060 | REV- R0

SCALE: NTS | WT: | SHEET: 01 OF 01