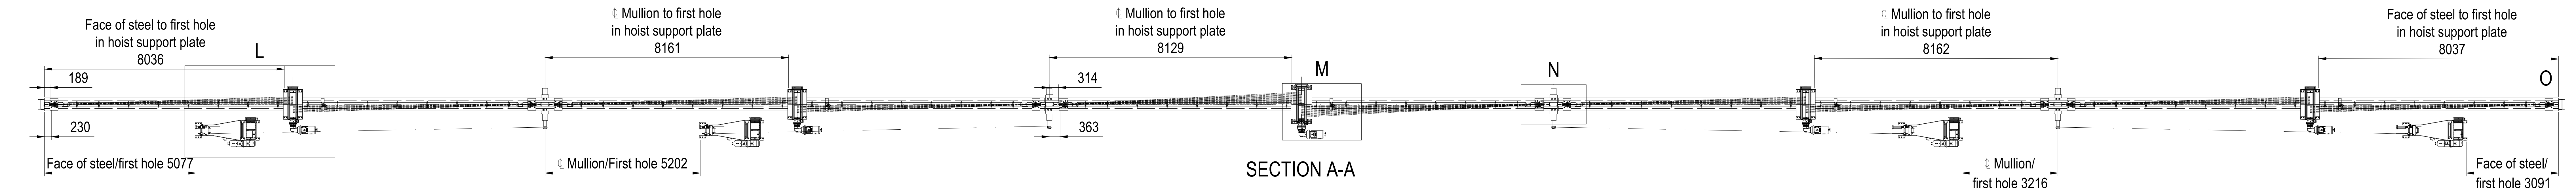

SECTION A-A

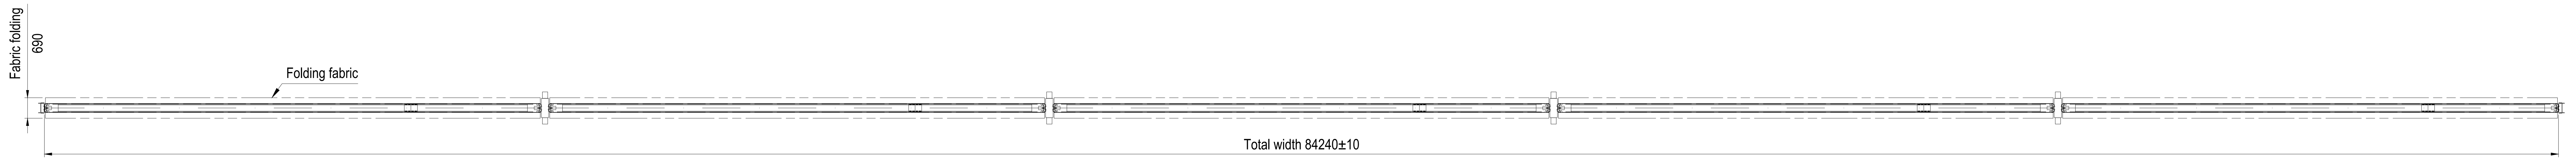

SECTION B-B

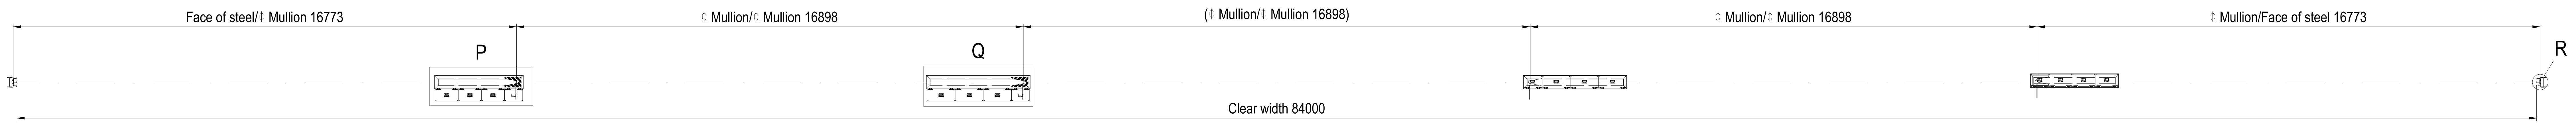
Face of steel/℄ Mullion 16773
℄ Mullion/℄ Mullion 16898
(℄ Mullion/℄ Mullion 16898)
℄ Mullion/℄ Mullion 16898
℄ Mullion/Face of steel 16773
P
Q
R
Clear width 84000

SECTION C-C

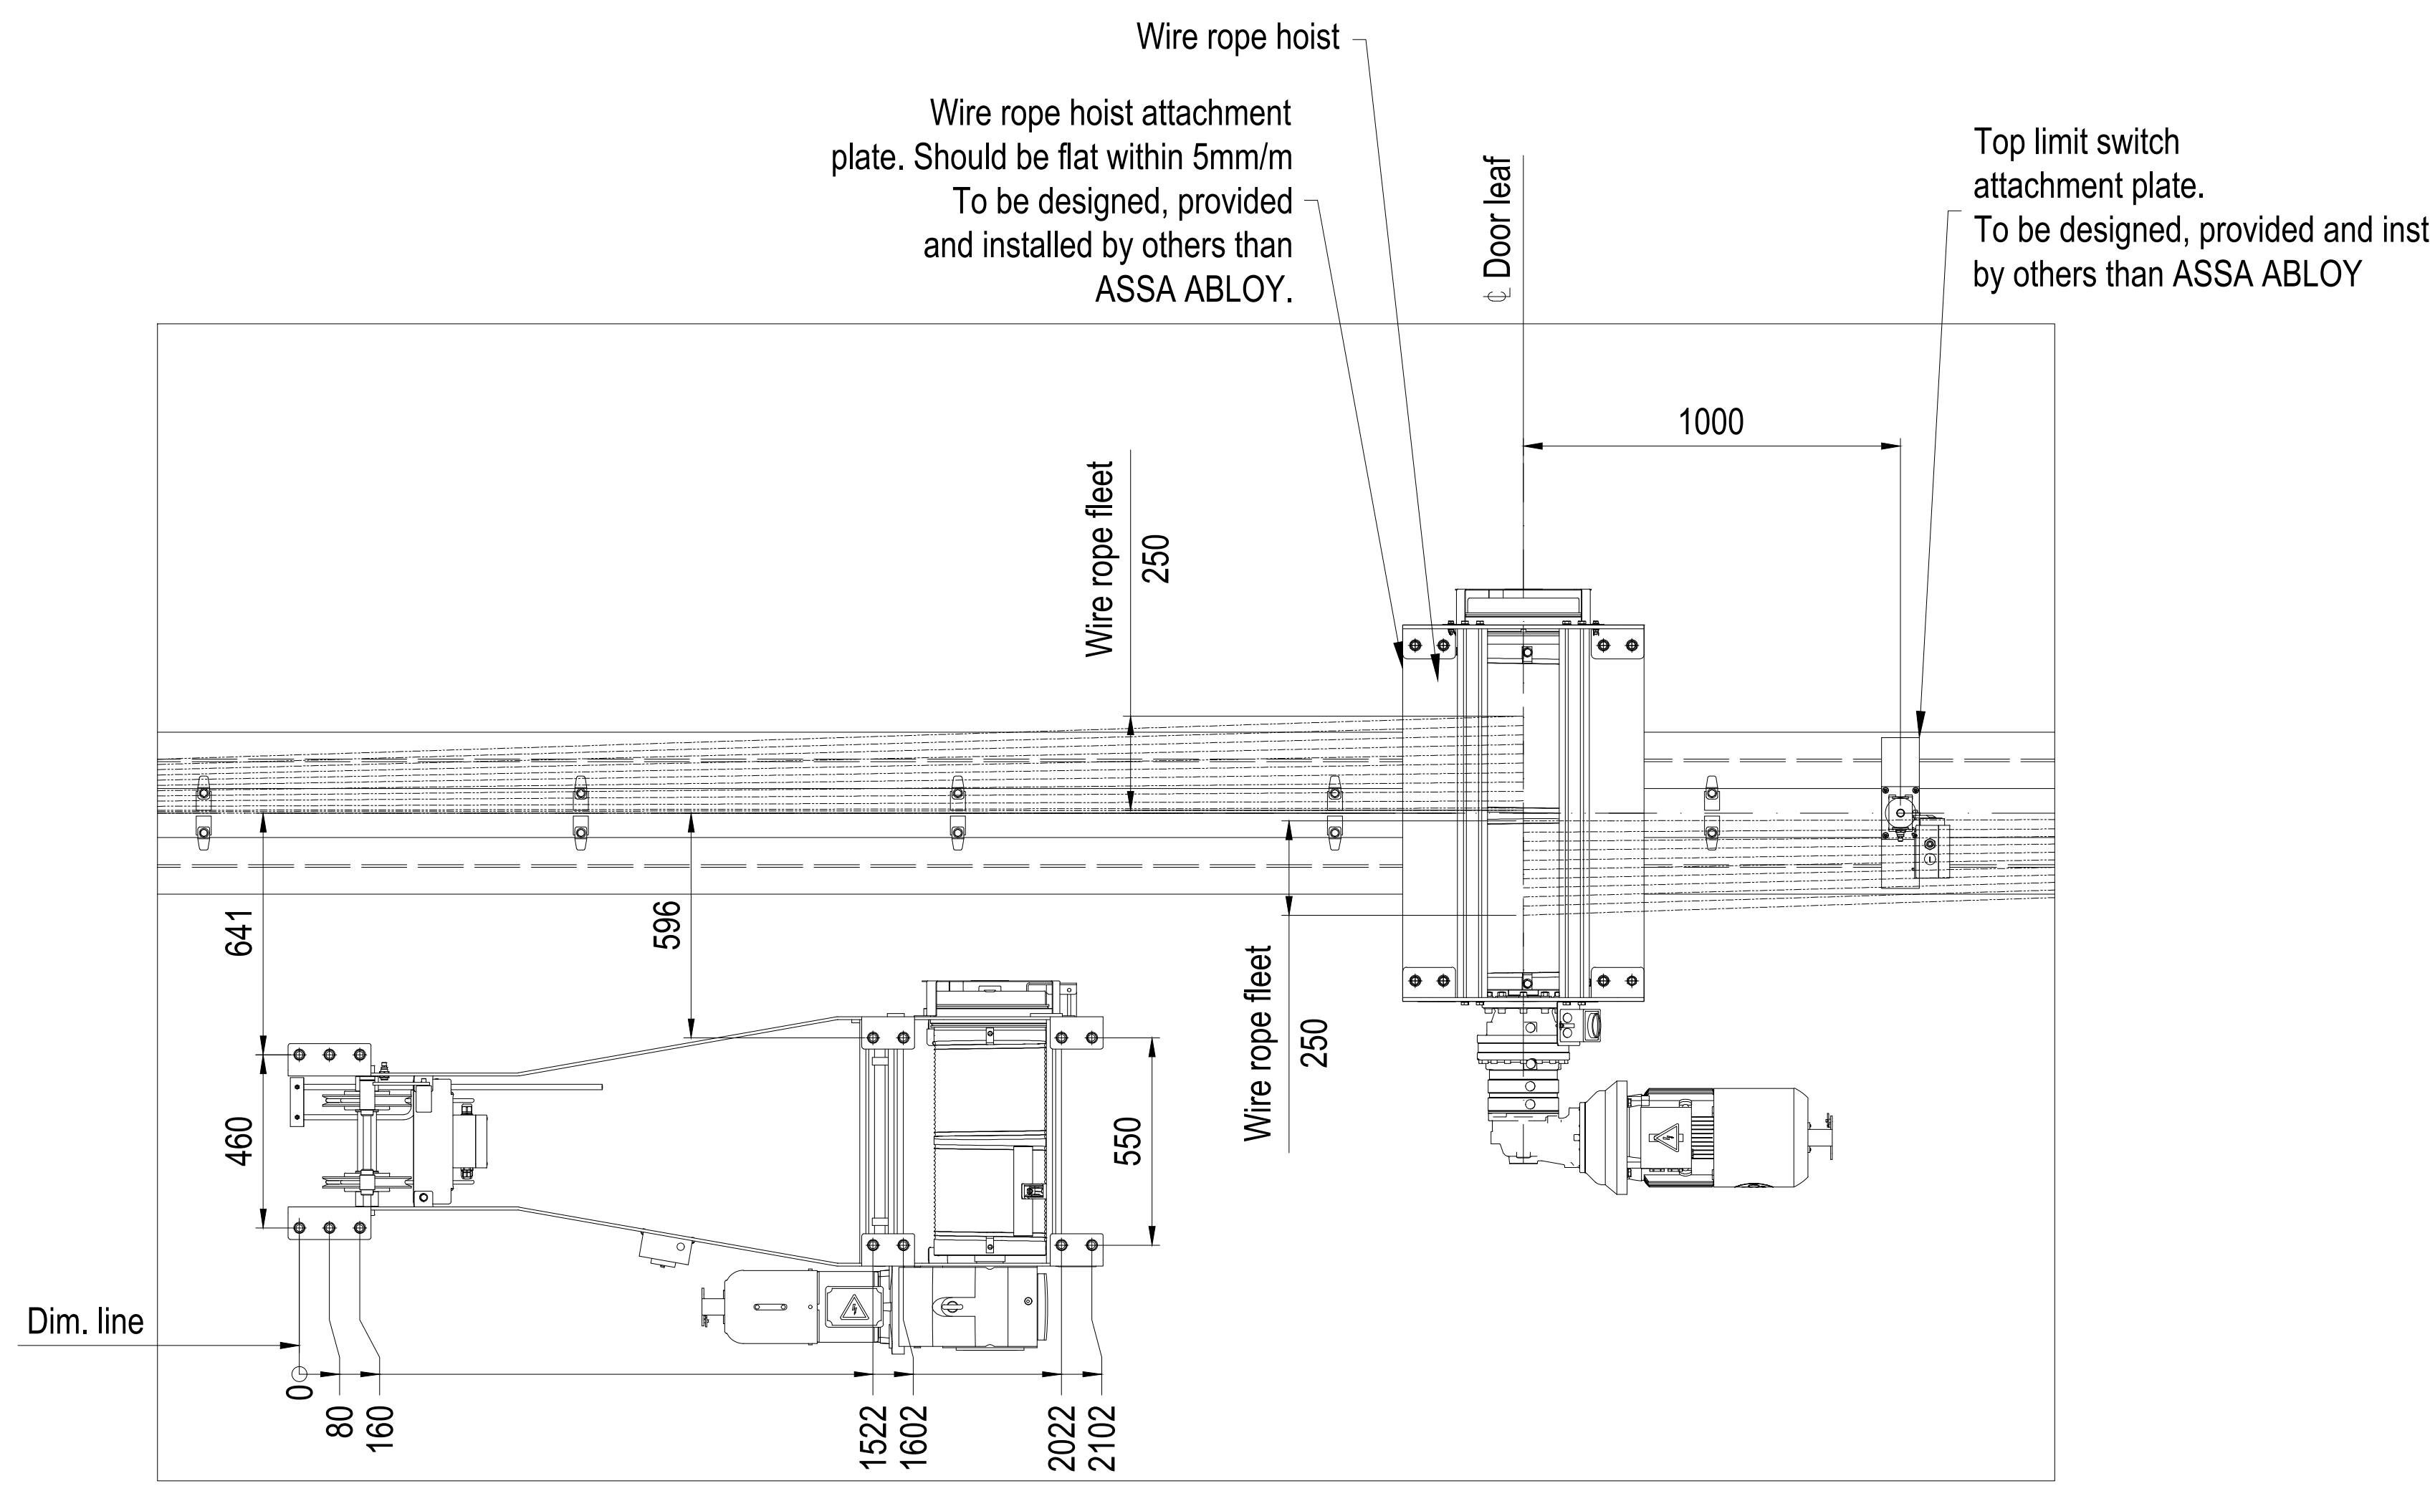

DETAIL L, SCALE (1:20)

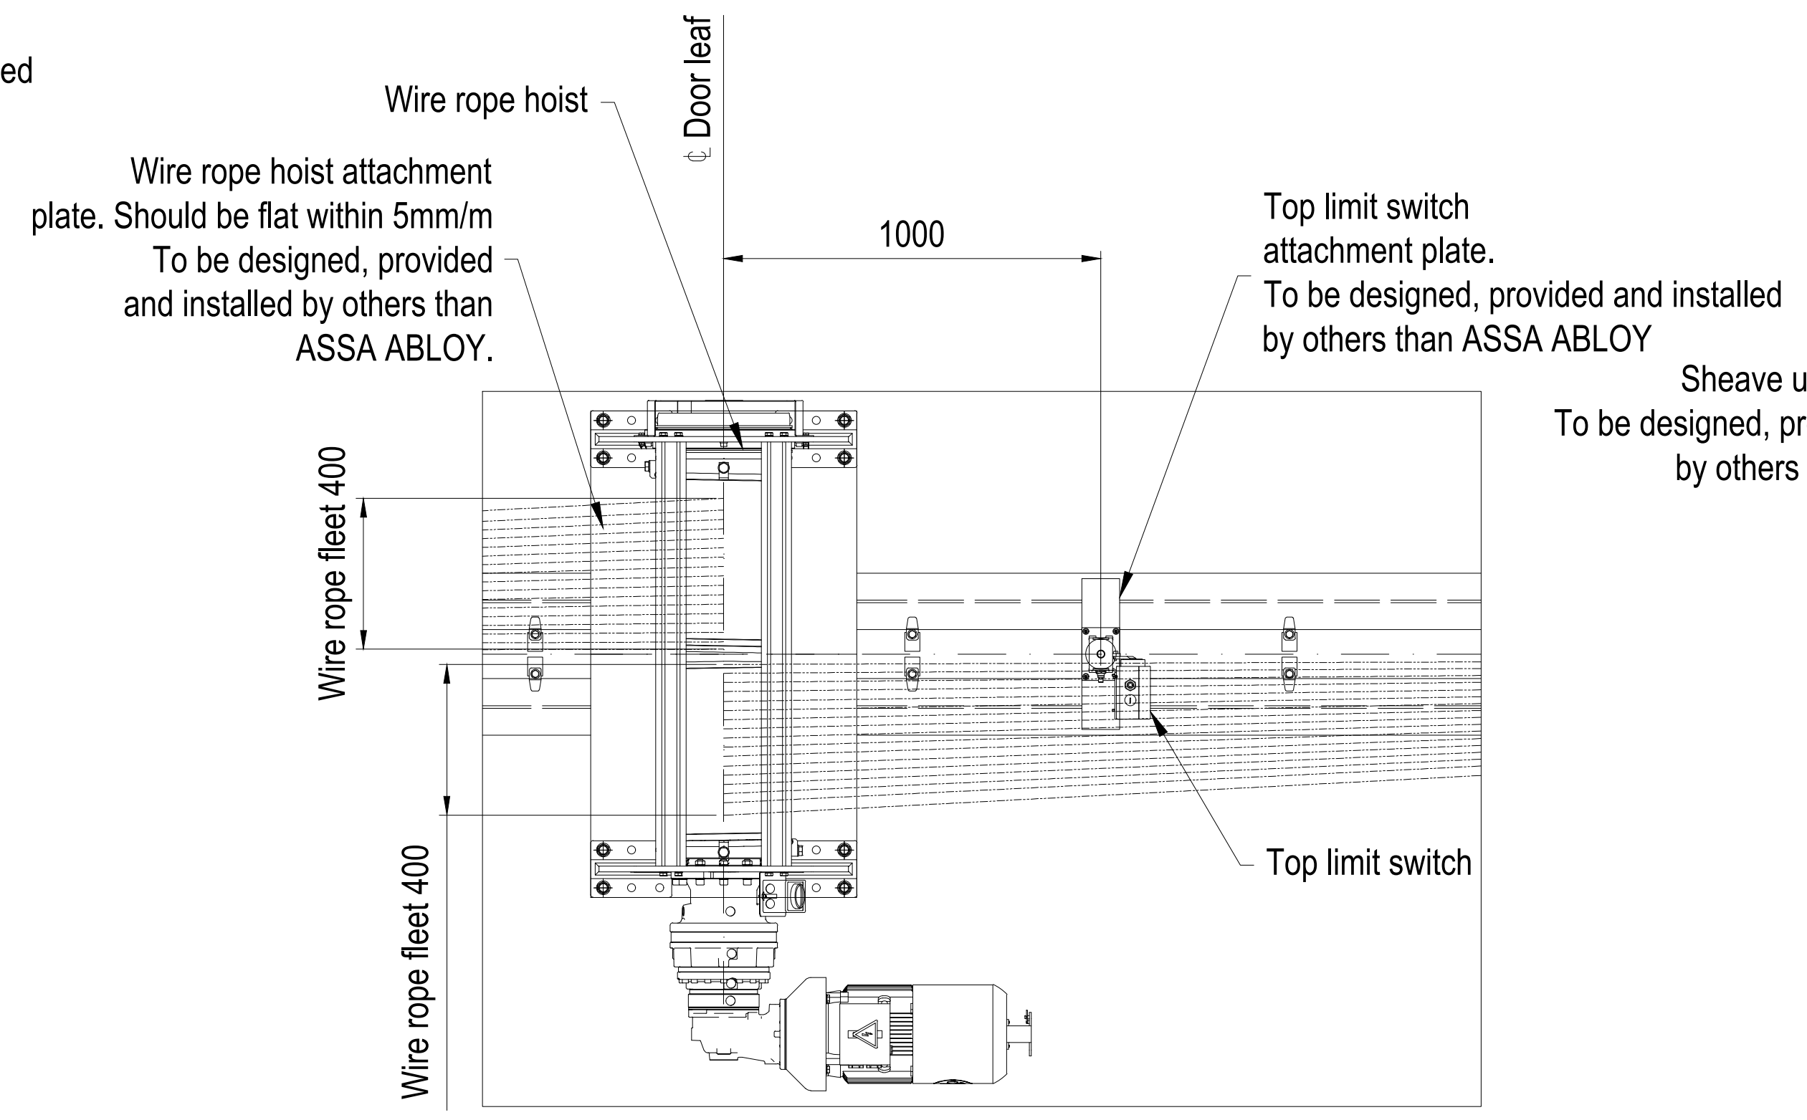

DETAIL M, SCALE (1:20)

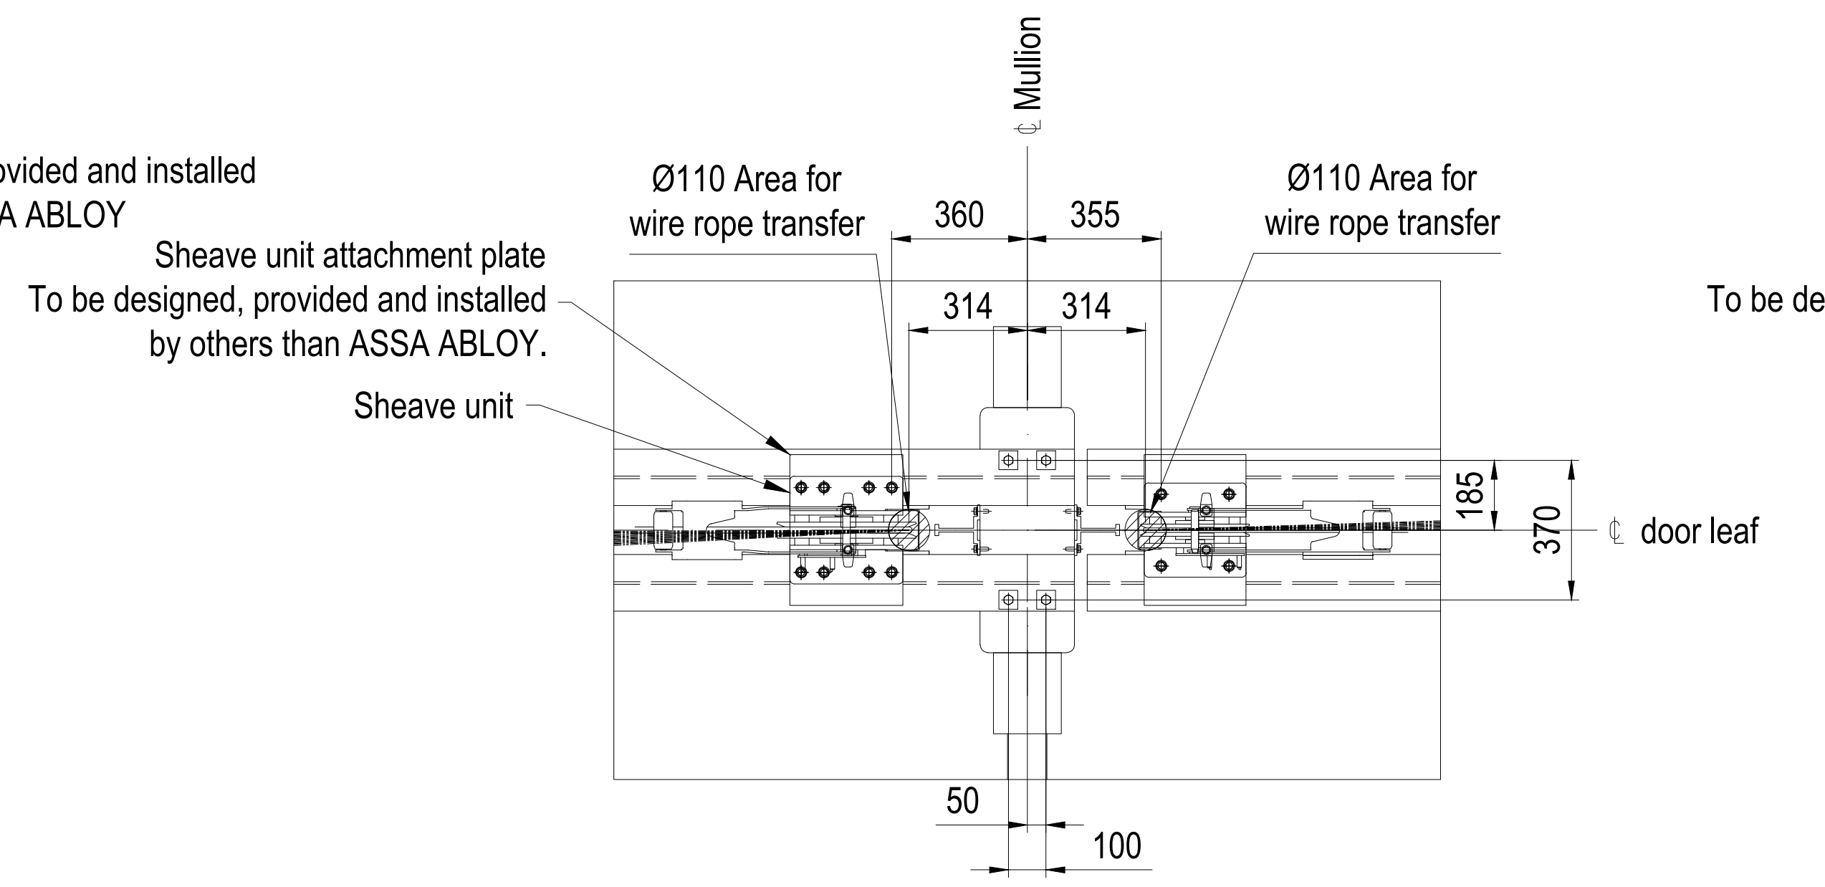

DETAIL N, SCALE (1:20)

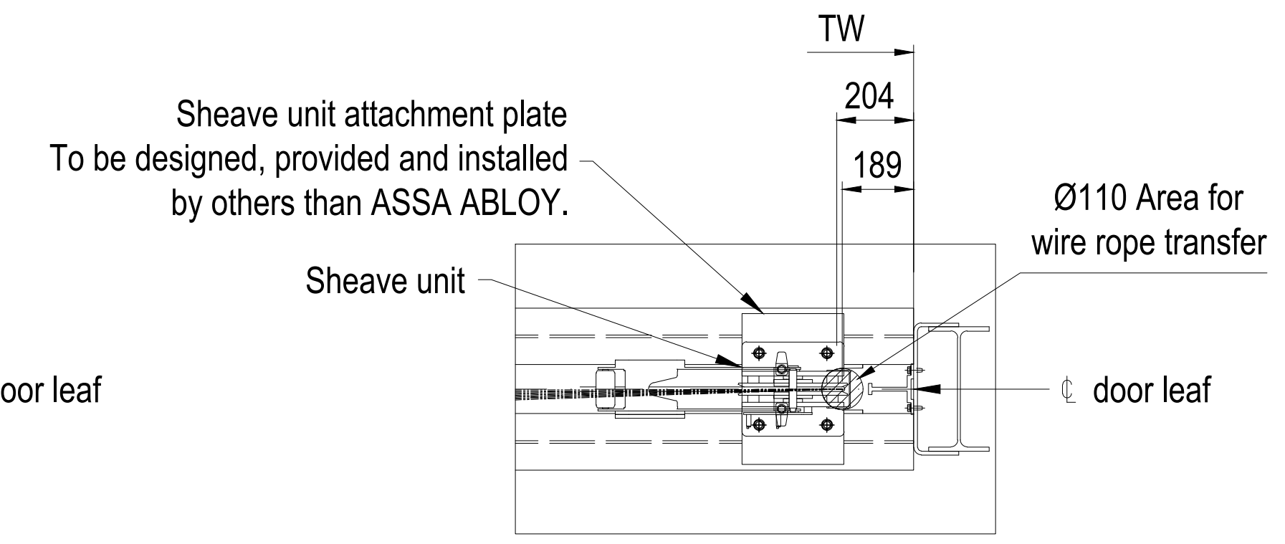
TW
204
189
Sheave unit attachment plate
To be designed, provided and installed
by others than ASSA ABLOY.
Ø110 Area for
wire rope transfer
Sheave unit
℄ door leaf

DETAIL O, SCALE (1:20)

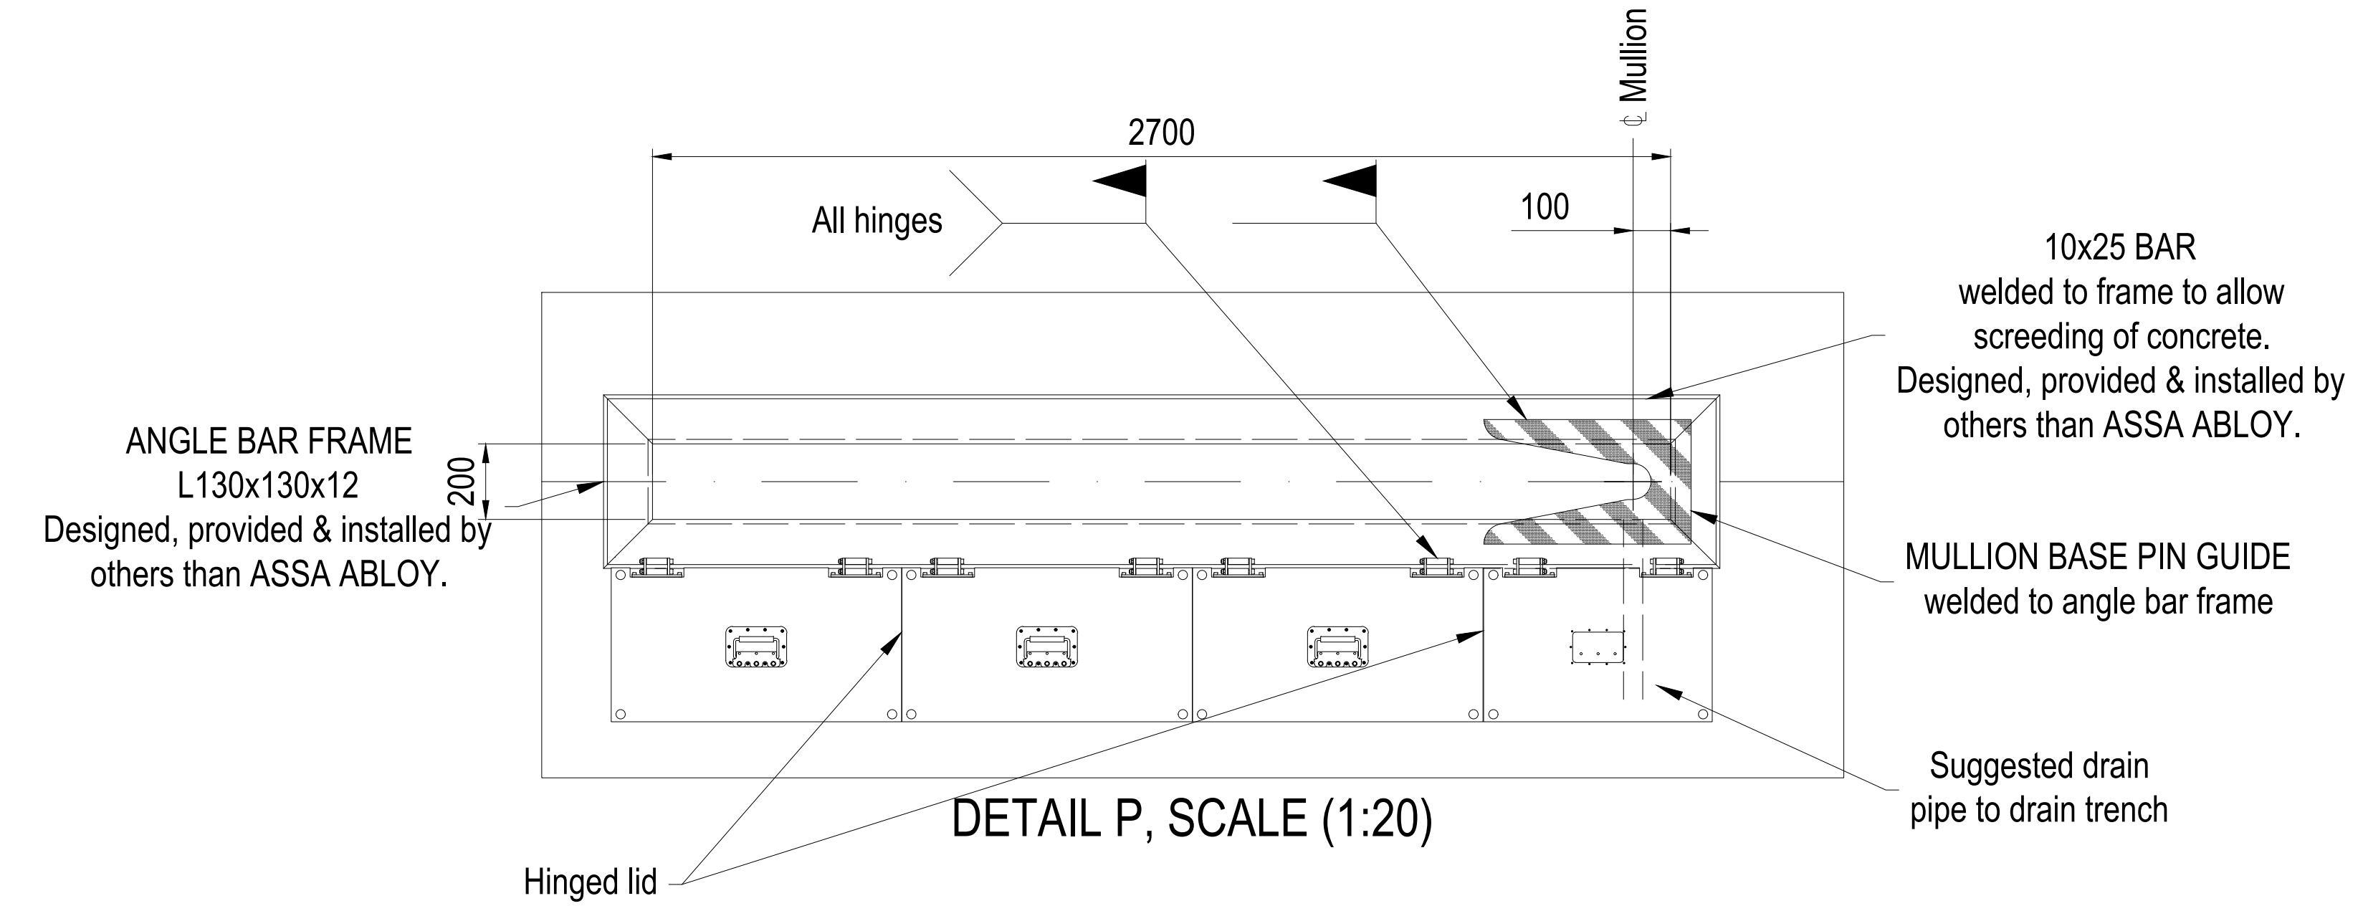

DETAIL P, SCALE (1:20)

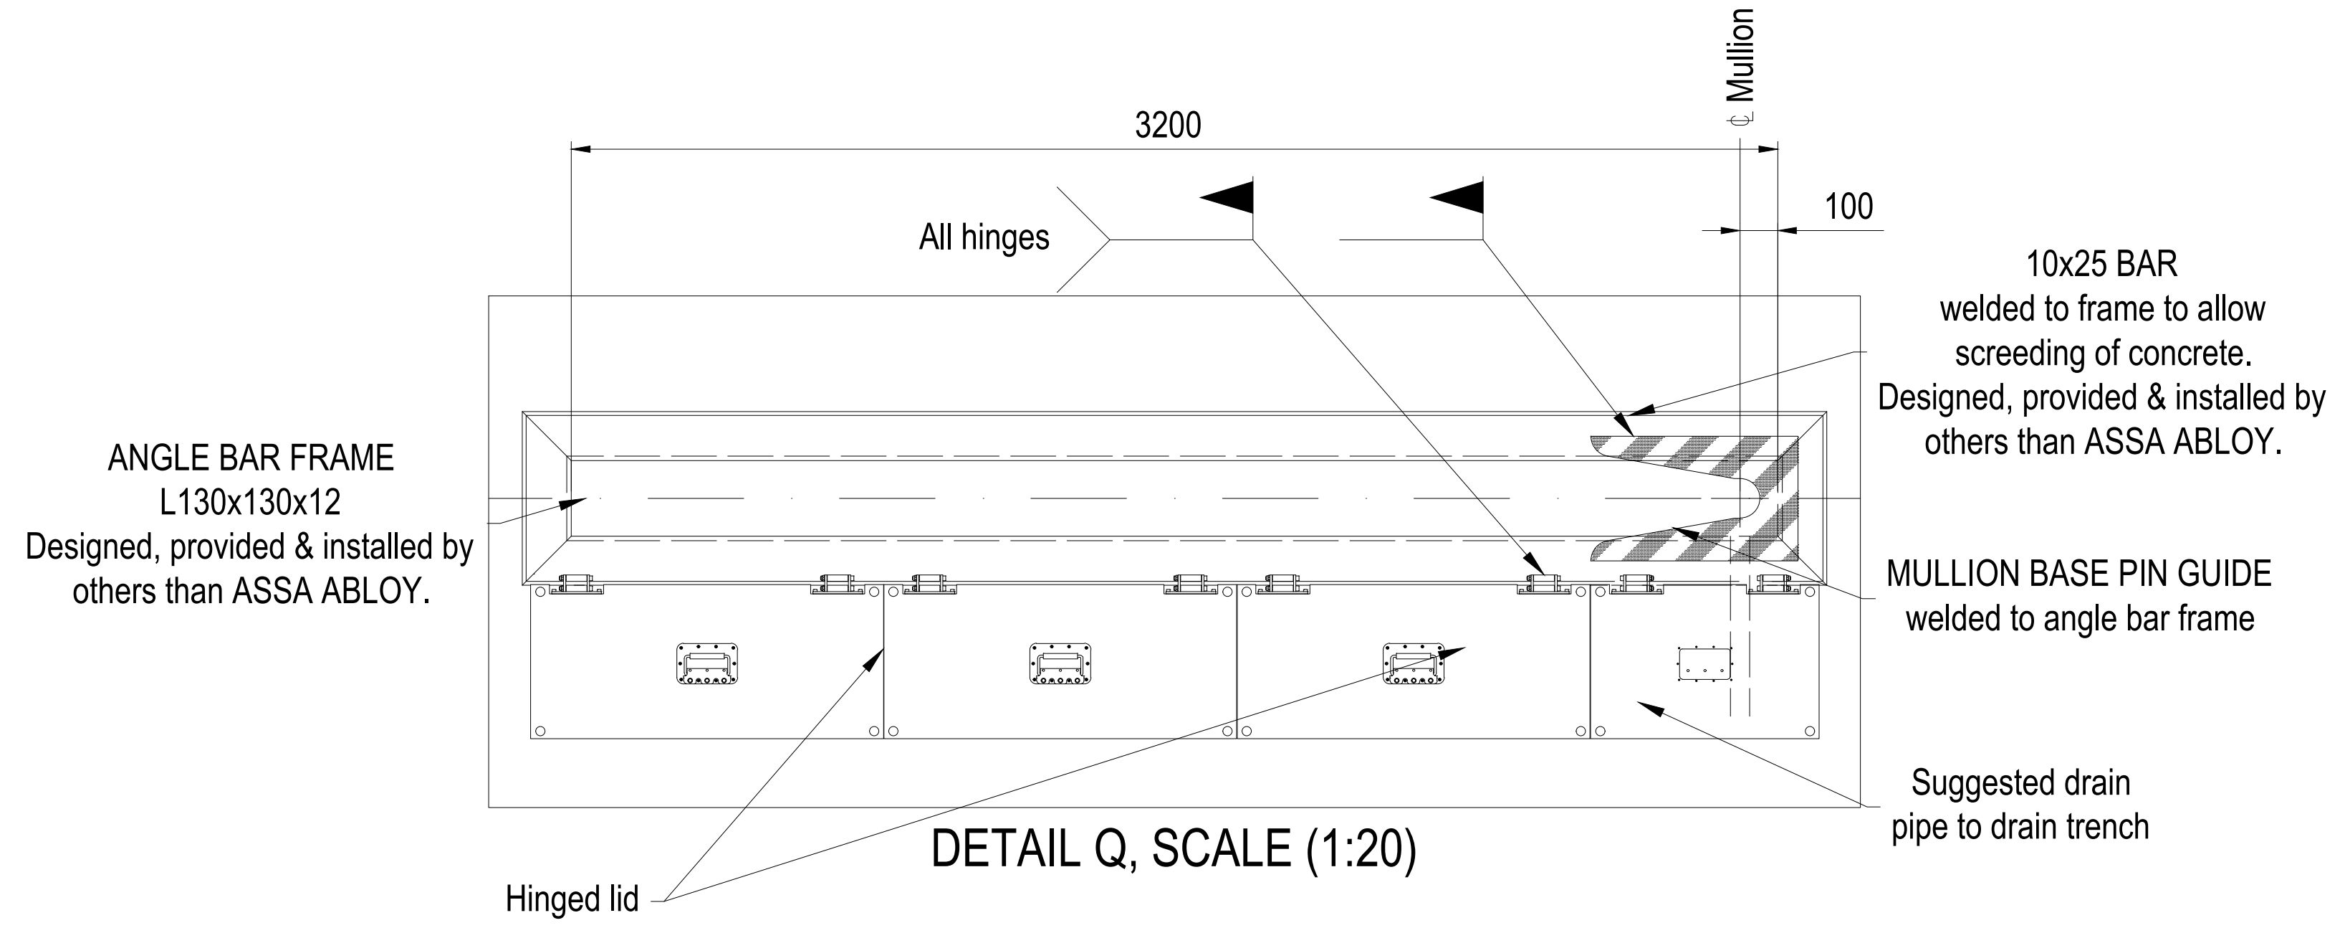

DETAIL Q, SCALE (1:20)

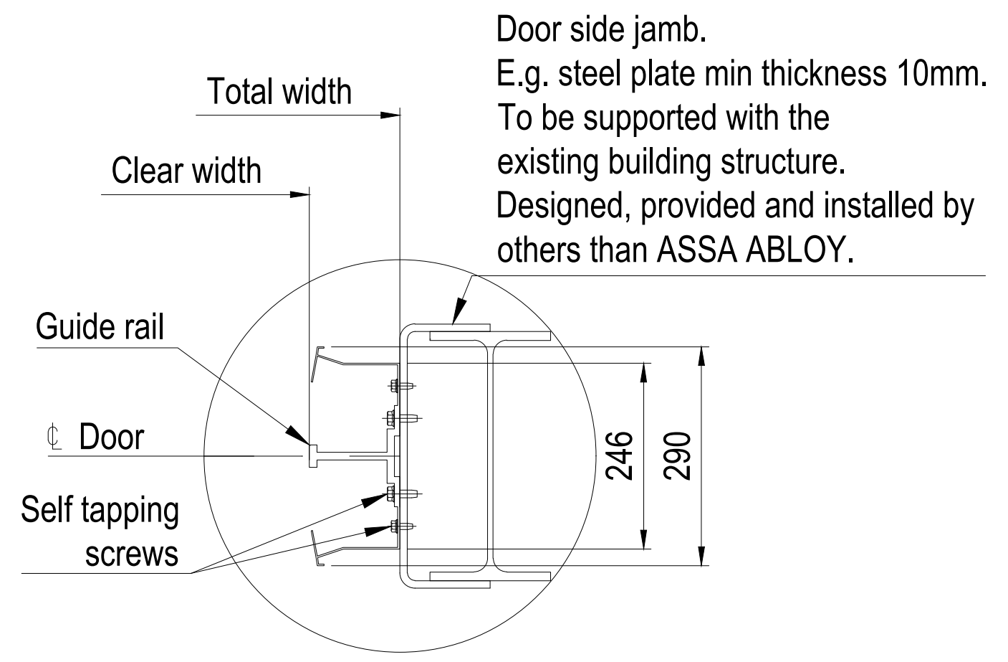

DETAIL R, SCALE (1:10)

DOOR IDENTITY NUMBER: 84800001

LOAD DIAGRAM & NOTES, ref. to drwng. no. 77446

INTERFACE, SECTIONS ref. to drwng. no. 77445

INTERFACE, ELEVATION ref. to drwng. no. 77443

DESIGNED EB	SIZE A1F	SCALE 1:100	GMR Aero Technic Hangar1 India Megadoor 84000x23000/14000 Interface, Plan views	PLOT DATE
CODE 84800	If not otherwise stated: Tolerances ISO 2768-m EN ISO 13920-B Cutting class ISO 9013-442 Weld class ISO 5817-C Surface finish Smooth raw surface			
ITEM NO				
DATE 2022-08-23			DRAWING NO 77444	REVISION --
ASSA ABLOY				

This document is the property of ASSA ABLOY Entrance Systems AB and shall not without our written permission be copied, imparted to a third party or used for any other unauthorized purpose.