

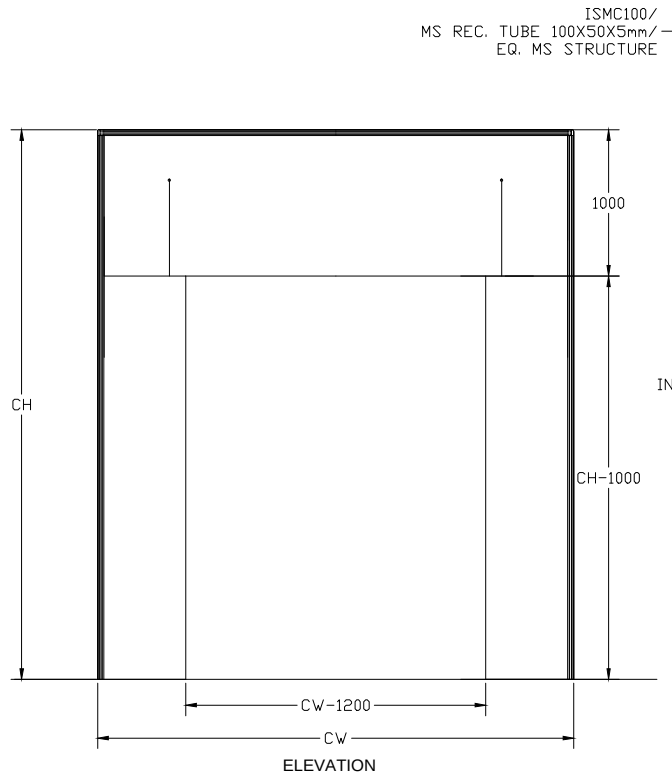



ELEVATION

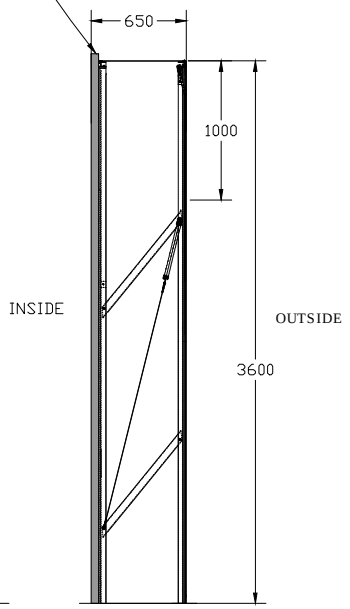

SECTION

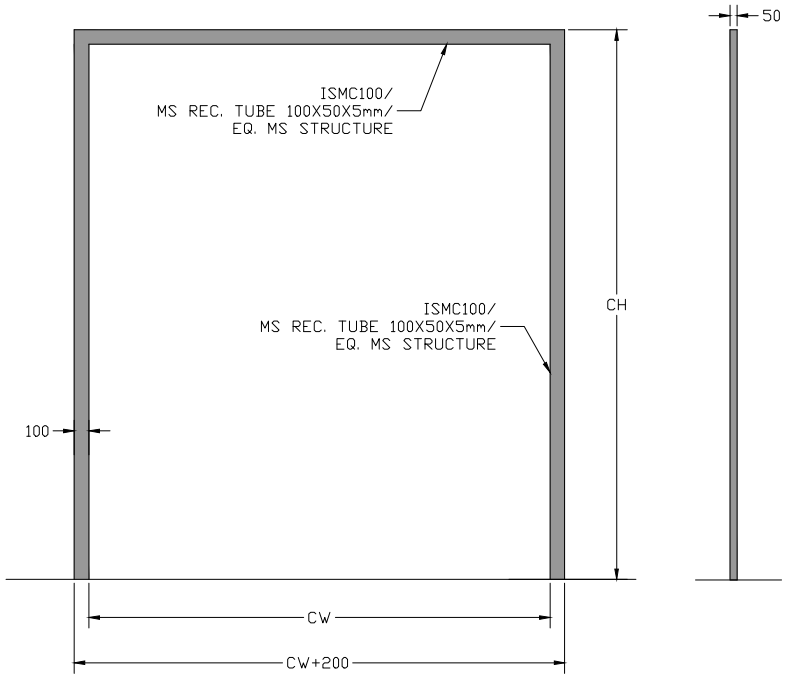

MS STRUCTRE

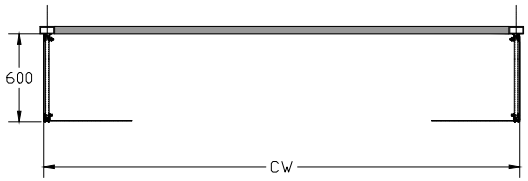

PLAN

STRUCTURE SIZE			
SR.NO	CLEAR WIDTH(CW)	CLEAR HEIGHT(CH)	QTY.
01.	3300	3650	01 NO

SHELTER SIZE			
SR.NO	CLEAR WIDTH(CW)	CLEAR HEIGHT(CH)	QTY.
01.	3400	3600	01 NO

NOTE:-ALL CIVIL WORKS AND STRUCTURES ARE CLIENT SCOPE

TOLERANCE - ±10mm

This drawing & design is the property of NIHVA TECHNOLOGIES. Not to be sold or copied to any other concern.

TITLE
DOCK SHELTER & MS STRUCTURE 1

NIHVA TECHNOLOGIES PVT. LTD.

NIHVA TECHNOLOGIES PVT. LTD. PUNE
Tel : 020 66304033
Email:- info@nihva.com
Website:- www.nihva.com

	NAME	SIGN	DATE
DRAWN	P.A		06.01.2020
CHECK	G.J		06.01.2020
APPRD.			

CLIENT - SYNERGY
PROJECT -
SITE LOCATION - CHAKAN
If any queries contact : design@nihva.com
DWG. NO. : NIHVA/19-20/0189 REV- 0
ALL DIMENSION ARE IN mm
SCALE: NTS WT: SHEET: 01 OF 01