




SIDE VIEW

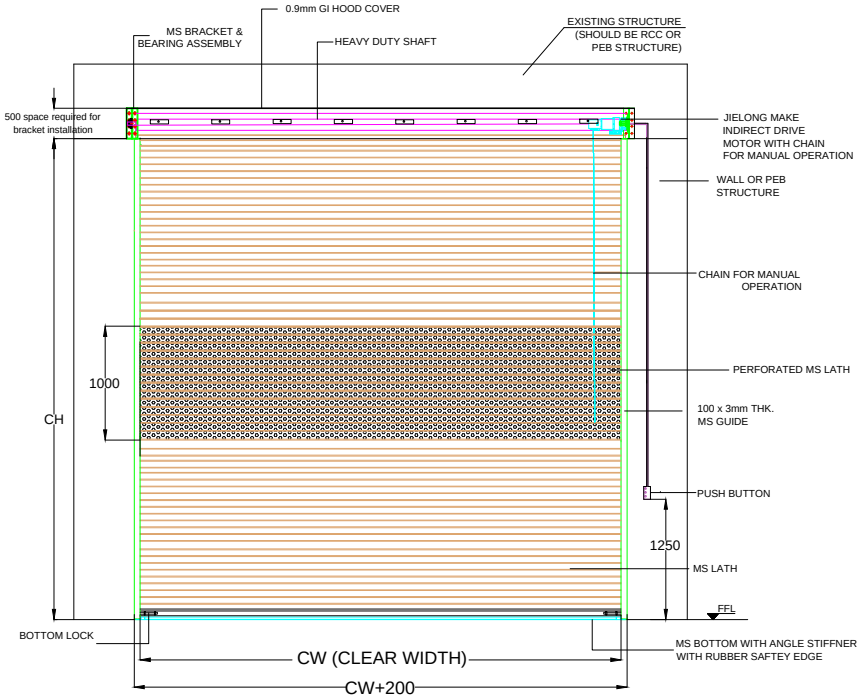


ELEVATION

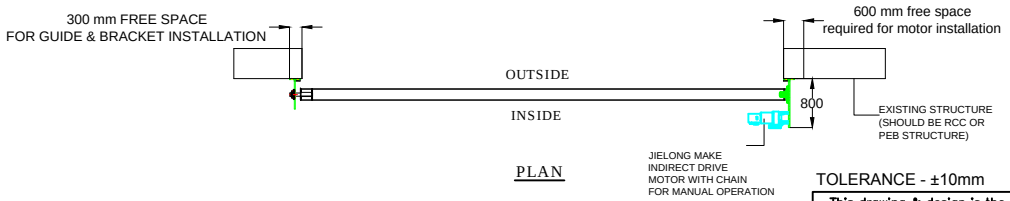


PLAN

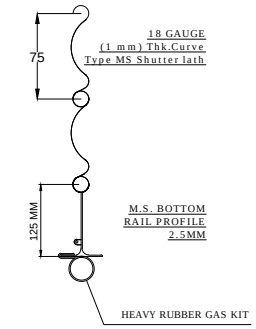

M.S. BOTTOM RAIL PROFILE 2.5MM

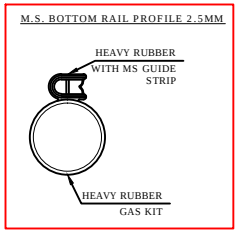

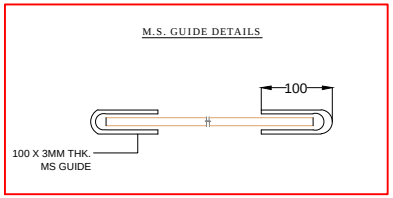

NOTE:
1 REQUIRED STRUCTURE FOR SHUTTER SHALL BE IN CLIENT SCOPE.
2.ONE COAT OF RED OXIDE PRIMER WILL BE GIVEN TO THE SHUTTER.
3.SINGLE PHASE. 3CORE 1.2SQ. CABLE REQUIRED AT SITE (CLIENT'S SCOPE)
4.COLOUR OF SHUTTER WILL BE RAL 7038 GREY

REV NO	DRAWN	DATE	REMARK
01	PRADEEP	19.10.2018	3. BOTTOM RUBBER PROFILE DETAIL ADD 2. GUIDE DETAIL ADD 1. MOTOR MAKE MENTION

CLEAR WIDTH	CLEAR HEIGHT	QTY.
4000mm	4000mm	01NOS

TOLERANCE - ±10mm

This drawing & design is the property of NIHVA TECHNOLOGIES. Not to be sold or copied to any other concern.

TITLE
MOTORISED ROLLING SHUTTER

	NAME	SIGN	DATE
DRAWN	SURAJ		12-10-2018
CHECK	PRADEEP		12-10-2018
APPRD.	R.D		12-10-2018

If any queries contact : design@nihva.com

ALL DIMENSION ARE IN mm

NIHVA TECHNOLOGIES PVT. LTD.
NIHVA TECHNOLOGIES PVT. LTD. PUNE
Tel : 020 66304033
Email:- info@nihva.com
Website:- www.nihva.com

CLIENT -VAICHAL CONSTRUCTION PVT. LTD

PROJECT - CNH

SITE LOCATION - CHAKAN

DWG. NO. : NIHVA/18-19/0144/R01 | REV- 01

SCALE: NTS | WT: | SHEET: 01 OF 01