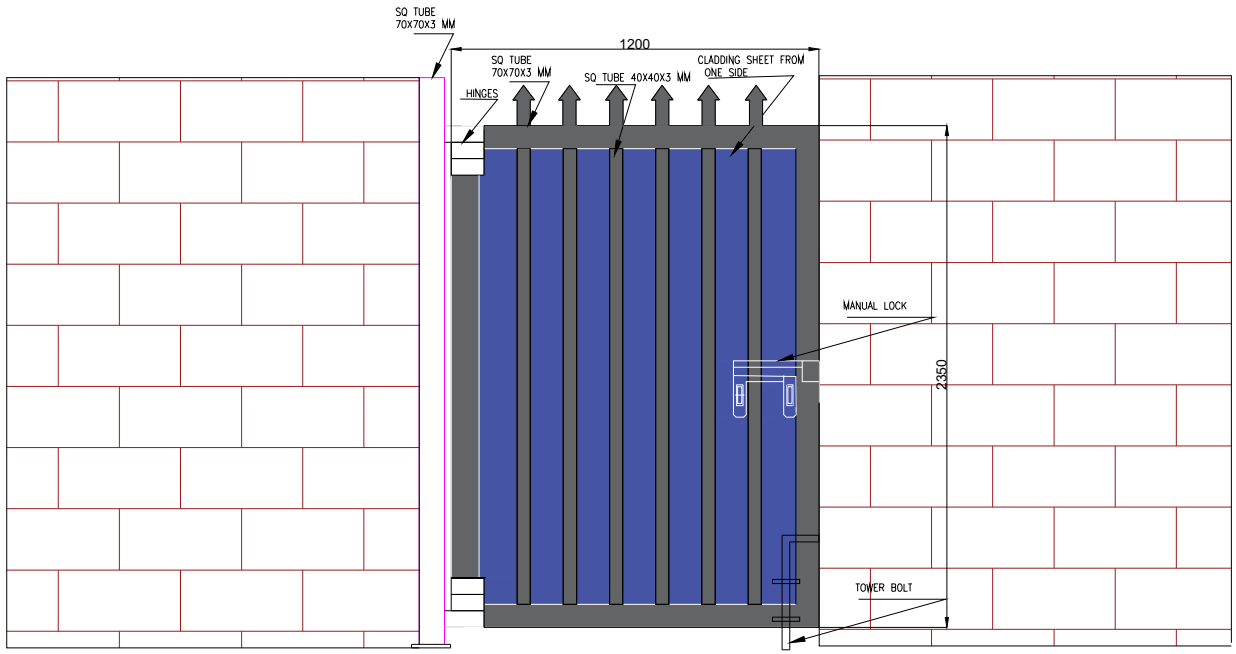


TECHNICAL SPECIFICATION:-

SR.	SPECIFICATION	DETAILS
1.	DOOR TYPE	MANUAL SINGLE LEAF WICKET GATE
2.	MOUNTING LOCATION AREA	INSIDE AREA
3.	OUTER FRAME & POST	SQ TUBE 70X70X3 MM
4.	INNEAR TUBE	SQ TUBE 40X40X3 MM
5.	GAP BETWEEN TUBES	100 MM C/C
6.	OPERATION	MANUALLY OPENING
7.	COLOUR	
8.	ACCESSORIES	HINGES,MANUAL LOACK & TOWER BOLT

GATE SIZES :-

SR.	CLEAR OPENING	CLEAR HEIGHT	QTY.
01	1200 mm	2350 mm	01

This drawing & design is the property of NIHVA TECHNOLOGIES. Not to be sold or copied to any other concern.

TITLE				NIHVA TECHNOLOGIES PVT. LTD. PUNE
WICKET GATES				Tel : 020 66304033 Email:- info@nihva.com Website:- www.nihva.com
	NAME	SIGN	DATE	
DRAWN	B.S		15.04.2026	CLIENT - CG POWER
CHECK	V.T		15.04.2026	PRODUCT - WICKRT GATES
APPRD.	V.T		15.04.2026	FORMAT NO - NIHVA-DD-F-03
If any queries contact : design2@nihva.com				DWG. NO. : NIHVA/26-27 / REV- R00
ALL DIMENSION ARE IN mm				SCALE: NTS / WT: / SHEET: