

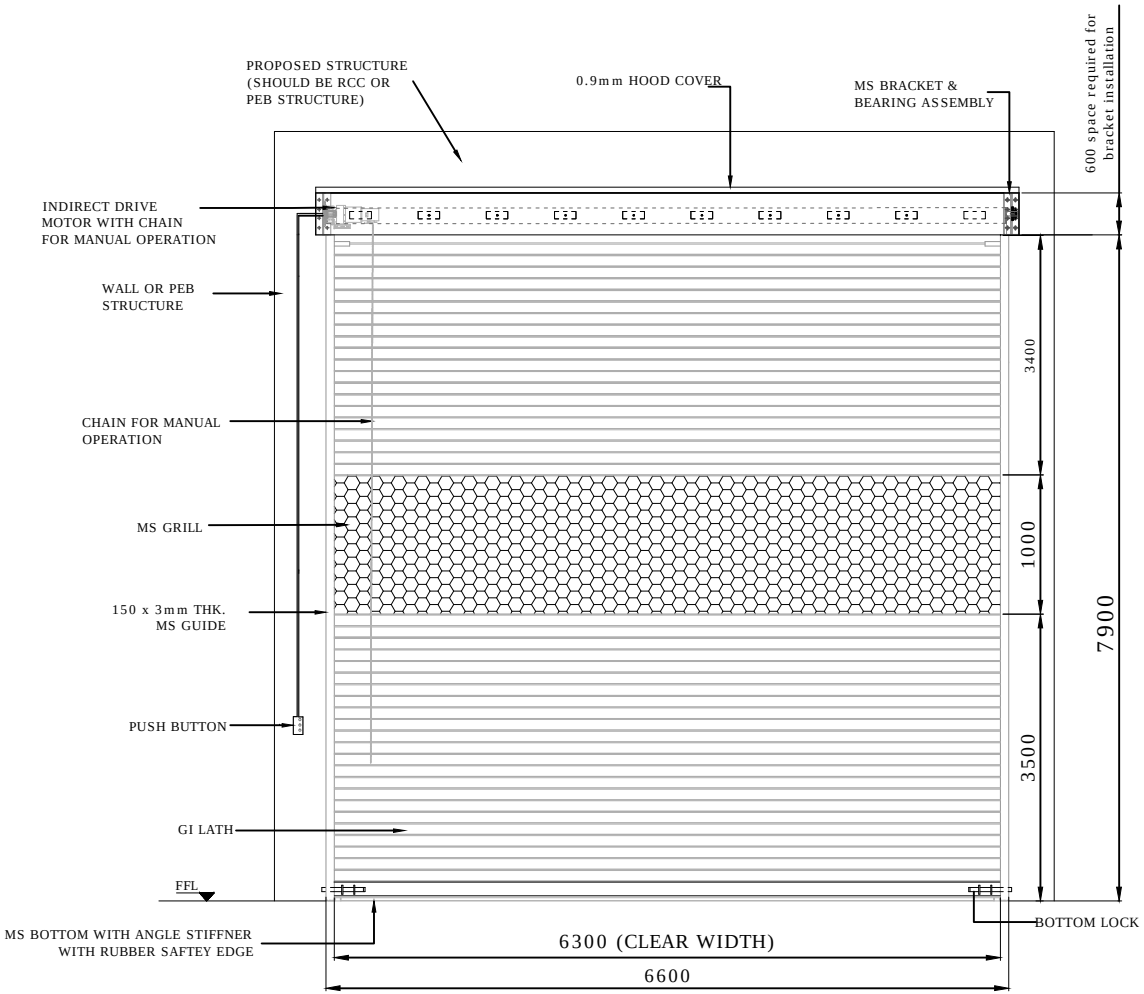



INSIDE ELEVATION

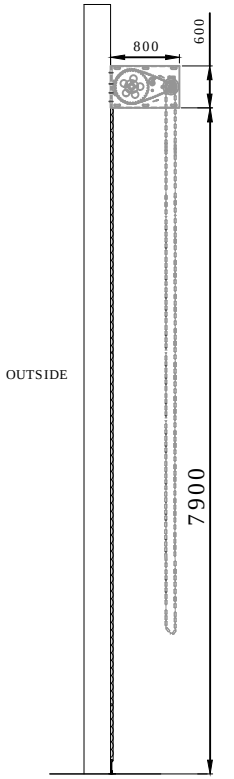


SIDE VIEW

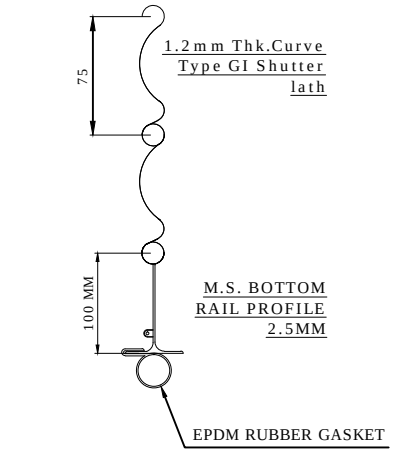

M.S. BOTTOM RAIL PROFILE 2.5MM

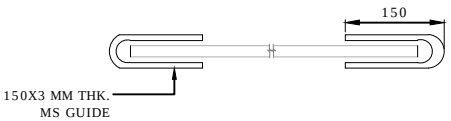

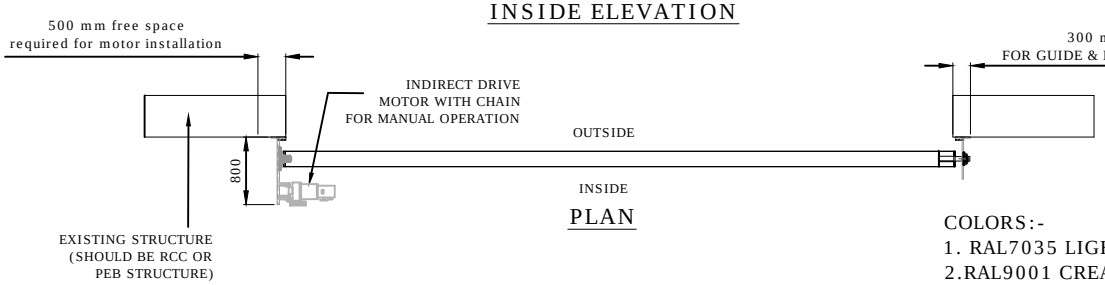

PLAN

NOTE:-
1.REQUIRED STRUCTURE FOR ROLLING SHUTTER SHALL BE IN CLIENT SCOPE.
2.ALL REQUIRED CIVIL WORK IN CLIENT SCOPE.
3.3 PHASE POWER SUPPLY SHOULD BE PROVIDED.
4.CLIENT HAS TO SELECT RAL COLOR SHADE FROM GIVEN OPTION.

COLORS:-
1. RAL7035 LIGHT GRAY.
2.RAL9001 CREAM WHITE.
3.RAL9010 PURE WHITE.

CLEAR WIDTH (CW)	CLEAR HEIGHT (CH)	QUANTITY
6300	7900	1

REVISION 1- SHUTTER SIZES HAS BEEN REVISED AS PER ACTUAL SITE CONDITIONS.

This drawing & designing is the property of NIHVA TECHNOLOGIES. Not to be sold or copied to any other concern.

TITLE: MOTORIZED ROLLING SHUTTER

NIHVA TECHNOLOGIES PVT. LTD. PUNE
Tel : 020 66304033
Email:- info@nihva.com
Website:- www.nihva.com

	SIGN	DATE
DRAWN	OMKAR	15/09/17
CHECK	SAGAR	15/09/17
APPROVAL	SHEKHAR	15/09/17
REV.		

CLIENT -S.S.GHORPADE
PROJECT -ROSS PROCESS EQUIPMENT PVT. LTD.
SITE -CHAKAN
DWG. NO. : NIHVA/17-18/0203/R01
If any queries contact : projects@nihva.com
SCALE: NTS | WT: | SHEET: 01 OF 01
ALL DIMENSION ARE IN mm