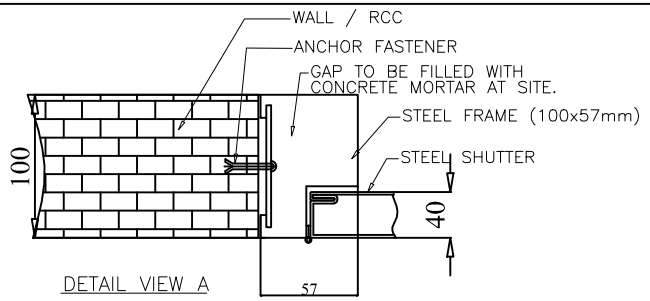


DETAIL VIEW A

NOTES:–
ALL DIMENSIONS ARE IN MM.

NOTES:–
ALL DIMENSIONS ARE IN MM.

A. ABBREVIATION

Wall Opening Width : WOW
Wall Opening Height : WOH
Frame Opening Height : FOH
Frame Opening Width : FOW
Shutter Opening Height : SOH
Shutter Opening Width : SOW

MATERIAL OF CONSTRUCTION


FRAME : G.I. 1.20mm Sheet
SHUTTER : G.I. 0.80mm Sheet
THICKNESS : 40MM
FRAME PROFILE : 100 x 57Mm (Single Ribet)

INFILL MATERIAL : MINERAL WOOL
DENSITY 48kg/cm3

PAINT: AS PER AS APPROVED RAL SHADE
POWDER COATED (DFT 80 Microns min)


SCHEDULE OF HARDWARE

1) S.S. Ball Bearing Hinges - 3 NOS (GEZE Make) .
2) Panic Bar for Single Leaf door YALE MAKE - 1 NO
3) External Trim Bar (Panic latch) YALE MAKE -1 Nos
4) Heavy Duty Door Closer GEZE MAKE -1 Nos
5) Anchor Fastener - 8 x 80MM.

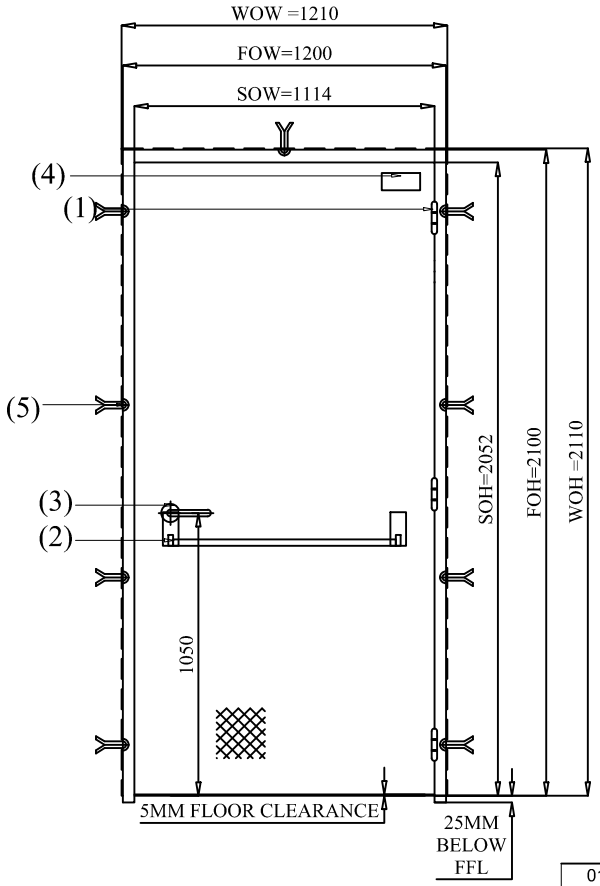

Door Opening Style - (B)
Right Hand Outside Opening

FOR PANIC BAR DOOR CHOOSE THIS STYLE ONLY

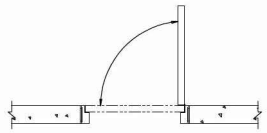

PUSH SIDE
(PANIC BAR)
PLANT INSIDE

PLEASE NOTE : Wall Openings to be maintained at site

SR. NO	WALL OPENING WIDTH	WALL OPENING HEIGHT	QTY	RAL
01	1200	2100	09	3020

TOLERANCE - ±02mm

This drawing & design is the property of NIHVA TECHNOLOGIES. Not to be sold or copied to any other concern.

TITLE	NAME	SIGN	DATE	
SINGLE LEAF STEEL DOOR				NIHVA TECHNOLOGIES PVT. LTD. PUNE Tel : 020 66304033 Email:- info@nihva.com Website:- www.nihva.com
DRAWN	P.A		08.01.2020	CLIENT - SYNERGY
CHECK	G.J		08.01.2020	PROJECT - EMBASSY
APPRD.				SITE LOCATION - CHAKAN, PUNE.
If any queries contact : design@nihva.com				DWG. NO. : NIHVA/19-20/0195 REV- R00
ALL DIMENSION ARE IN mm				SCALE: NTS WT: SHEET: 01 OF 01