


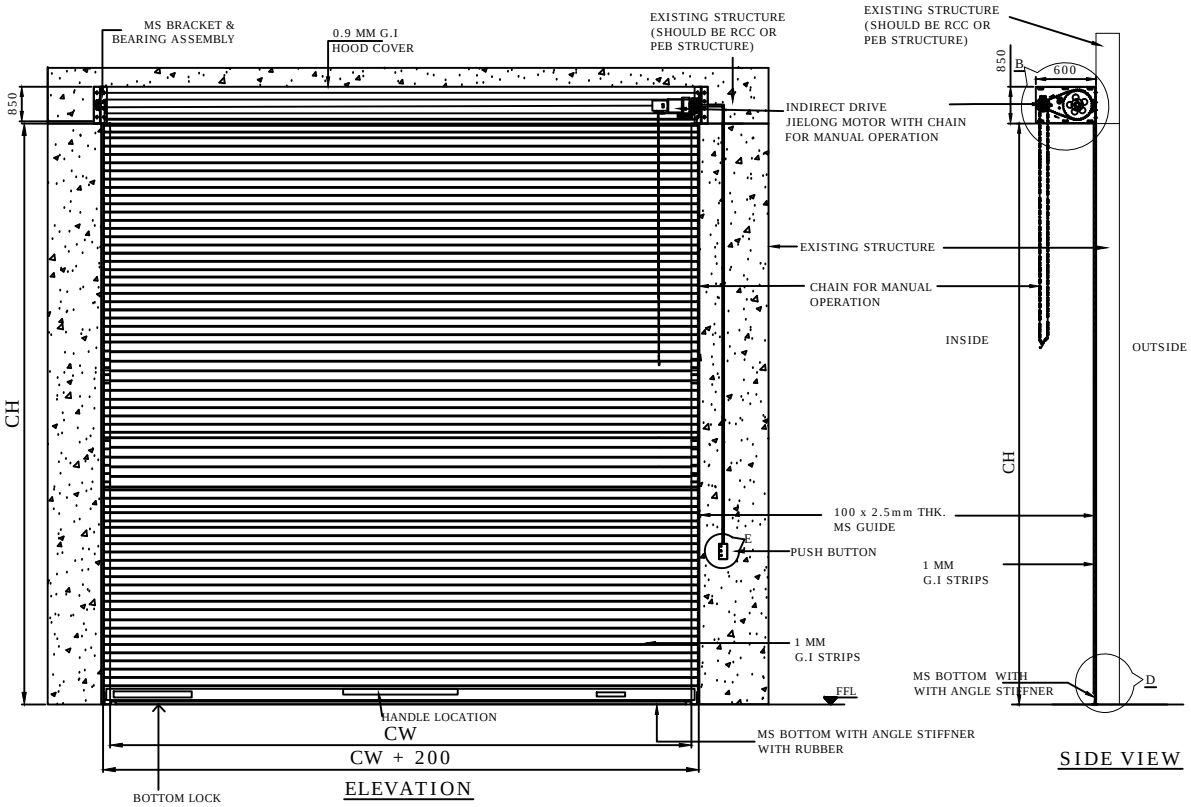


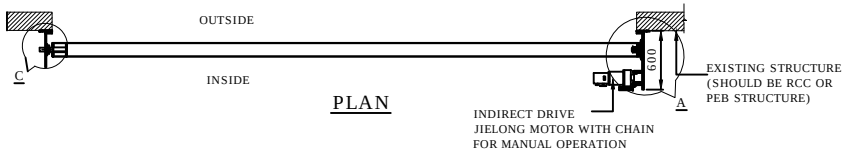


PLAN

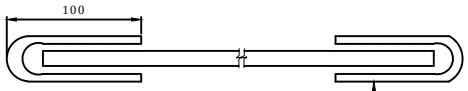


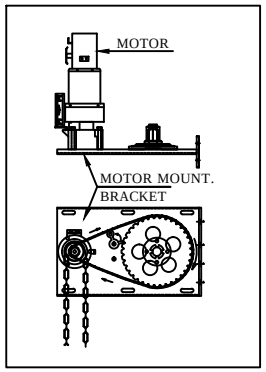

DETAILS : A & B

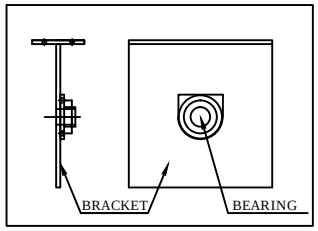

DETAILS : C

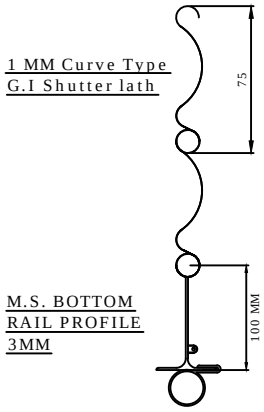

DETAILS : D

(NOTE: IF REQUIRED TECHNICAL STRUCTURE FOR SHUTTER IS IN CLIENT SCOPE)

CLEAR WIDTH (CW)	CLEAR HEIGHT (CH)	QUANTITY	STD RAL CODE	APPROVED
3000	3000	1 NOS	RAL 3001	
			RAL 7035	
			RAL 5002	
			RAL 9010	

This drawing & design is the property of NIHVA TECHNOLOGIES. Not to be sold or copied to any other concern.

TITLE	MOTORIZED ROLLING SHUTTER			NIHVA TECHNOLOGIES PVT. LTD. PUNE
	NAME	SIGN	DATE	Tel : 020 66304033
DRAWN	S.S.		28.09.2020	Email:- info@nihva.com
CHECK	P.A		28.09.2020	Website:- www.nihva.com
APPRD.				CLIENT - A R CONSTRUCTION
				PROJECT - MOTORISED ROLLING SHUTTER
				SITE LOCATION - PUNE
If any queries contact : design@nihva.com				DWG. NO. : NIHVA/20-21/0057 REV- R00
ALL DIMENSION ARE IN mm				SCALE: NTS WT: SHEET: