

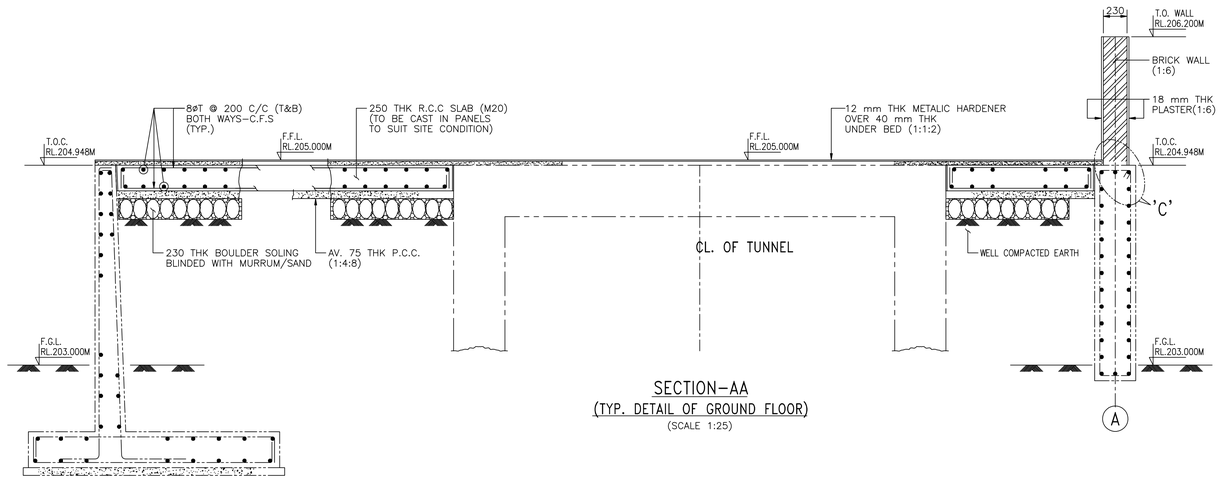



SECTION–AA
(TYP. DETAIL OF GROUND FLOOR)
(SCALE 1:25)

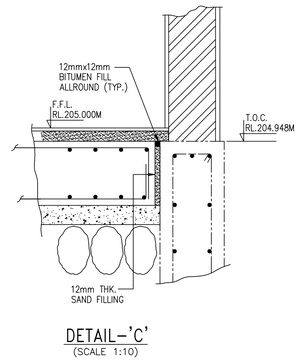


DETAIL–'C'
(SCALE 1:10)

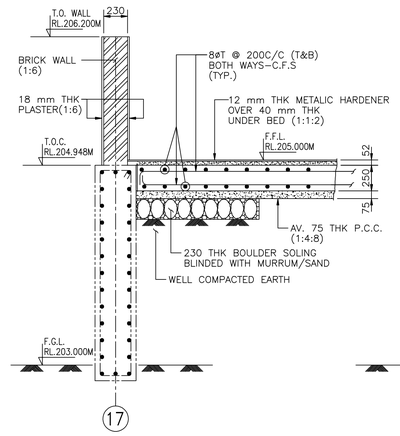

SECTION–BB
(SCALE 1:25)

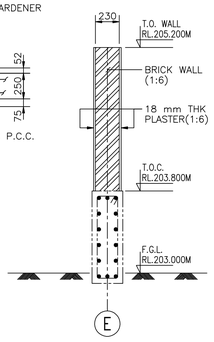

SECTION–CC
(SCALE 1:25)

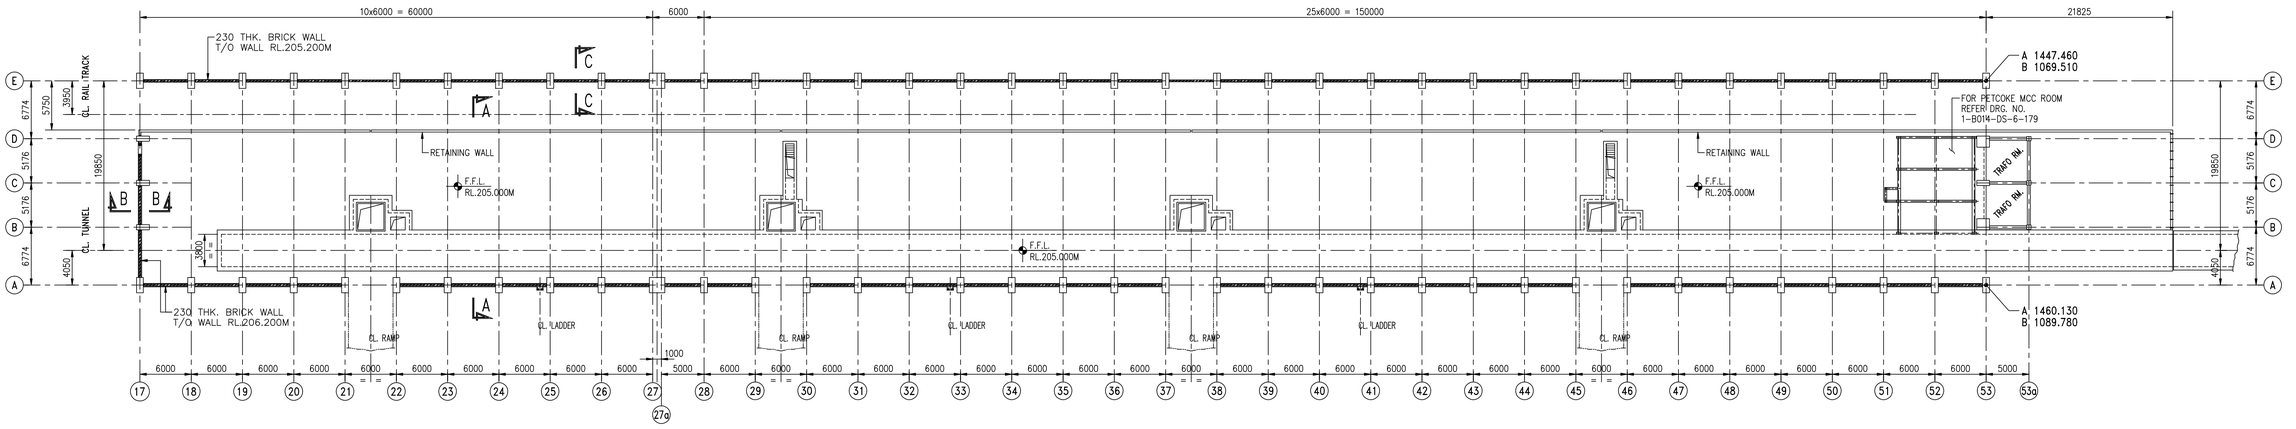

GROUND FLOOR PLAN
(SCALE 1:300)

CLEAR COVER TO MAIN REINFORCEMENT SHALL BE 25mm UNLESS NOTED OTHERWISE.

NOTES :–

1. ALL DIMENSIONS ARE IN MILLIMETRES AND LEVELS ARE IN METRES UNLESS NOTED OTHERWISE.
2. PLANT EL.(±)0.000M CORRESPONDS TO RL.203.500M.
3. F.G.L. (FINISHED GROUND LEV.) CORRESPONDS TO RL.203.000M.
4. CONCRETE TO BE OF GRADE M20 UNLESS NOTED OTHERWISE.
5. ALL REBARS ARE TO BE OF TMT RODS OF GRADE–Fe500 CONFORMING TO IS:1786–1985.
6. THIS DRAWING SHALL BE READ IN CONJUNCTION WITH DRG. NO. 1–B014–DS–6–001, 002, 003, 004 & 005.

REV	REVISION DETAILS	NO.OF REV. MARKS	DRAWN	CHECKED	REVIEWED: MECH.	PRO. & UTIL.	ELEC.	INST.	CIVL	STRL.	APPROVED	DATE
6												
5												
4												
3												
2												
1												

SL.NO.	DRG. PRPD. BY	DESCRIPTION	DRAWING NO.	SHT	REV

REFERENCE DRAWINGS

DATE	16.04.09	17.04.09	20.04.09								21.04.09
SIGN.											
NAME	S.Paul	S.Samanta	R.Das								R.Das
	DESIGNED	DRAWN	CHECKED	REVIEWED: MECH.	PRO. & UTIL.	ELEC.	INST.	CIVL	STRL.		APPROVED

1. DO NOT SCALE, IF ANY DOUBT PLEASE ASK.
2. REVISION MARKS ARE INSCRIBED IN △

THIS DRAWING IS MBE'S PROPERTY AND MUST NOT BE USED EXCEPT IN CONNECTION WITH MBE'S WORK. REPRODUCTION, USE OR DISCLOSURE OF THE CONTENTS OF THIS DRAWING TO THIRD PARTY/IES WITHOUT EXPRESS / WRITTEN PERMISSION OF MBE IS STRICTLY PROHIBITED.

CLIENT	VEDANTA ALUMINIUM LIMITED, JHARSUGUDA, INDIA
PROJECT	THREE UNITS OF GREEN ANODE PLANT
TITLE	PETROLEUM COKE UNLOADING & STORAGE SHED GROUND FLOOR - G.A. & DETAILS
	McNally Bharat ENGINEERING COMPANY LIMITED, 4, MANGOE LANE. KOLKATA, INDIA. (PROJECTS DIVISION)
SCALE	1:300,25,10
MBE DRAWING NUMBER	1 – B014 – DS – 6 – 015
MBE ~~PROPOSAL~~/SO NO.	08304
SHT NO.	1
REV.	0

STF–G–002 (REV–1) 07–10.01.2001

Jharsuguda expansion AL sheet