
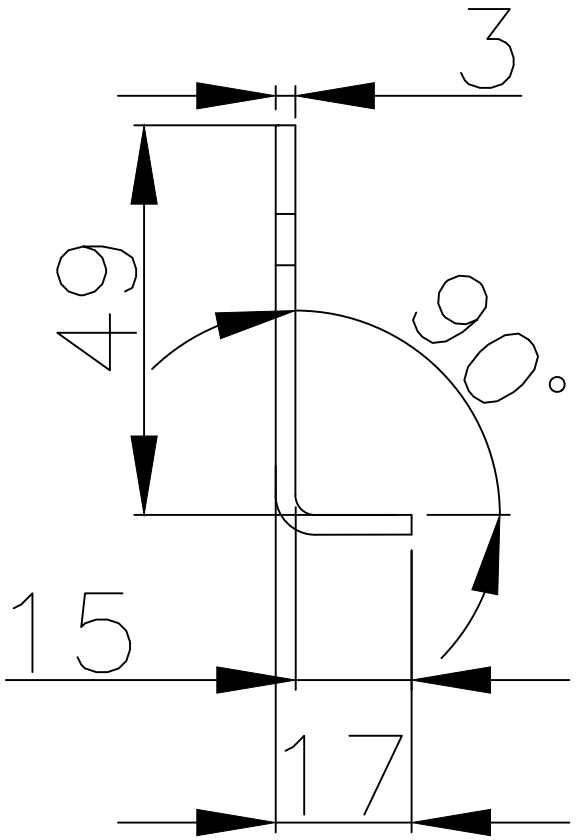


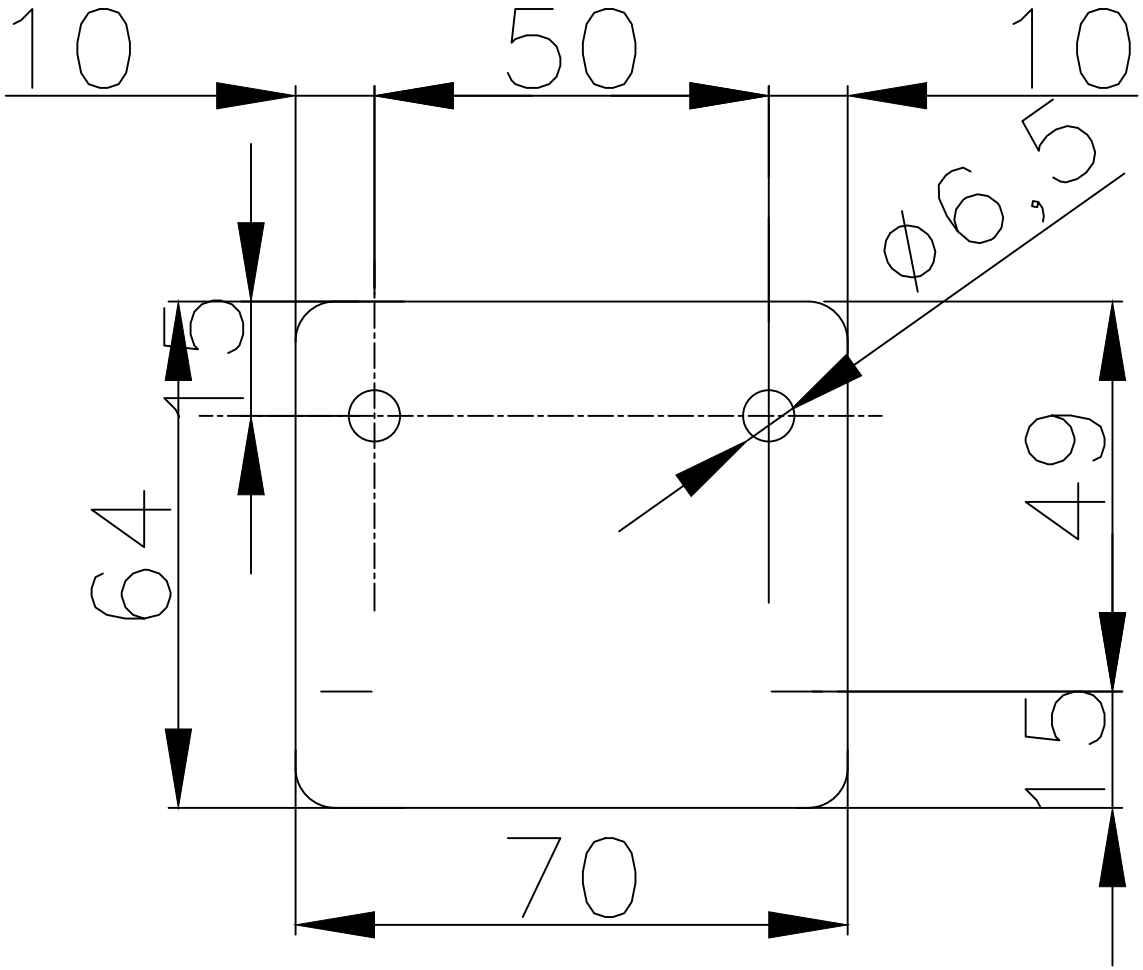

NOTE : MTL = SS 304

This drawing & design is the property of NIHVA TECHNOLOGIES. Not to be sold or copied to any other concern.

TITLE : - L-PLATE FOR SEGMENT LOCKING			NIHVA TECHNOLOGIES PVT. LTD. PUNE Tel : 020 66304033 Email:- info@nihva.com Website:- www.nihva.com
	SIGN	DATE	
DRAWN	G.J	19.08.19	
CHECK	A.K	19.08.19	
REV.			
APPROVAL			DWG. NO. : NIHVA\19-20\VDR\0069
If any queries contact : projects@nihva.com			SCALE: NTS / MATERIAL - SS 304, 3MM
ALL DIMENSION ARE IN mm			QUANTITY :- 24 Nos. / Part Number - LPSL