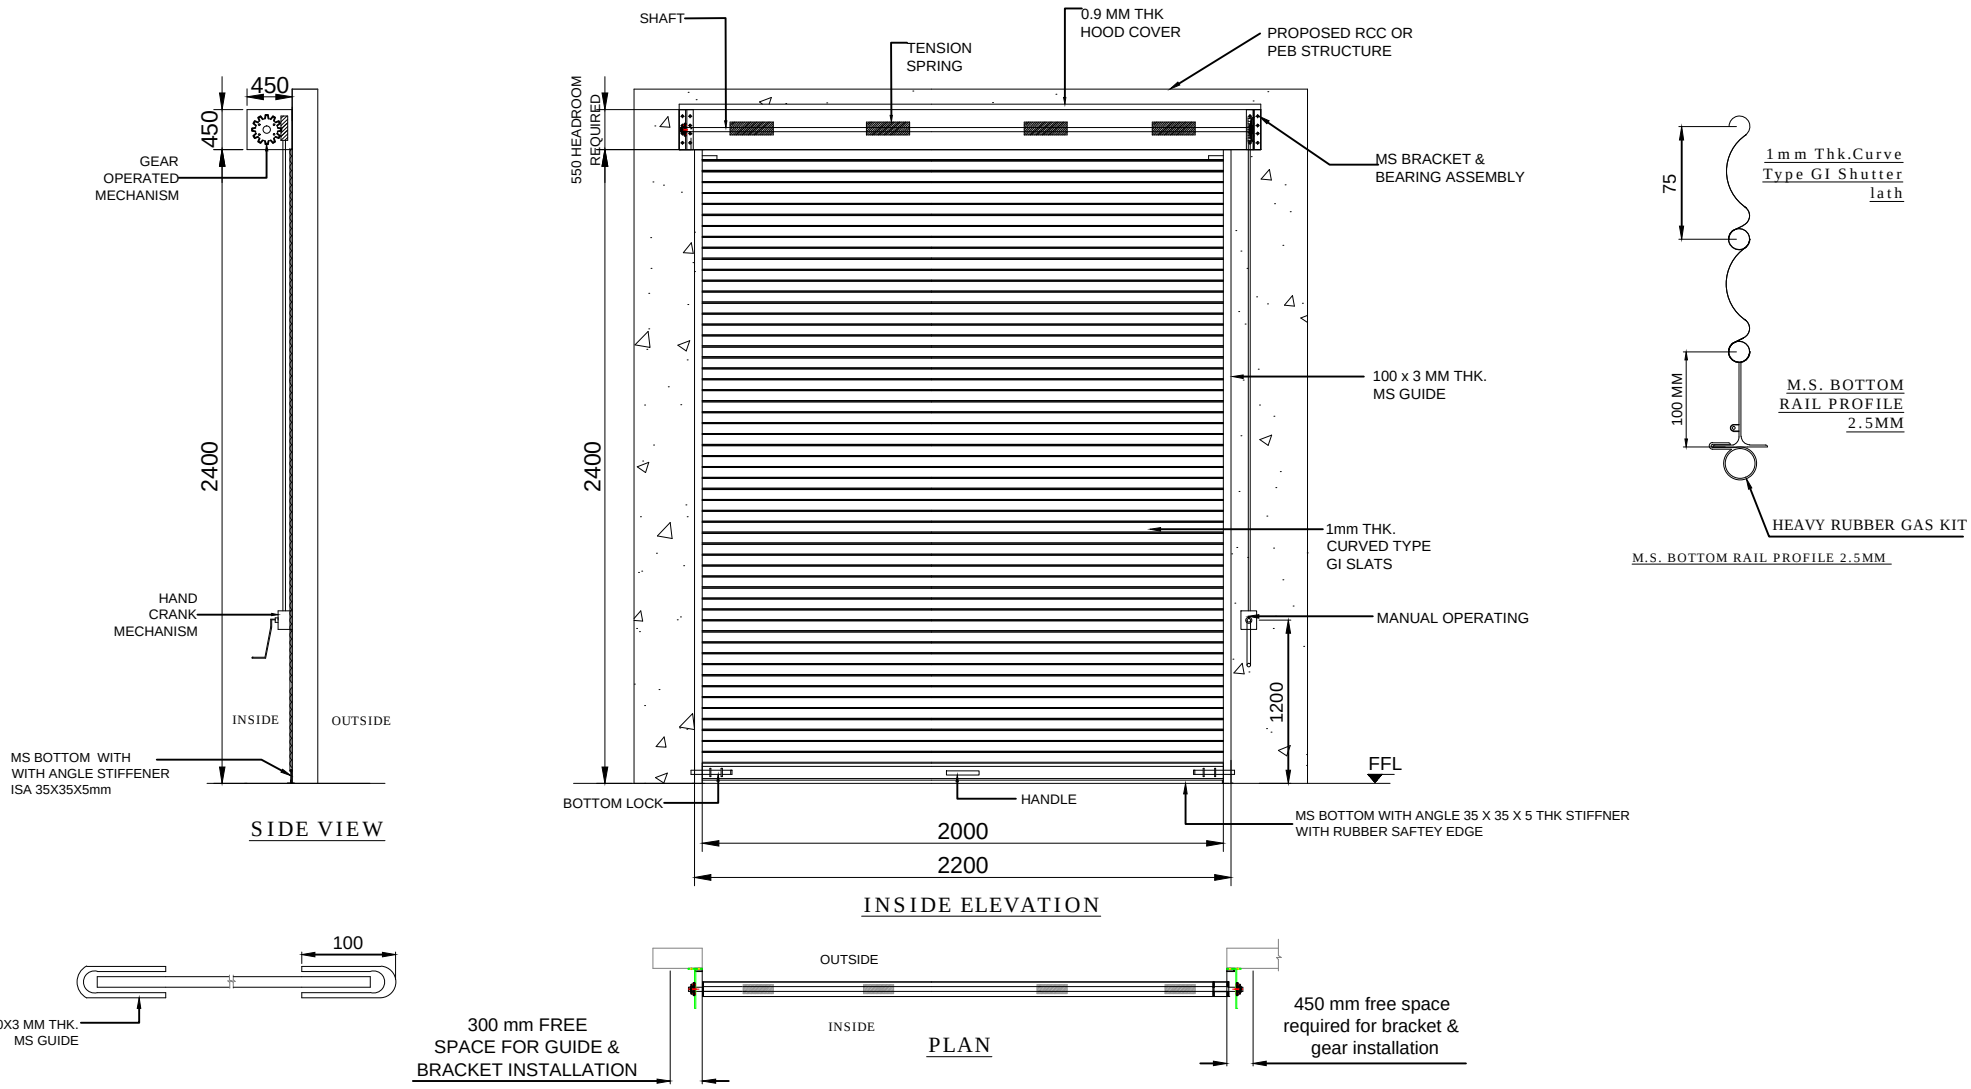


TOLERANCE - ±10mm

S.N.	LOCATION	SIZE	QUANTITY
1	-	2000(W)X2400(H)	01

NOTE-
1. ALL CIVIL WORK WILL BE CLIENT'S SCOPE.
2.STRUCTURE REQUIRED FOR SHUTTER IS IN CLIENT'S SCOPE.
3.FINAL FINISH OF SHUTTER WILL BE IN POWDER COATING OF APPROVED COLOR.
4.DESIGN OF SHUTTER IS AS PER I.S. 6248:1979 STANDARDS.

This drawing & design is the property of NIHVA TECHNOLOGIES. Not to be sold or copied to any other concern.

TITLE	GEAR OPERATED ROLLING SHUTTER 2mX2.4m With Right side gearbox			NIHVA TECHNOLOGIES PVT. LTD. PUNE Tel : 020 66304033 Email:- info@nihva.com
	NAME	SIGN	DATE	Website:- www.nihva.com
DRAWN	SURAJ		14.12.2018	CLIENT -REWARD CONSTRUCTION
CHECK	P.A		14.12.2018	PROJECT -
APPRD.	R.D		14.12.2018	SITE LOCATION - CHAKAN
If any queries contact : design@nihva.com				DWG. NO. : NIHVA/18-19/0205 / REV- 0
ALL DIMENSION ARE IN mm				SCALE: NTS / WT: / SHEET: 01 OF 01