NIHVA

NIHVA TECHNOLOGIES PVT. LTD.


CUSTOMER NAME :- PAVILION MALL PUNE

SUPPLIER :- NIHVA TECHNOLOGIES PVT LTD

PROJECT NAME :- RETRACTABLE SYSTEM

RETRACTABLE ROOF - THE PAVILION, PUNE


NIHVA
NIHVA TECHNOLOGIES PVT. LTD.

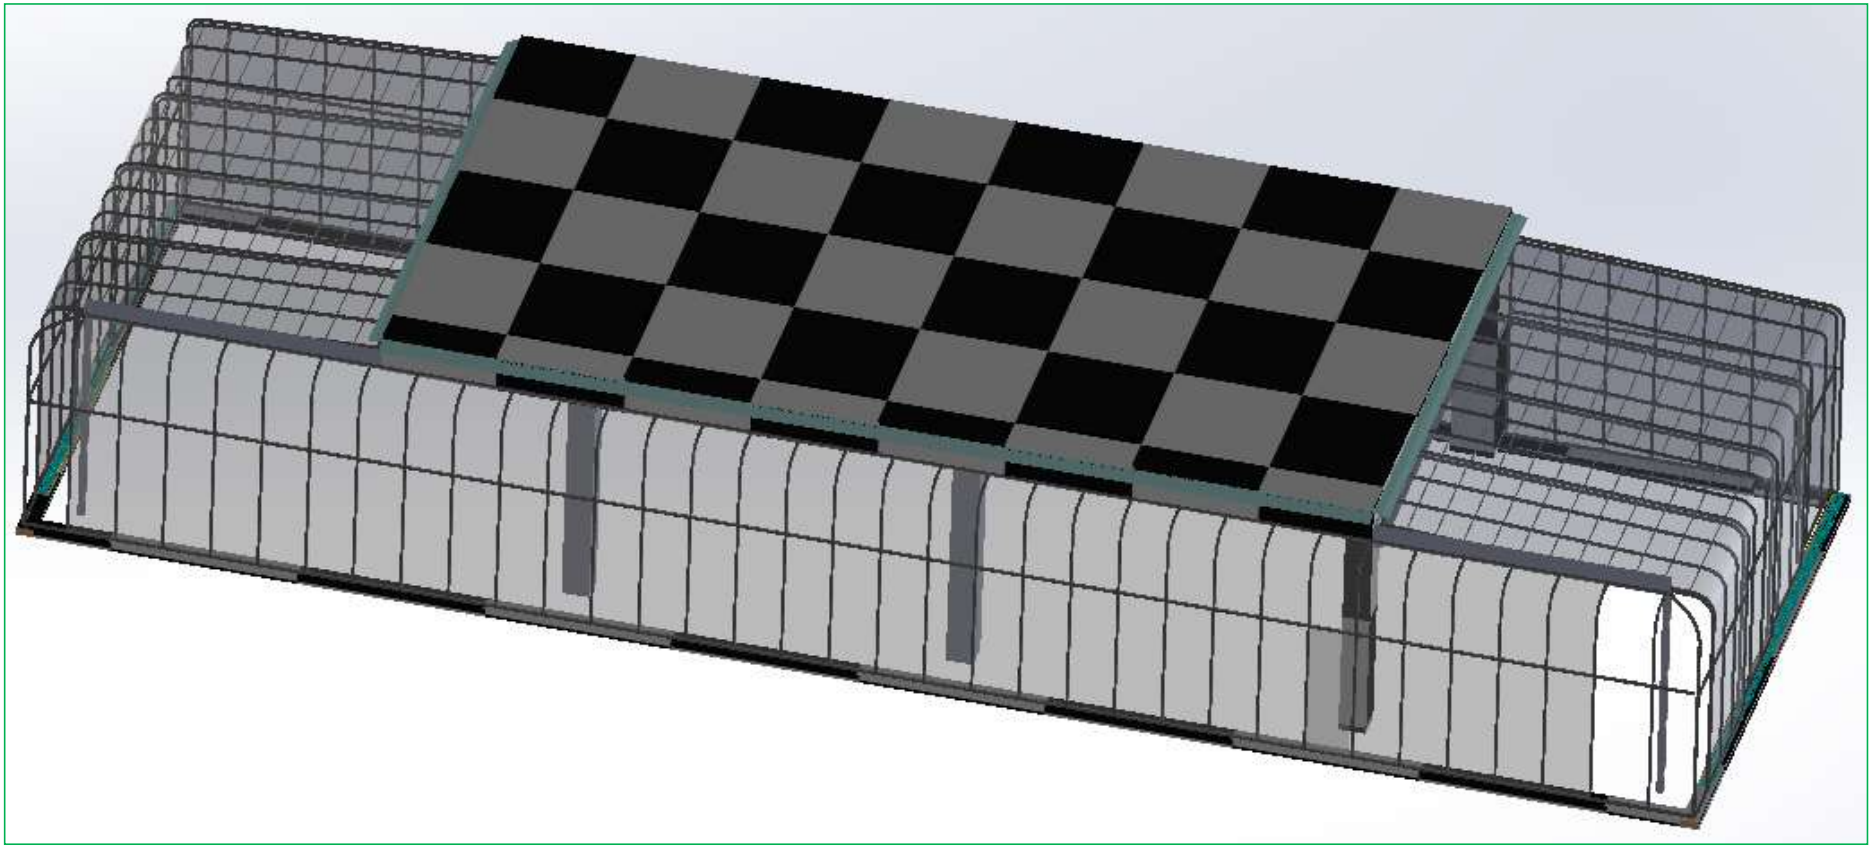

CLOSE CONDITION

RETRACTABLE ROOF - THE PAVILION, PUNE


NIHVA
NIHVA TECHNOLOGIES PVT. LTD.

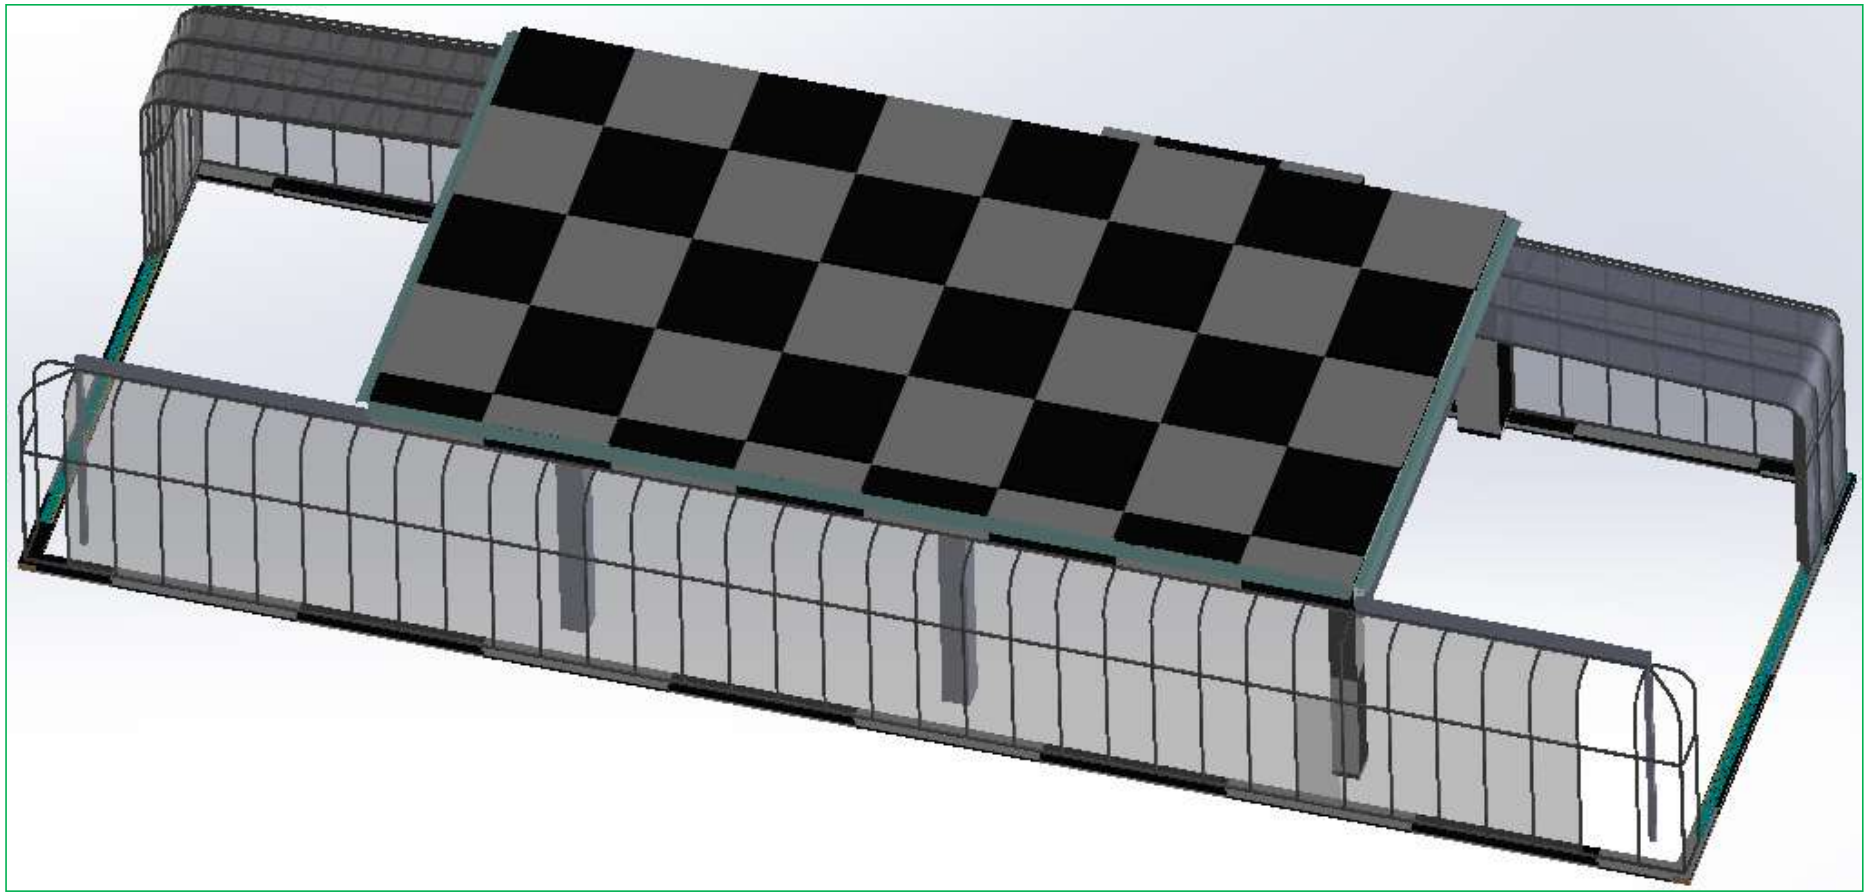

OPEN CONDITION

RETRACTABLE ROOF - THE PAVILION, PUNE


NIHVA
NIHVA TECHNOLOGIES PVT. LTD.

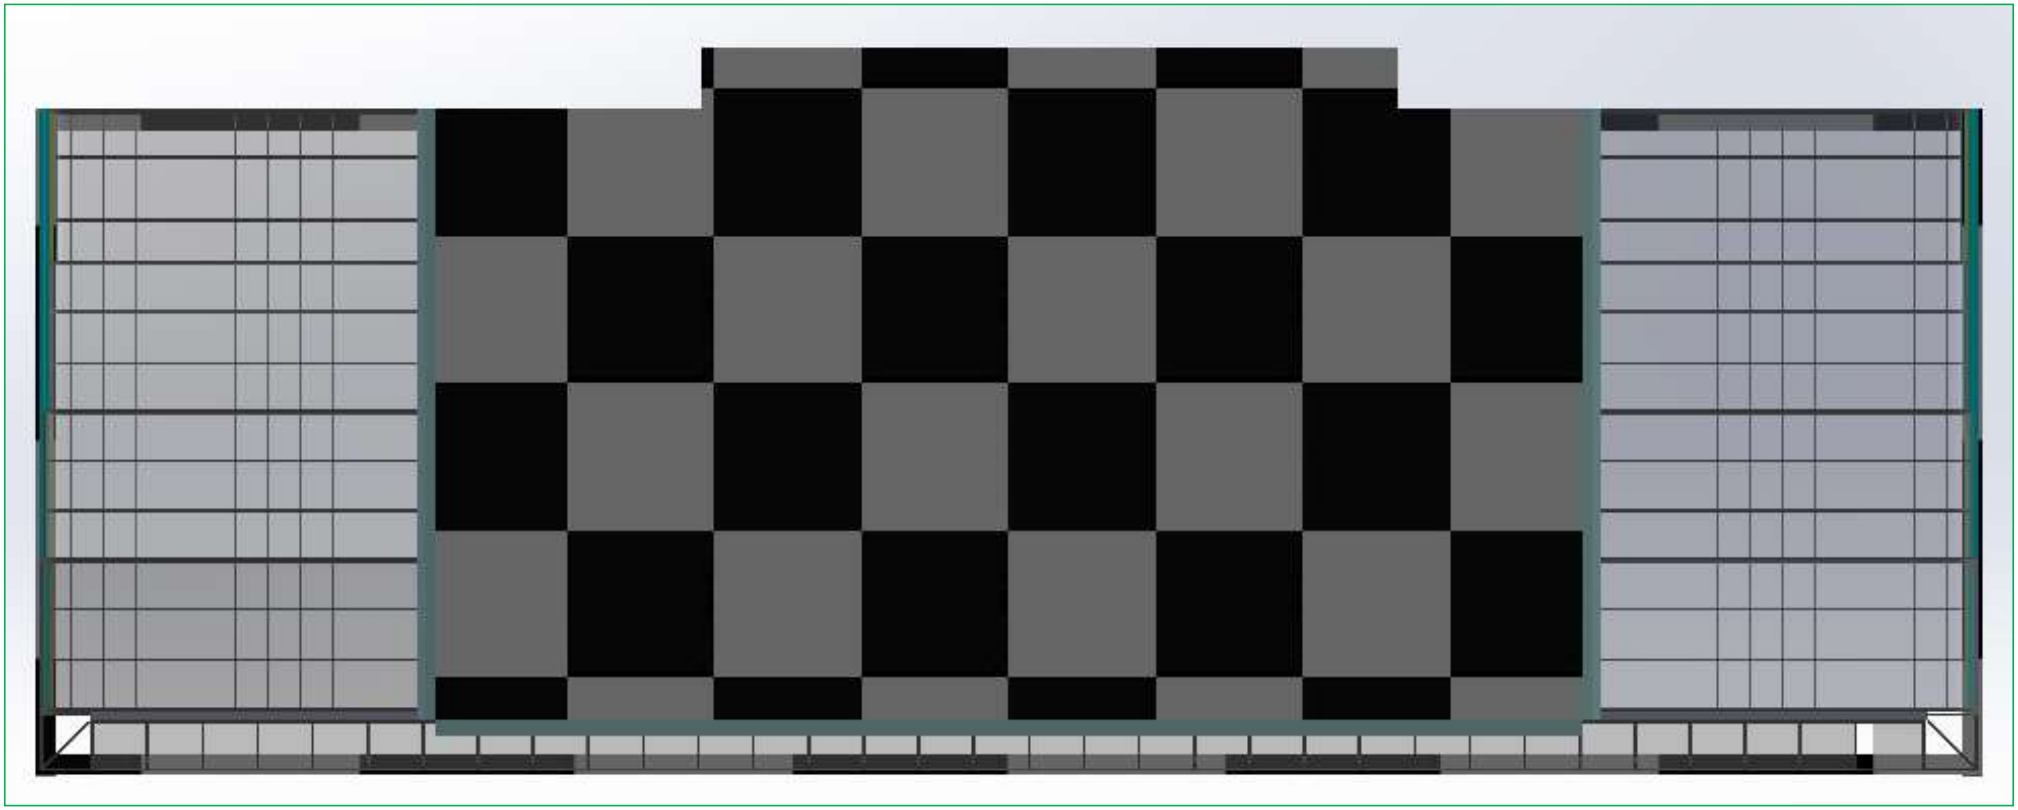

TOP VIEW

RETRACTABLE ROOF - THE PAVILION, PUNE


NIHVA
NIHVA TECHNOLOGIES PVT. LTD.

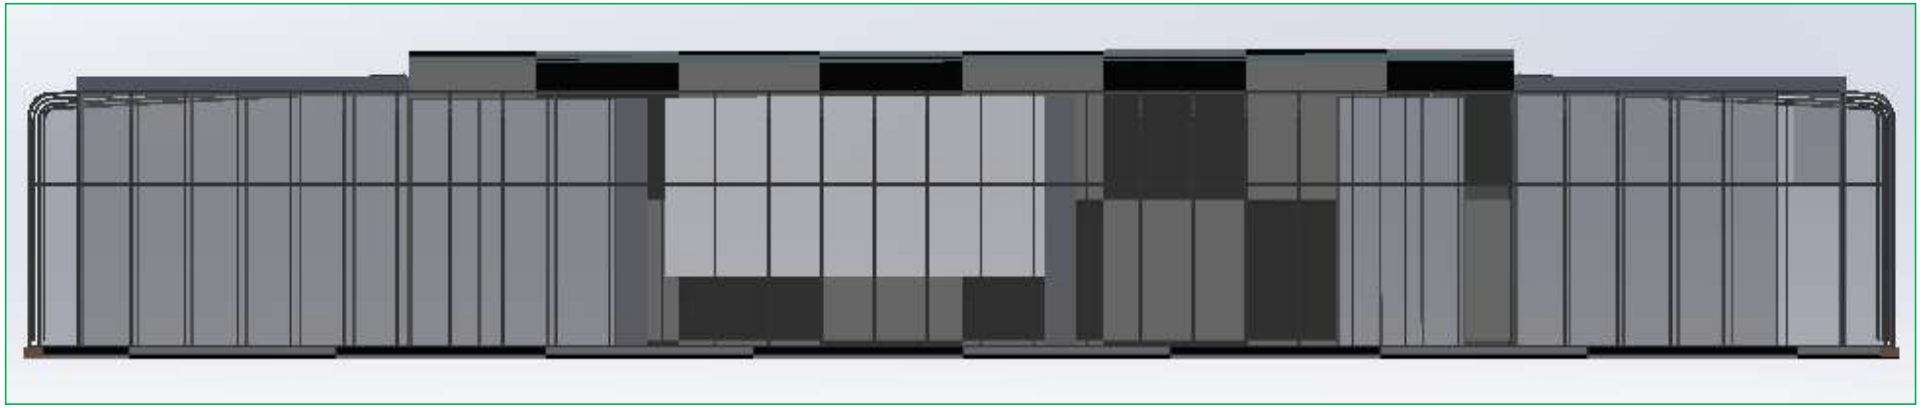

FRONT VIEW

RETRACTABLE ROOF - THE PAVILION, PUNE

NIHVA
NIHVA TECHNOLOGIES PVT. LTD.

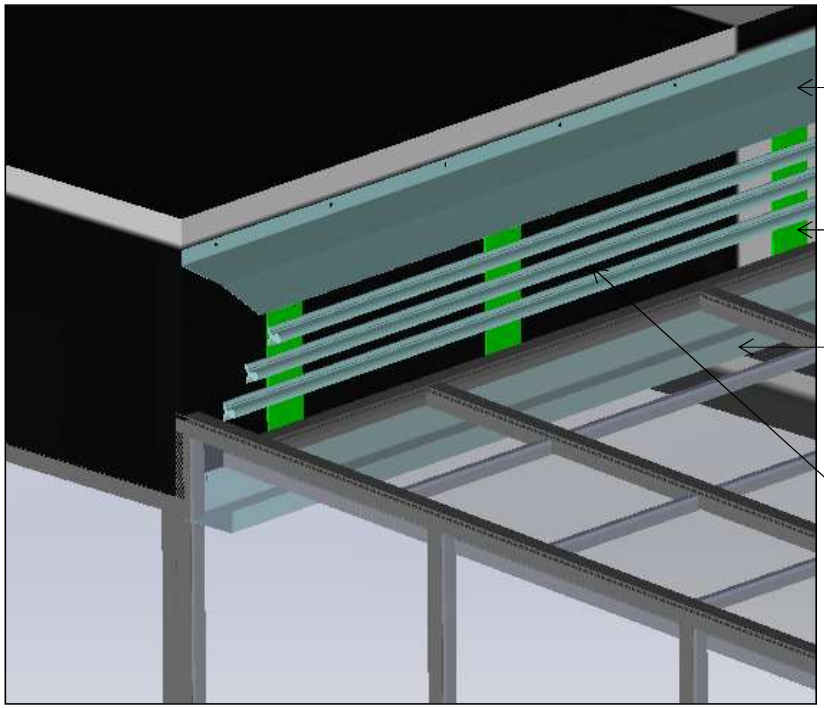


RAIN GUARD

GUIDE ANCHORING PLATE

BOTTOM WATER GUTTER

TOP GUIDE FOR SLIDING

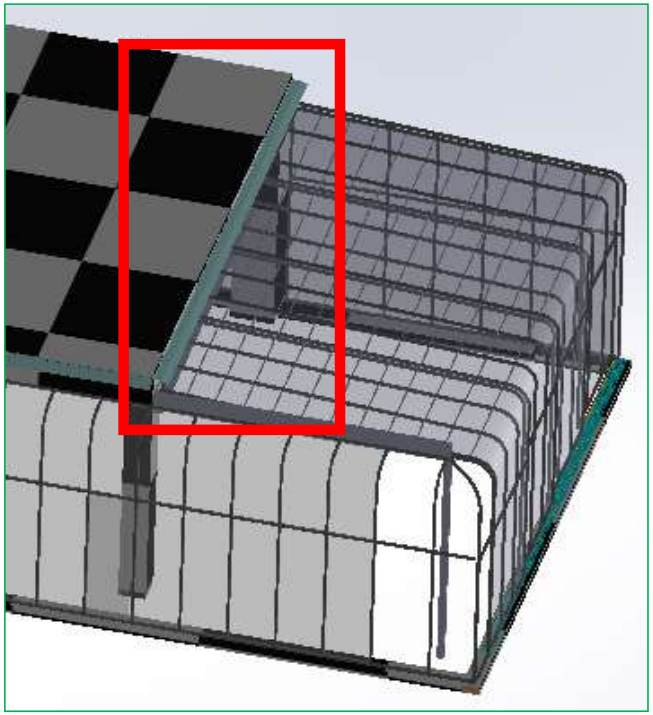


TOP TRACK MOUNTING (ANCHORING)

NOTE :

1. Ø 10 X 150 MM ANCHORING FOR 1 M PITCH DISTANCE ALONG 4 GUIDES, 1 TOP RAIN GUARD & 1 BOTTOM GUTTER.

RETRACTABLE ROOF - THE PAVILION, PUNE

NIHVA
NIHVA TECHNOLOGIES PVT. LTD.

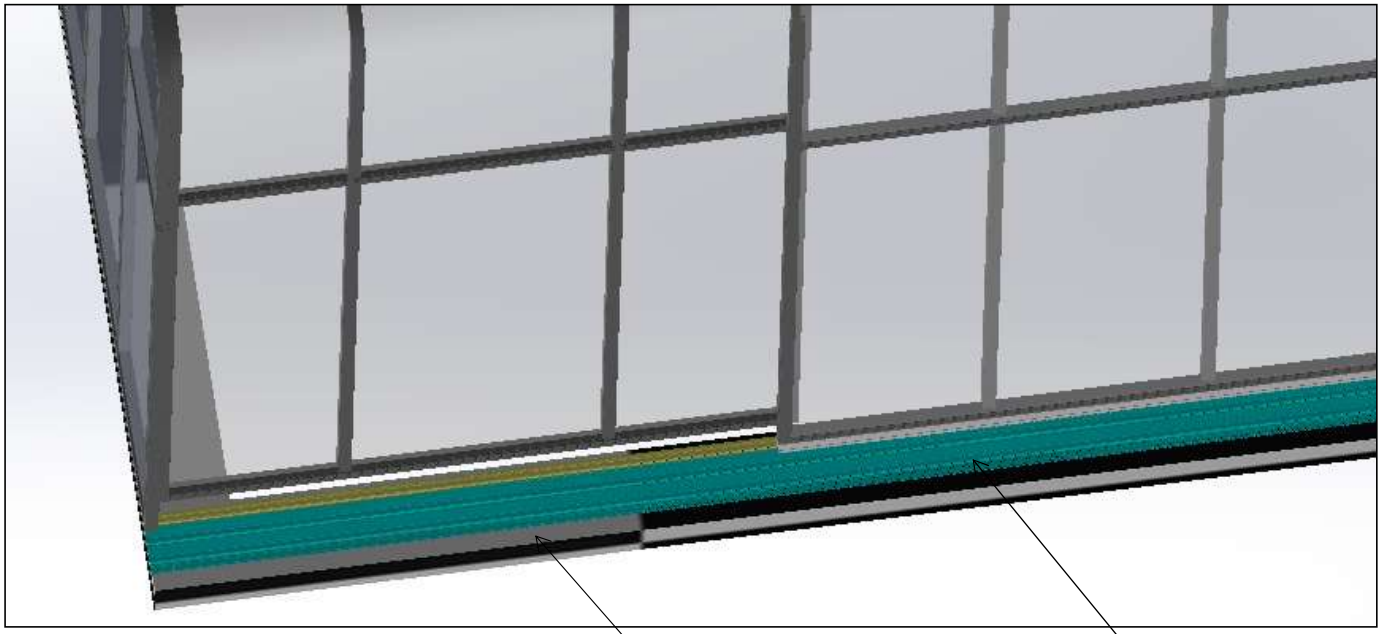


NOTE :

1. EACH TRACK HAVING A Ø 10 X 150 MM ANCHORING FOR 1 M PITCH DISTANCE FOR EACH GUIDE.
2. BOTTOM CONCRETE SURFACE IS IN CLIENT SCOPE

RETRACTABLE ROOF - THE PAVILION, PUNE

NIHVA
NIHVA TECHNOLOGIES PVT. LTD.

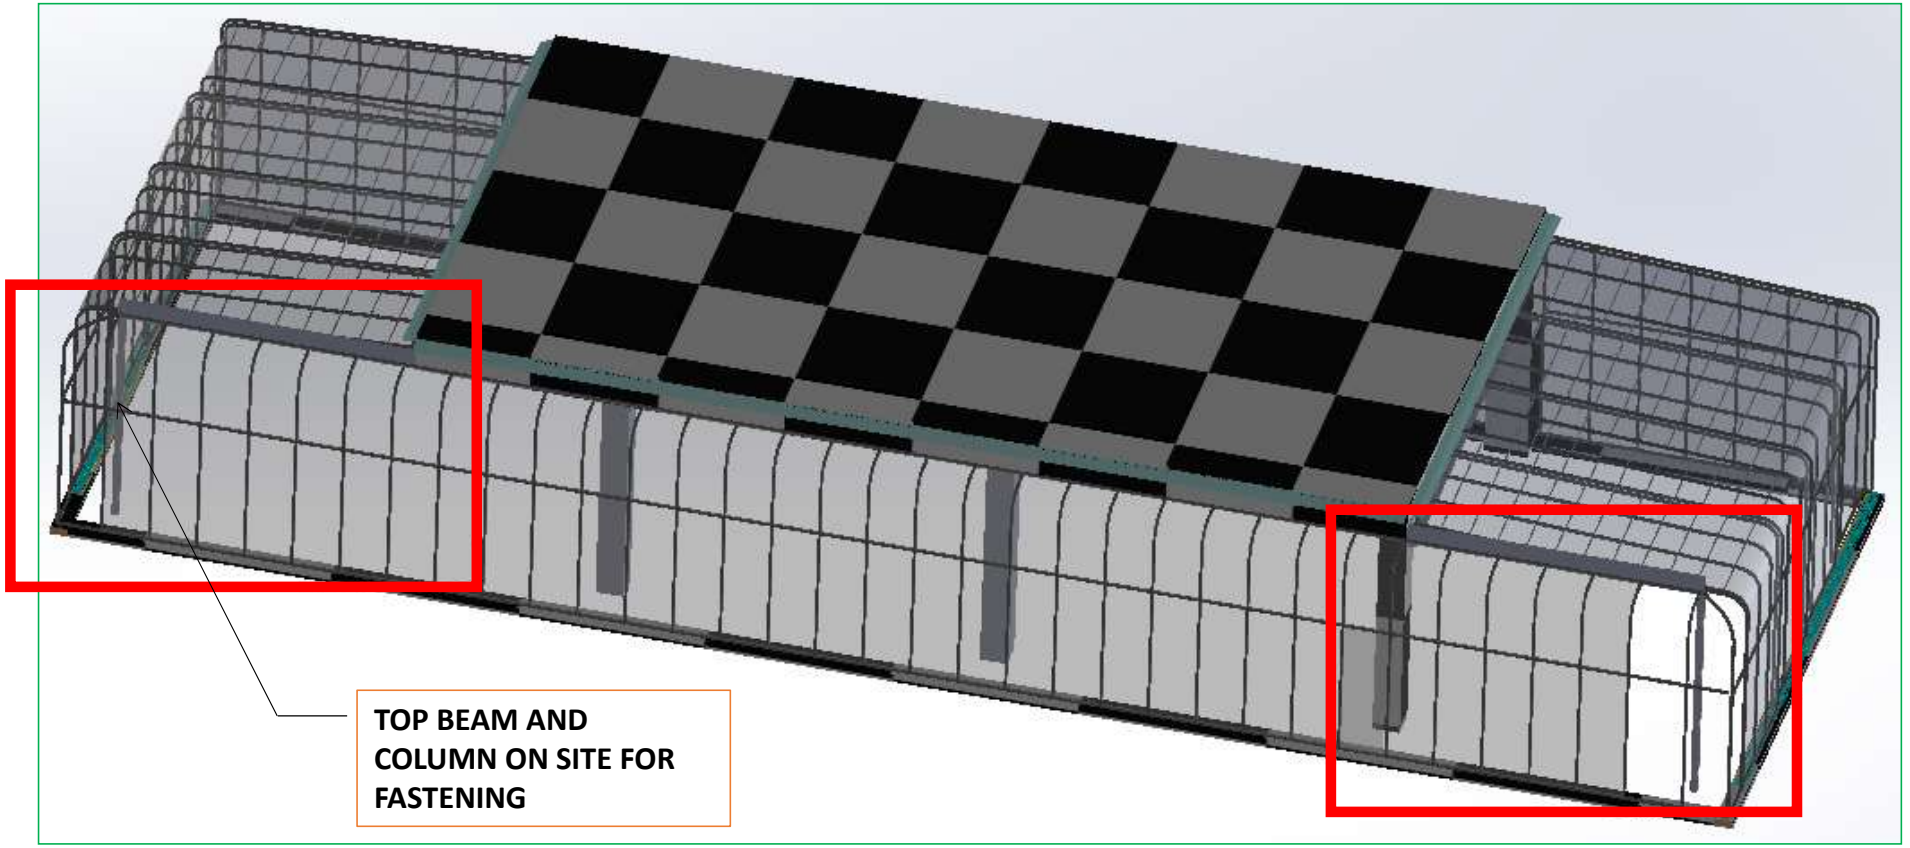

NOTE :

1. STRUCTURAL COLUMN SHOWN IS IN NIHVA SCOPE.

RETRACTABLE ROOF - THE PAVILION, PUNE

NIHVA TECHNOLOGIES PVT. LTD.

OBSERVATION:-

1. The top beam height from the ground is not at one level. Variations are observed from 4877 mm to 5026 mm along the periphery. It needs to be on one level for proper alignment of whole system.
2. On the LH side, there is slope on the floor which needs to be addressed.
3. Bottom concrete block to be constructed for anchoring and fastening for the whole system. It is in client scope.

THANK YOU!