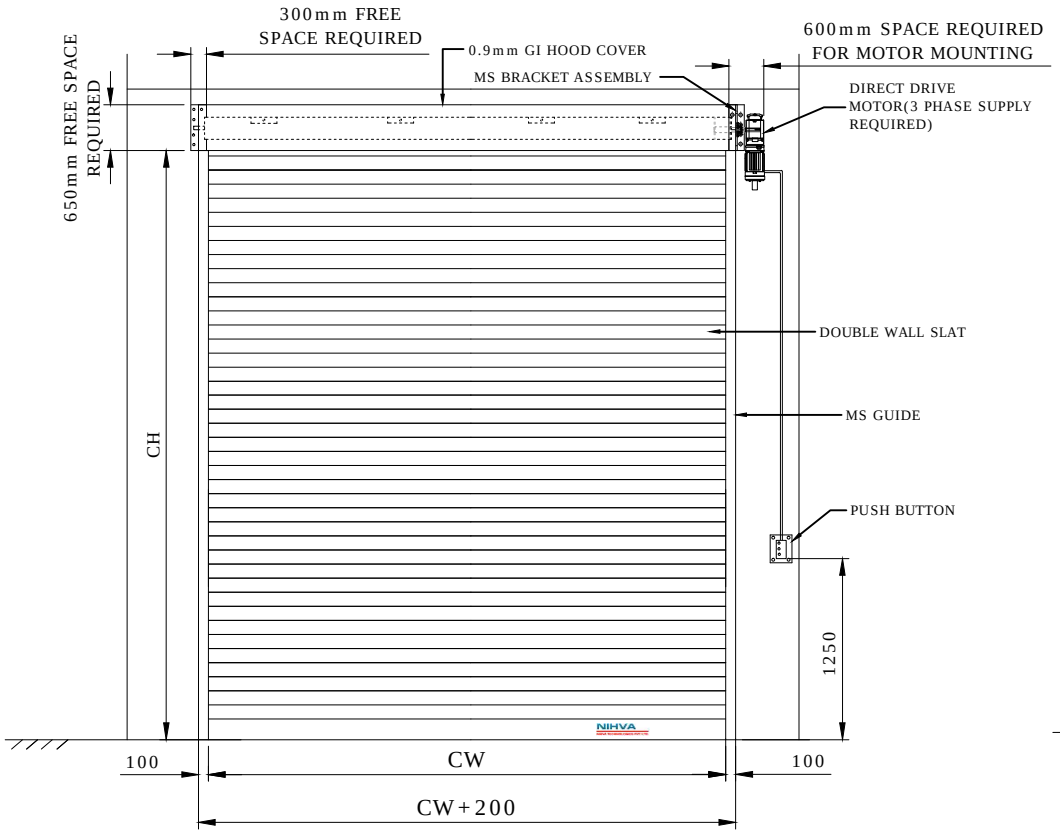

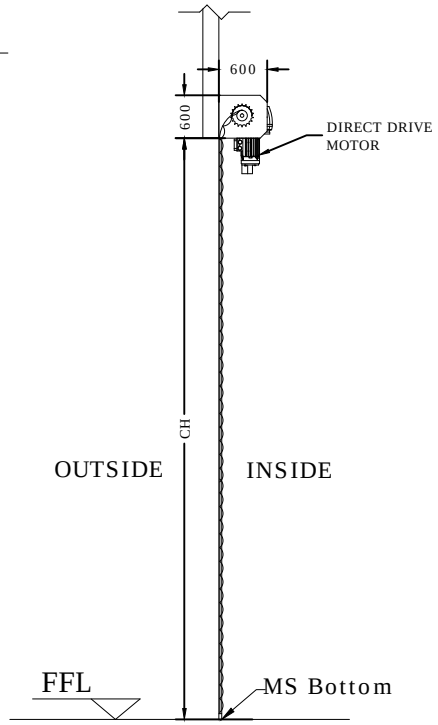

Section A-A

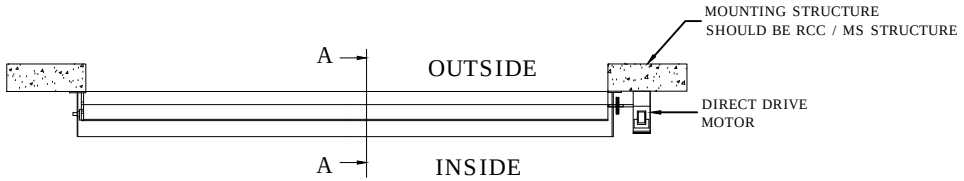

Main Slats
Double Wall Rolling Shutter

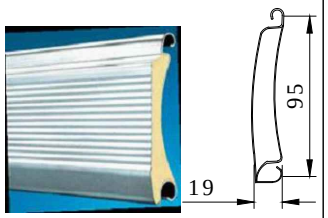

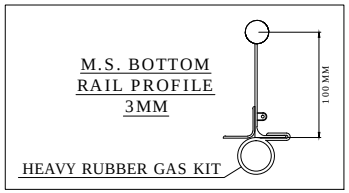

CLEAR WIDTH (CW)	CLEAR HEIGHT (CH)	QUANTITY
2000 mm	3000 mm	2 NOS
2500 mm	3000 mm	1 NOS

COLOR - PU PAINT AS PER APPROVED RAL SHADE.

DIMENSION :

CLEAR WIDTH	CLEAR HEIGHT	QUANTITY
2000 mm	3000 mm	2 NOS
2500 mm	3000 mm	1 NOS

MATERIAL :

THICKNESS :

NOTE:-

1.STRUCTURE FOR SHUTTER FOR SHUTTER WILL BE IN CLIENT'S SCOPE.

2. 3 PHASE SUPPLY SHOULD BE PROVIDED.

NIHVA TECHNOLOGIES PVT. LTD.

NIHVA TECHNOLOGIES PVT. LTD. PUNE
Email:- info@nihva.com
Website:- www.nihva.com

TITLE:

DOUBLE WALL ROLLING SHUTTER

CLIENT'S APPROVAL :

CLIENT -

PROJECT -

SITE LOCATION -

DWG. NO. : NIHVA/17-18/VDR/0125

SCALE: NTS	WT:	SHEET:1 OF 1
DRAWN BY: OMKAR	DATE: 27-09-2017	
CHECKED BY: SHEKHAR	DATE: 27-09-2017	
APPROVED BY : SHEKHAR	DATE: 27-09-2017	

If any queries contact : projects@nihva.com

NOTE: ALL DIMENSIONS ARE IN mm

THIS DRAWING & DESIGN IS THE PROPERTY OF NIHVA TECHNOLOGIES. NOT TO BE SOLD OR COPIED TO ANY OTHER CONCERN.