IN CASE OF DOUBT ASK.

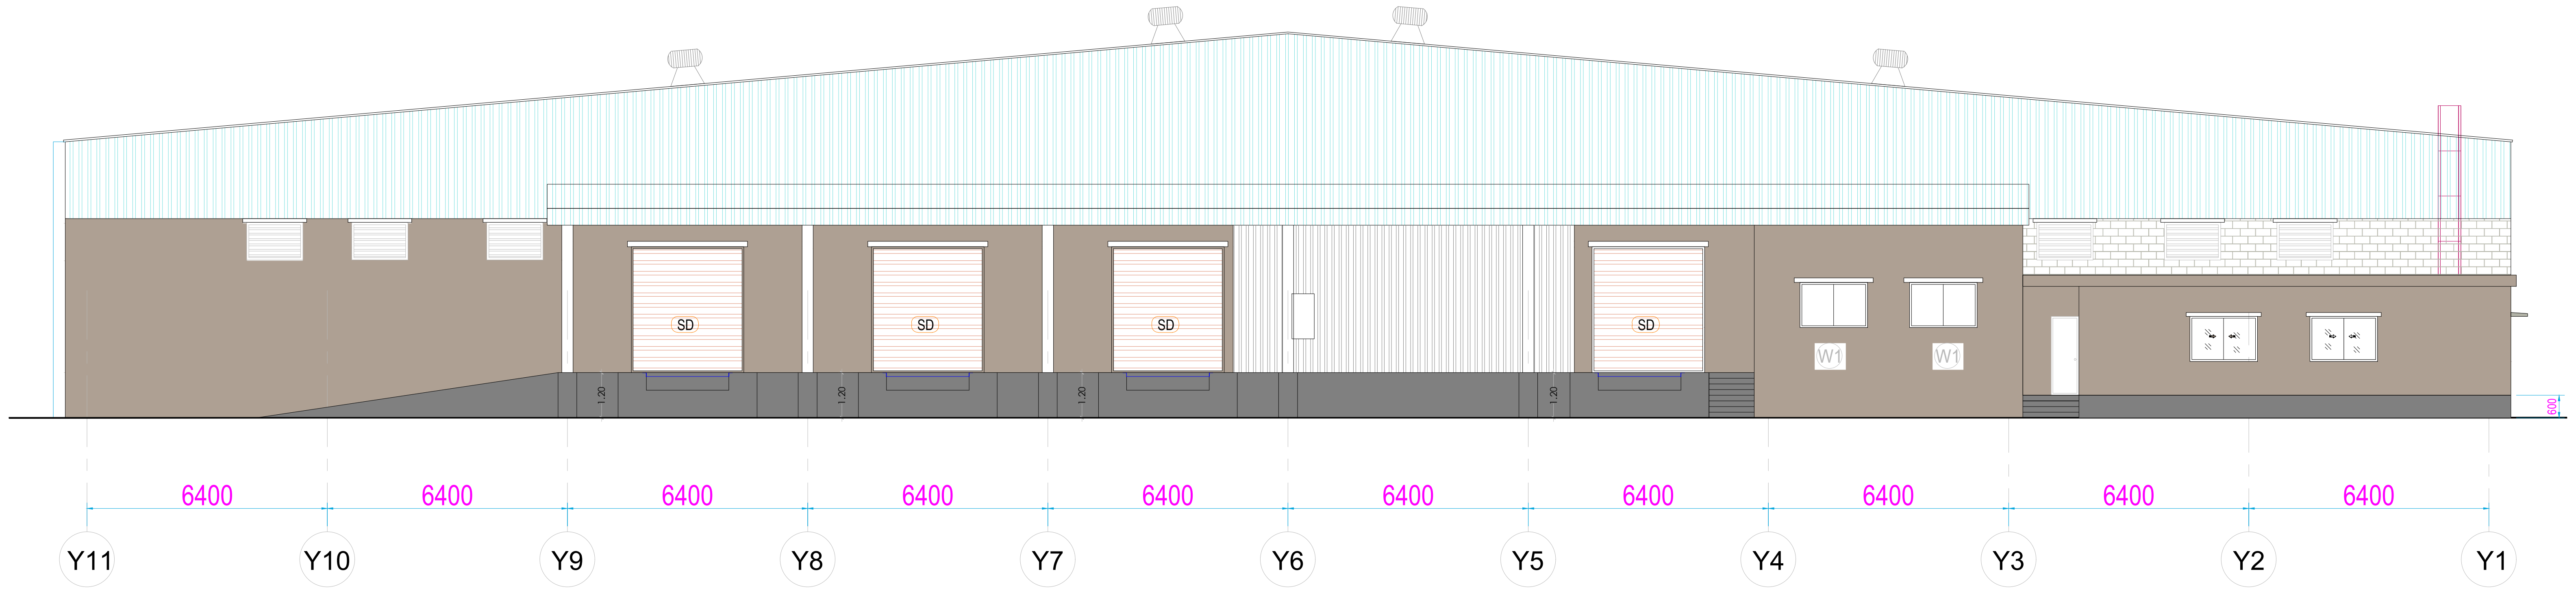

6 WEST SIDE ELEVATION

SCALE 1:100

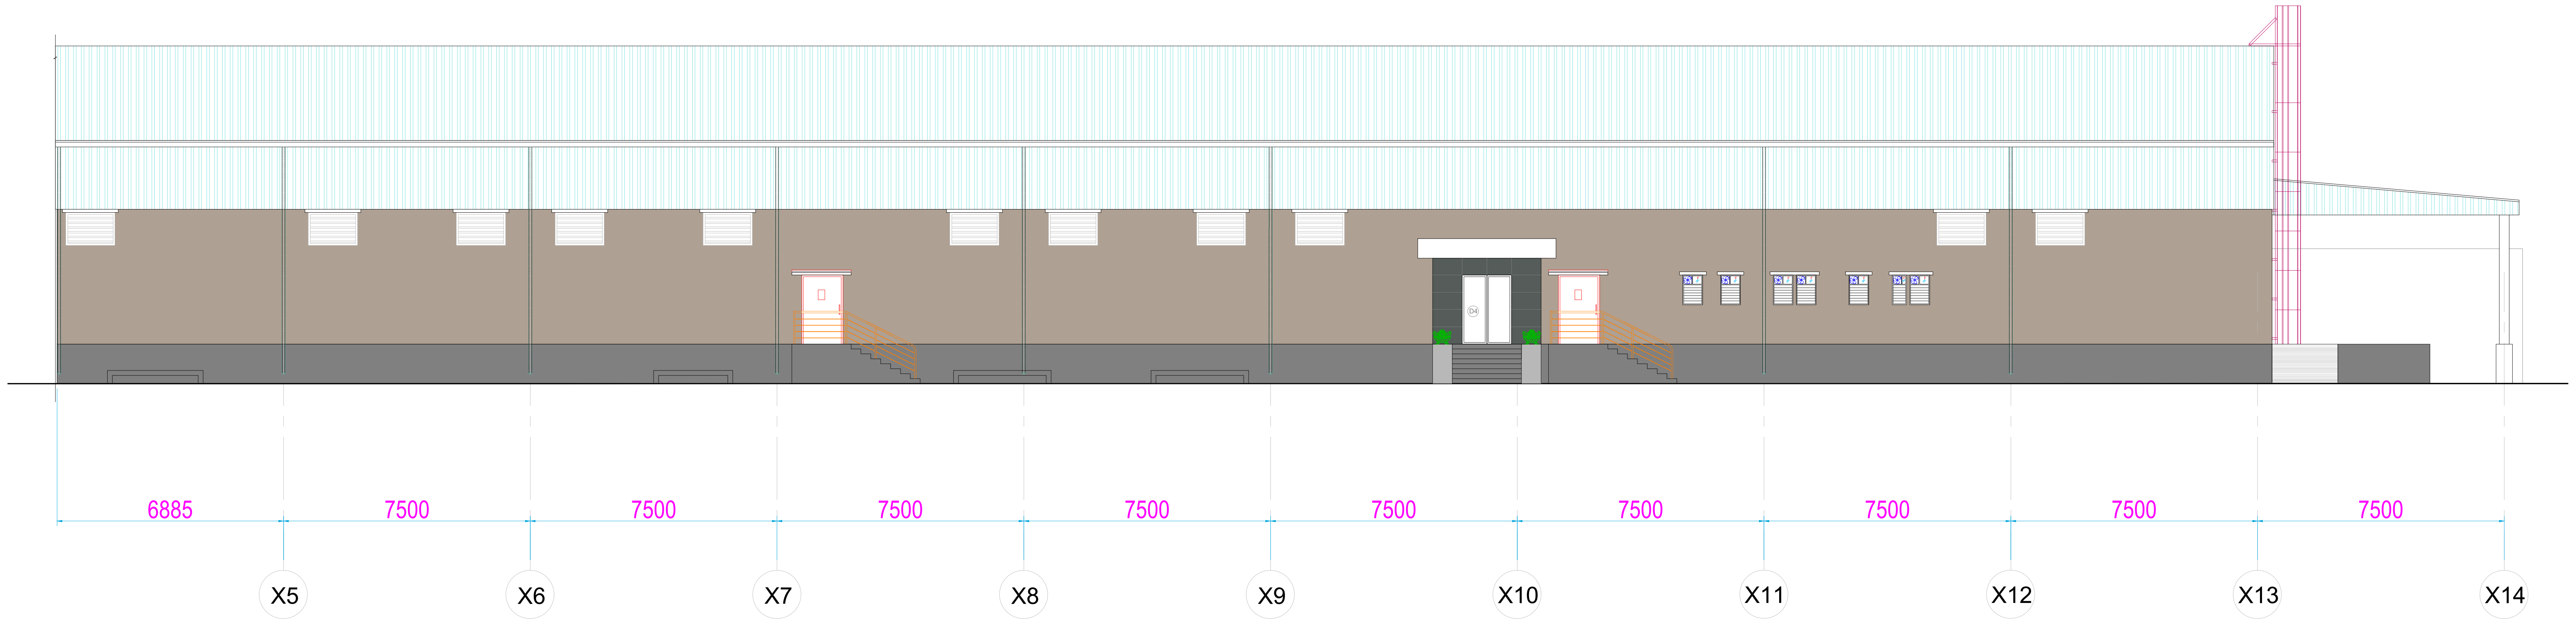

7 NORTH SIDE ELEVATION

SCALE 1:100

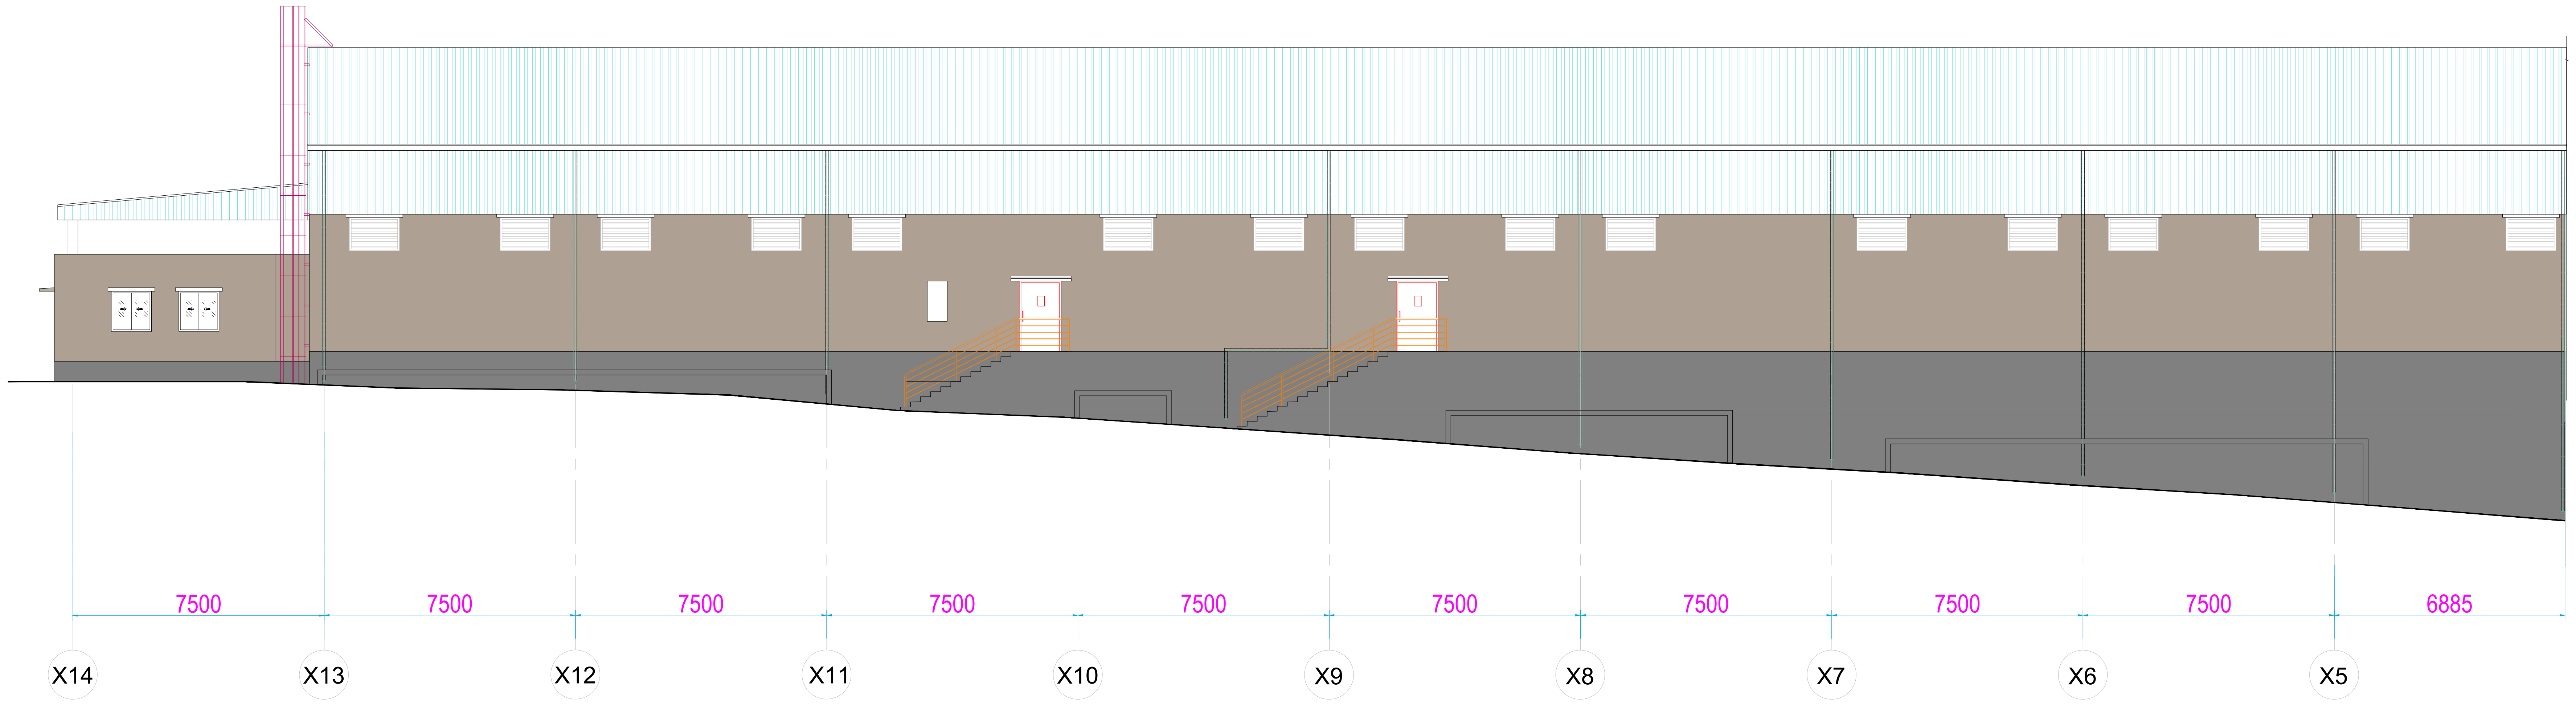

8 SOUTH SIDE ELEVATION

SCALE 1:100

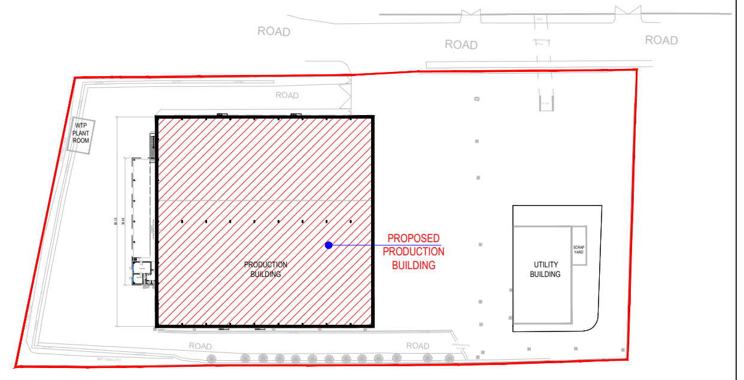

SITE PLAN

SCALE - NTS

ALL DIMENSIONS ARE IN MM.

--

NO.	REV. DATE	DESCRIPTION	NO.	REV. DATE	DESCRIPTION
R0	30.01.2020	FOR TENDER	R7		
R1			R8		
R2			R9		
R3			R10		
R4			R11		
R5			R12		
R6			R13		

DRG. NO. 201911A_1000_ARCH_GN_ELEV_107_TEN_00_R0

CHECKED BY	DRAWN BY	SCALE	BLDG. TYPE	JOB NO.	SHEET NO.
SK	SY	1:100	ELEVATIONS	201911A	1 OF 1

PROJECT
PROPOSED BEVERAGE AND WETS FACILITY IN SATARA MEGA FOOD PARK.

TITLE
PRODUCTION BUILDING - WESTSIDE, NORTH SIDE & SOUTH SIDE ELEVATION

CLIENT:

FOOD SERVICE INDIA PVT. LTD.
Plot No. 1+2, Gat No. 1288/1, 1288/2, 1490/1, 1490/2
Satara Mega Food Park, Satara.
Degaon, Tal. & Dist. Satara, Maharashtra,
Pin :- 415004

E.P.C.M.

FABS®
Facilities And Building Solutions

REGIONAL OFFICE :
FACILITIES AND BUILDING SOLUTIONS PVT. LTD.
12/26, RIVER VIEW APARTMENT, 1ST FLOOR,
OFF MUMBAI-PUNE ROAD,
WAKDEWADI, PUNE-411003
Tel. ☎ +91-8087002501

HEAD OFFICE :
FACILITIES AND BUILDING SOLUTIONS PVT LTD.
#856,5TH CROSS, 5TH MAIN,
INDIRANAGAR, 1ST STAGE,
BANGALORE-560 038
Tel. ☎ +91 80 41520118 / 120