

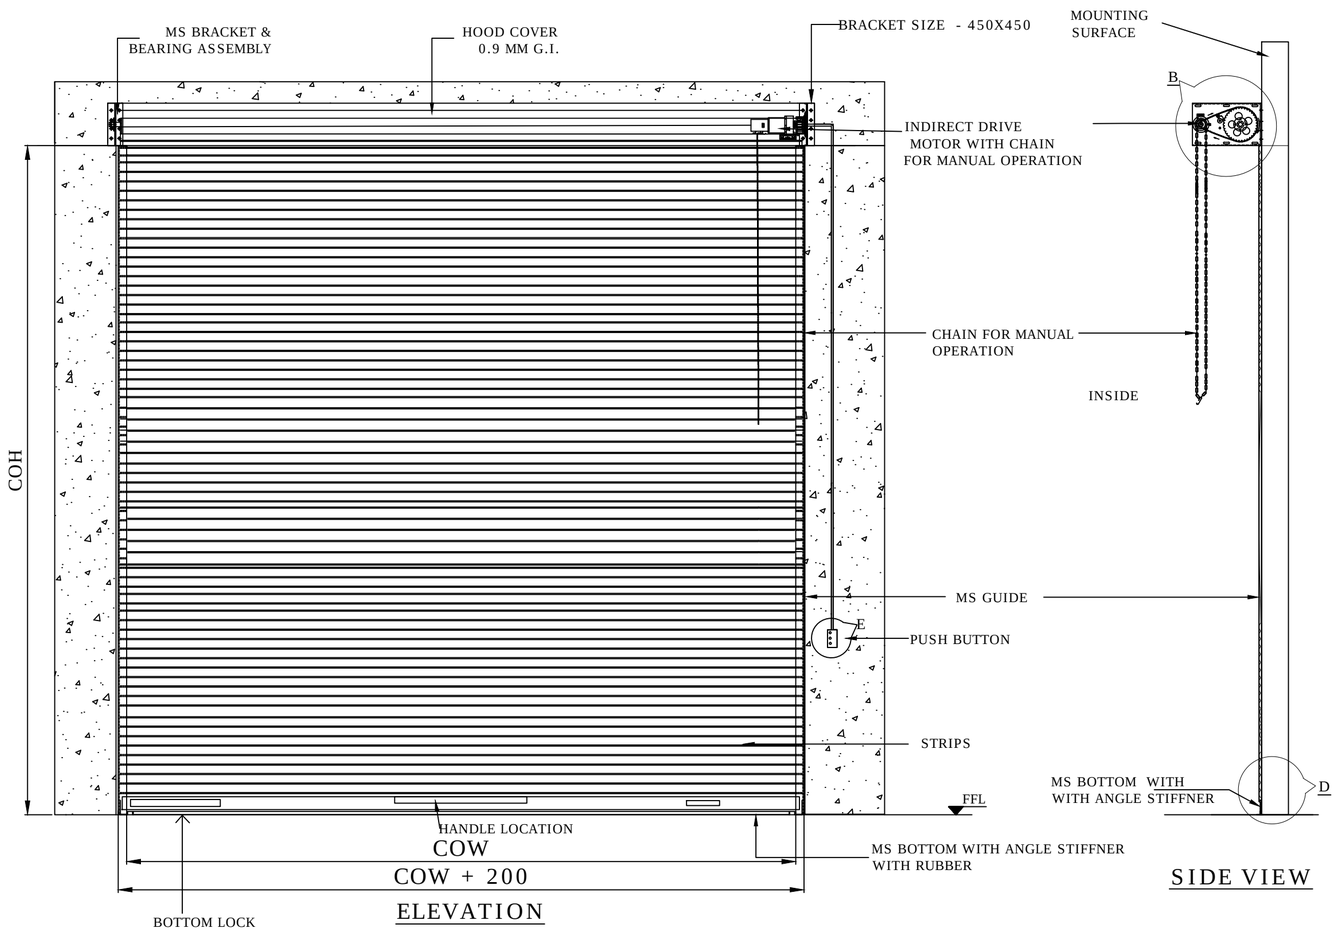


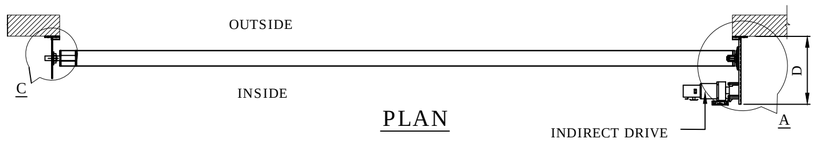

PLAN

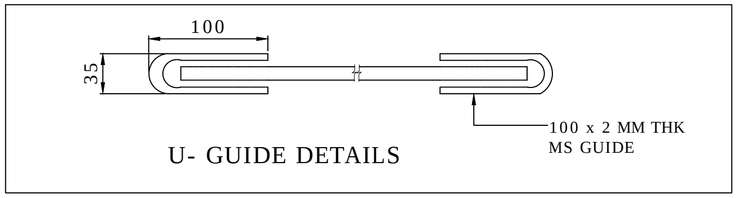


U- GUIDE DETAILS


RAL CODE	SHADE	COLOUR
RAL 9001	CREAM	
RAL 9002	GREY WHITE	
RAL 9010	PURE WHITE	
RAL 5002	ULTRAMARINE BLUE	
RAL 7035	LIGHT GREY	
RAL 7001	SILVER GREY	

NOTES-


1. REFER ABOVE RAL SHADE CHART & CONFIRM RAL SHADE FOR POWDER COATING .
2. CONFIRM MOUNTING OF ROLLING SHUTTER IS ON CONCRETE WALL OR STRUCTURE .
3. IF REQUIRED ALL CIVIL WORK , STRUCTURE & ITS FITTING IS IN CLIENT SCOPE .
4. SPACE OF 600 MM IS REQUIRED ABOVE CLEAR OPENING HEIGHT FOR INSTALLATION OF SHUTTER.
5. MOTOR - RIGHT SIDE STANDARD.

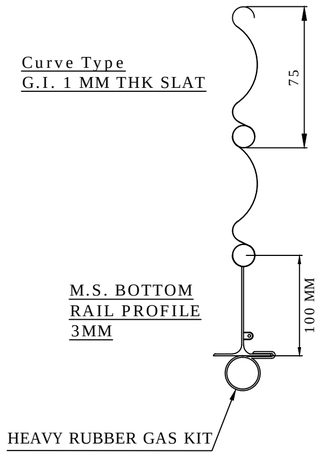

DETAILS : D

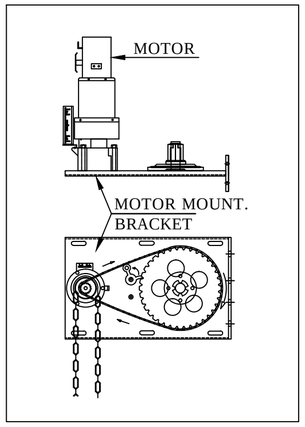

DETAILS : A & B

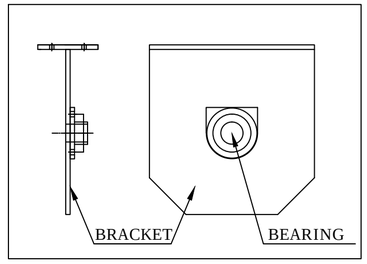

DETAILS : C

1	4050	4600	1 NO	
SR NO	CLEAR OPENING WIDTH (COW)	CLEAR OPENING HEIGHT (COH)	QUANTITY	RAL COLOR POWDER COATED

This drawing & design is the property of NIHVA TECHNOLOGIES. Not to be sold or copied to any other concern.

TITLE GI MOTORIZED ROLLING SHUTTER 4050X4600

	NAME	SIGN	DATE
DRAWN	S.M.S.		14.7.2021
CHECK	A.K.		14.7.2021
APPRD.			

NIHVA TECHNOLOGIES PVT. LTD.
NIHVA TECHNOLOGIES PVT. PUNE
Tel : 020 66304033
Email:- info@nihva.com
Website:- www.nihva.com

CLIENT - INGERSOLL RAND (INDIA) LIMITED

PROJECT -

SITE LOCATION - NARODA , AHMEDABAD

If any queries contact :design@nihva.com | DWG. NO. : NIHVA/21-22/040/MRS | REV- R00

ALL DIMENSION ARE IN mm | SCALE: NTS | WT: | SHEET: