Attachment profile related

54	6	Int. Beam support				19162433	0,08
53	6	Screw		MRT-GF 6x20		19200324	0,0066
52	74	Washer		RB 6,4 x 18 x 1,5		19203203	0,0015
51	6	Washer, rubber				19130893	0.0014
50	68	Screw		MRT-GF 6x16		19200452	0,006
49	62	Screw set				19143478	0,0
48							
47	1	Set of clamp strip attachment profiles				77809	78
46							

Bottom seal related

45							
44	222	Screw		RTS TX 5.5x19	Geomet	19204943	0,00
43							
42	2	Clamp strip		30x6 #2	L= 4558	19151078	1,3
41	4	Clamp strip		30x6 #2	L= 6000	19151078	1,7
40	1	Rubber seal	900 EPDM Grey	4x900	L= 16558 Finished Dimension	19203302	84,6

Bottom beam related


39							
38							
37							
36							
35							
34	1	Painted Clamp strip Alt. 2	Antracite grey (RAL7	30x6 #2	L= 4558	51124	1,3
33	2	Painted Clamp strip Alt. 2	Antracite grey (RAL7	30x6 #2	L= 6000	51124	1,7
32	1	Shims for bottom beam screw joint				19128506	
31	2	Nut	Class 8.8	M6M 20		19201687	0,053
30	4	Nut	Class 8.8	M6M 24		19203273	0,073
29	4	Washer	HB 200	21x36 t=3		19200202	0,011
28	8	Washer	HB 200	25x45 t=4		19203274	0,016
27	2	Screw	Class 8.8	M6S 20x70		19203191	0,22
26	4	Screw	Class 8.8	M6S 24x75		19203422	0,3
25	8	Washer		TBRSUB 13x36		19200211	0,041
24	8	Screw	Class 8.8	M6S 12x50		19201681	0,055
23							
22							
21							
20							
19	222	Screw		RTS TX 5.5x19		19204943	0,00
18	222	Screw		KFTS 5.5x16		19204944	0,00
17	222	Screw		RTS TX 5.5x16		19204942	0,00
16	12	Protective stud		Dia.20x10		19100902	
15	4	Screw		RTS TX 4.8x13		19200242	0,00
14	8	Screw		RTS TX 4.8x16		19200320	0,00
13							
12	2	Clamp strip		30x6 #3	L= 4558	19151079	1,3
11	4	Clamp strip		30x6 #3	L= 6000	19151079	1,7
10							
9	1	Painted Clamp strip Alt. 2	White (RAL9016)	30x6 #2	L= 4558	51120	1,3
8	2	Painted Clamp strip Alt. 2	White (RAL9016)	30x6 #2	L= 6000	51120	1,7
7							
6	2	Clamp strip		15x3 #1	L= 4558	19151077	0,6
5	4	Clamp strip		15x3 #1	L= 6000	19151077	0,7
4	2	Link			11&12 mm	19122913	7
3	2	Safety arrester				19149915	50
2							
1	2	Bottom beam half		L= 8065	290x450	77808	342
Item	**Qty**	**Description**	**Material**	**Dimension**	**Remarks**	**Drawing/ art.no.**	**Weight kg/pc.**


GMR Aero Technic Hangar1
India
Megadoor 79014x23000/14000
Bottom beam assembly #1, 2, 4 & 5
Parts list no. 77807.xls
Ref. to assembly drawing no. 77807


Date: 2022-10-31
Project no: 84800
Designed by: EB
Revision: ---

Total weight (kg): **999**

DETAIL 3, SCALE (1:4)

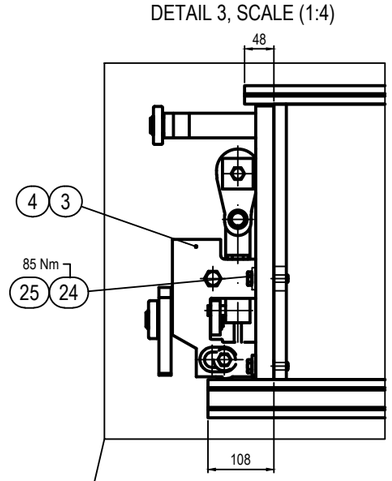

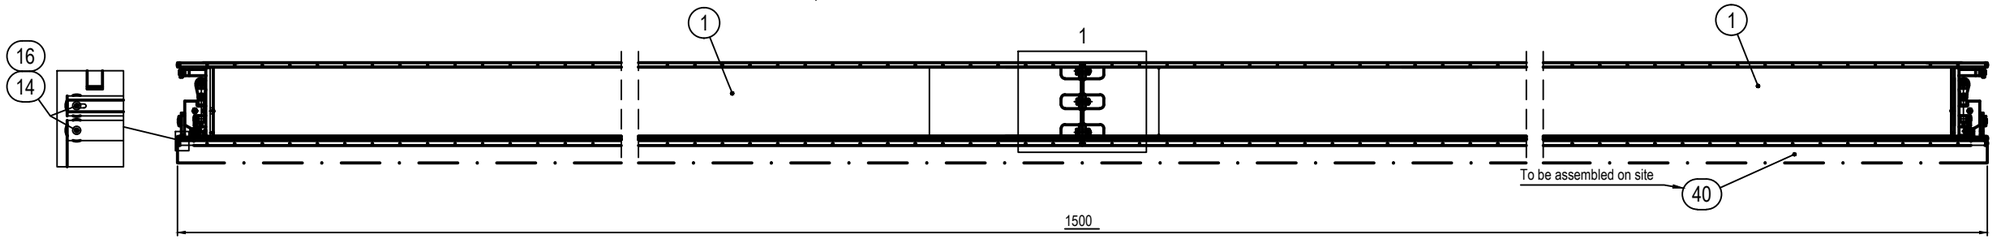


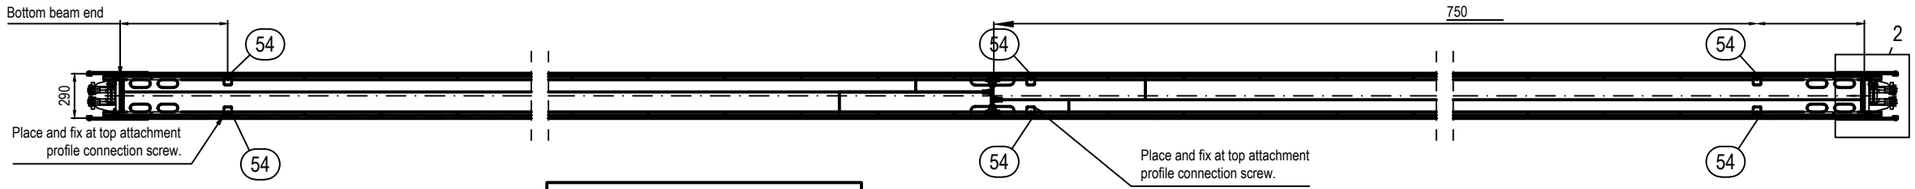


DRILL INSTRUCTIONS
Drill additional holes Ø5.5 thru attachment profiles into bottom beam if distance between bottom beam splice & 1st predrilled hole exceeds 250mm. Drill holes close to joint.

3


BOTTOM BEAM PREPARED FOR TRANSPORTATION
SCALE 1:10

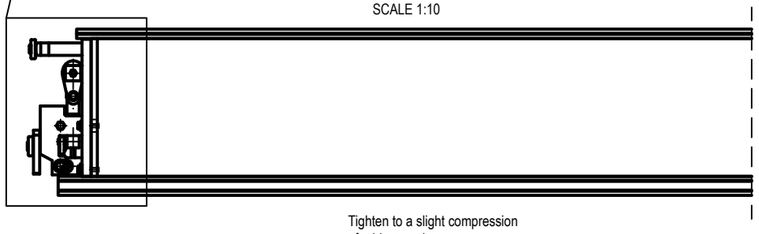

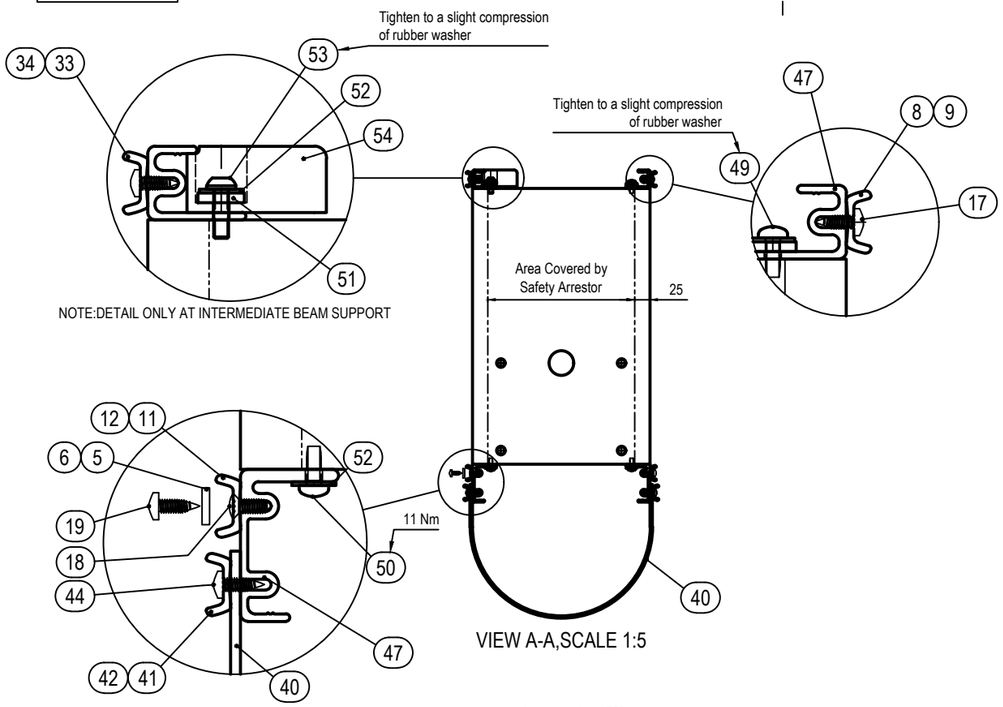


NOTE:DETAIL ONLY AT INTERMEDIATE BEAM SUPPORT

VIEW A-A,SCALE 1:5

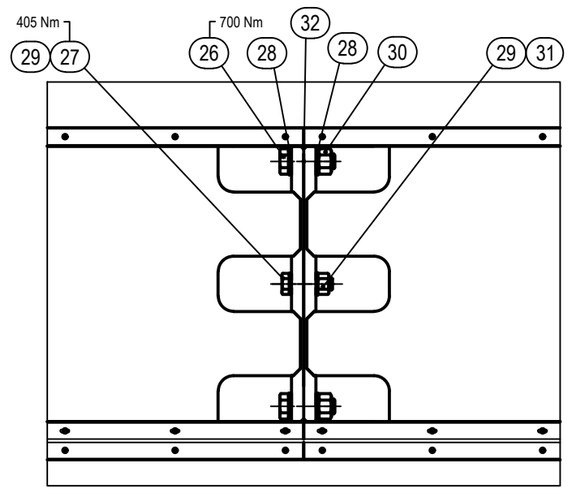


DETAIL 1, SCALE (1:5)

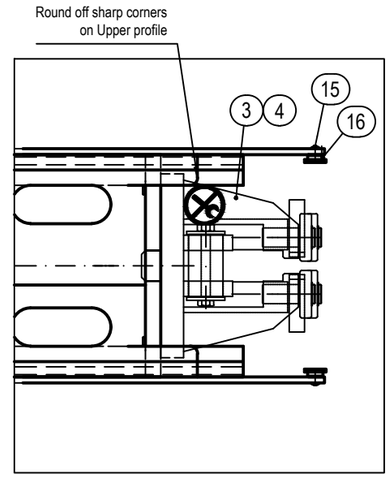

DETAIL 2, SCALE (1:4)


Beam length= 1500

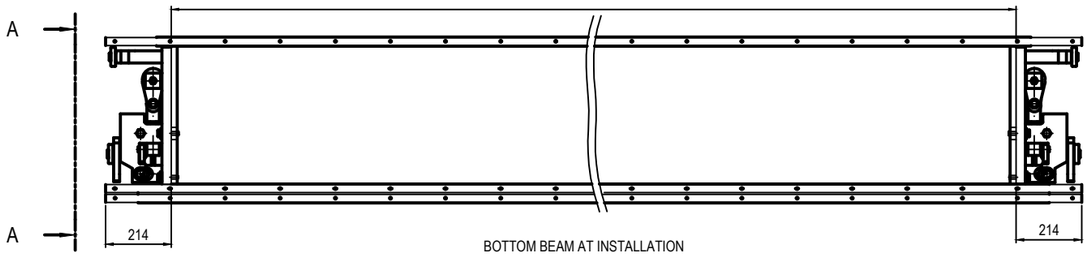


BOTTOM BEAM AT INSTALLATION
Interior view
SCALE 1:10

TITLE - MEGA DOOR				NIHVA TECHNOLOGIES PVT.LTD.PUNE
DWG NO -			QTY - 1	NIHVA Technologies Pvt. Ltd. Website - www.nihva.com
	NAME	SIGNATURE	DATE	PROJECT NO -
DRAWN	S.W		17-07-2025	PRODUCT -
CHK'D	P.M.		17-72025	SITE LOCATION -
APPV'D	V.T.		17-07-2025	
if any queries contact - supportautomation@nihva.com				REVISION -
ALL DIMENSION ARE IN mm		A3		SCALE - SHEET 1 OF 1


This document is the property of ASSA ABLOY Entrance Systems AB and shall not be reproduced or disclosed to a third party or used for any other unauthorized purpose.

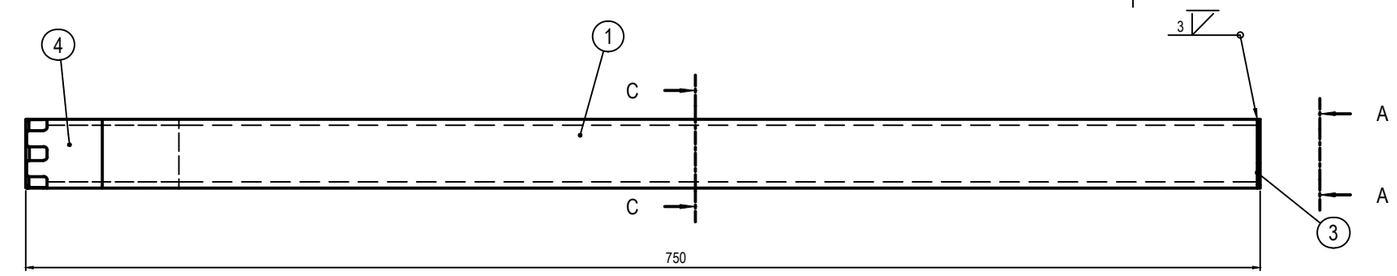

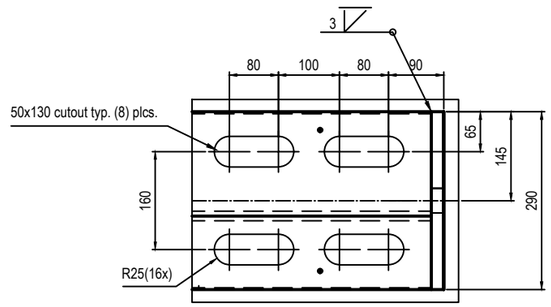



DETAIL A, SCALE (1:5)

HOLE TEMPLATE
Top of Bottom beam

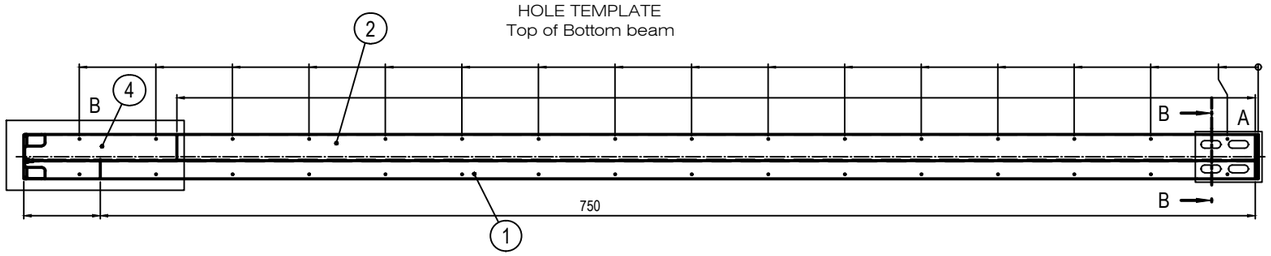


HOLE TEMPLATE
Bottom of Bottom beam

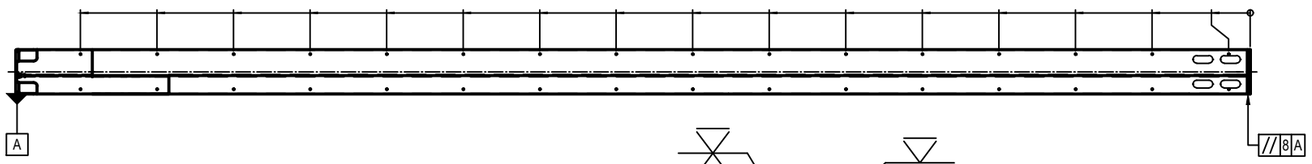


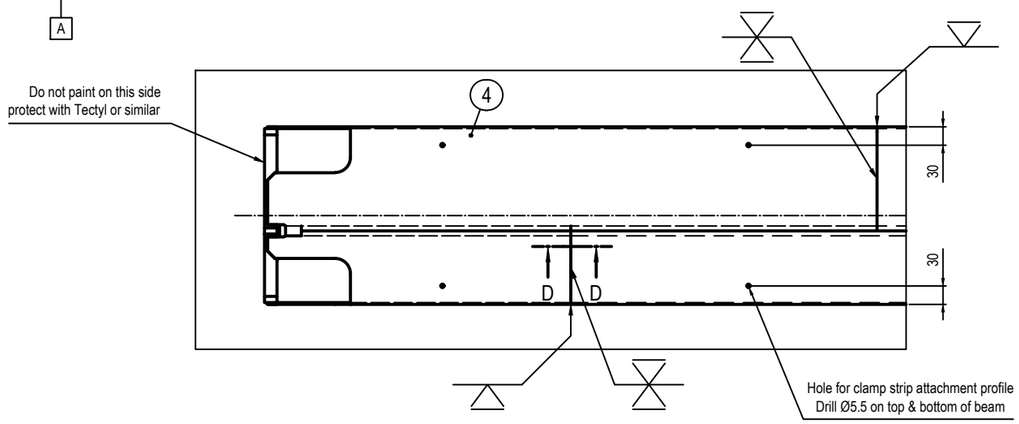

DETAIL B, SCALE (1:5)

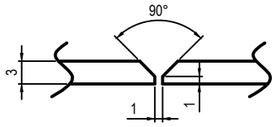


SECTION D-D, SCALE 1:1. Weld prep.

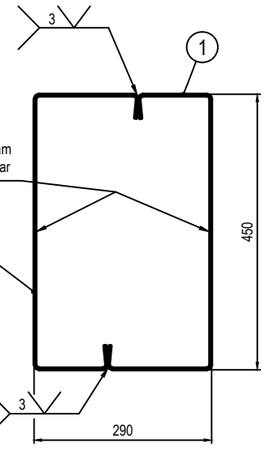

Section C-C
Scale 1:5


Surface treatment: A4-1500 Standard Color: Light grey (RAL 7047).
Surface treatment area: 1198 dm² Surface treatment area/m: 148.5 dm² Perimeter: 1480 mm Cross section area: 4776 mm² Weight: 342 kg
Wx = 660 cm3 Wy = 460 cm3 Zx = 806 cm3 Zy = - cm3 Ix = 14959 cm4 Iy = 6668 cm4
Grind all sharp edges and welding sparks after welding. This to prevent fabric wear.

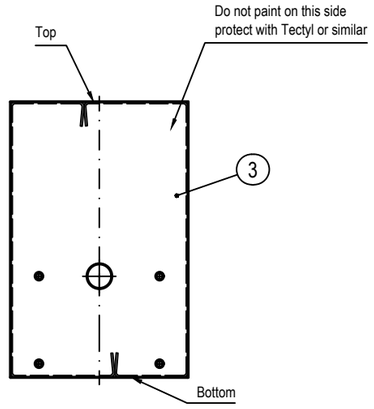

View A-A Scale 1:5



Section B-B
Scale 1:5

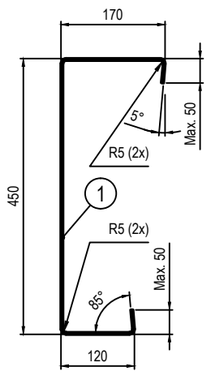

Pos 1 forming layout
Scale 1:5

TITLE - MEGA DOOR				NIHVA TECHNOLOGIES PVT.LTD.PUNE
DWG NO -			QTY - 1	Website - www.nihva.com
	NAME	SIGNATURE	DATE	PROJECT NO -
DRAWN	S.W		17-07-2025	PRODUCT -
CHK'D	P.M.		17-72025	SITE LOCATION -
APPV'D	V.T.		17-07-2025	
if any queries contact - supportautomation@nihva.com				REVISION -
ALL DIMENSION ARE IN mm		A3		SCALE - SHEET 1 OF 1

This document is the property of ASSA ABLOY Entrance Systems AB and shall not be reproduced or otherwise disclosed to a third party or used for any other unauthorized purpose.

Installation preparation, ref. to drawing no. A2-23869

41	2	Screw	cl 10.9	MF6S 12x30		19204118	
40	2	Fork pin washer				19141235	0,17
39	1	Set of guide rails				77824	385
38	4	Bottom seal clamp		L=84	Pos 2	62713	
37	2	Bottom seal clamp		L=210	Pos 1	62713	
36	2	Rubber fabric	EPDM	4x900x400		19203296	0,5
35	12	Parallel pin	SMS 2374	CP 5x40		19200363	
34	4	Tension pin	SMS 1663	FRP 6x30		19200972	
33	10	Tension pin	SMS 1663	FRP 6x10		19200373	
32	2	Tension pin	SMS 1663	FRP 4x10		19201678	
31	2	Nut	Cl. 8	M6M 20		19201687	0,073
30	2	Washer	HB 200	BRB 21x36		19200202	0,016
29	16	Washer	HB 200	BRB 13x24		19200333	0,005
28	1	Washer	HB 200	BRB 8.4x16		19200397	0,0017
27	2	Screw	Cl. 8.8	M6S 16x40		19200246	0,09
26	16	Screw	Cl. 8.8	M6S 12x50		19201681	0,055
25	104	Screw		M6SF-GF 10x30		19200455	0,028
24	88	Screw		M6SF-GF 8x20		19200233	0,014
23	1	Screw	Cl. 8.8	M6S 8x16		19203617	0,011
22	2	Screw	Cl. 8.8	M6SF-GF 5x16		19201978	0,0063
21	8	Screw		RTS TX 4.8x19		19200327	0,0027
20	16	Screw		RTS TX 4.8x13		19200242	0,0022
19	1	Bearing assembly				19123485	10
18	1	Bearing assembly				19123484	10
17	1	Suspension unit				19125059	10
16	2	Brush strip	Nylon 0.25	L=238	B=5, H=60 (51060)	19203460	
15	2	Brush strip bracket		L=238	F90° B=5, L=2000 (55590)	19203461	
14	1	Limit switch attachment plate				19143997	
13	1	Limit switch		IGS232		43998	
12	1	Trigger arm			L=350	43996	0,2
11	1	Fork pin				19141934	3,8
10	1	Set screw				19113946	0,48
9	1	Leaf spring				19113945	8,5
8	1	Hinge pin				19119857	36
7	1	Mullion				77823	1373
6	4	Shaft nut		M40x1.5	KM8	19201148	0,078
5	4	Thrust washer			GLY.PXG 527802 A	19201700	
4	2	Washer				19112647	0,3
3							
2	1	Fork				19123489	137
1	1	Mullion extension				77821	189
item	**qty**	**description**	**material**	**dimension**	**remarks**	**art.no/ drwng.no.**	**weight kg/pc.**

GMR Aero Technic Hangar1 **Total weight (kg): 2171**

India


Megadoor 79014x23000/14000 Date: 2022-11-02

Swing-up mullion #45 **Project no.** 84800

Parts list. 77820.xls Designed: EB

Ref. to assembly drawing no. 77820.dwg Revision: --

Stated tightening torque refers to dry screw and nut, unless noted otherwise, and a torque wrench with max. tolerance of ±5%. At re-check, the tightening torque must be within ±25% of stated torque.

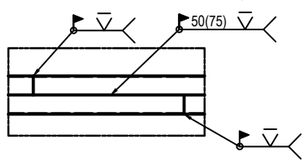



Mullion weld joint, scale 1:20


Electrode: ESAB OK48
Filarc 88S
Maxeta 22
Lincoln 7018
Hyundai SM-70
or similar.

NOTE!
Max. allowed compression of spring is 10mm


Springs should be set to a minimum of compression when mullion is hanging straight in vertical position. Adjust set screws simultaneously when adjustment is required to ensure a positive fit of base pin in floor guide.

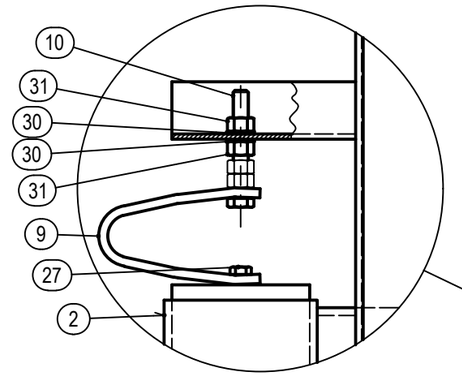

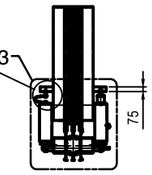


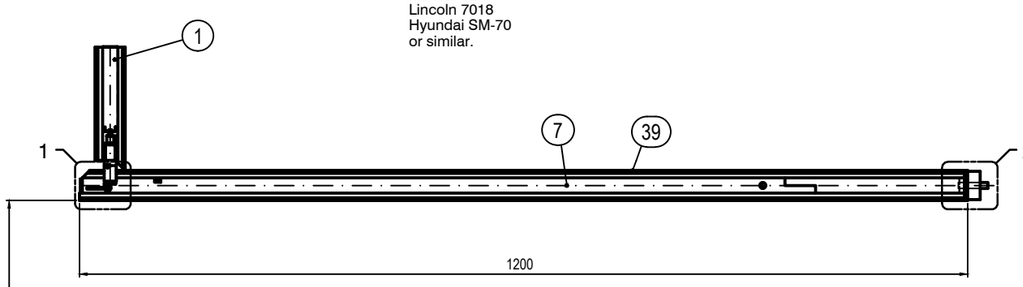


View from inside building

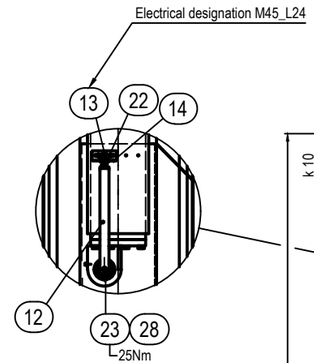


Set trigger arm so that limit switch is activated when mullion is in vertical position.
Drill Ø5x10 hole in shaft for tension pin.

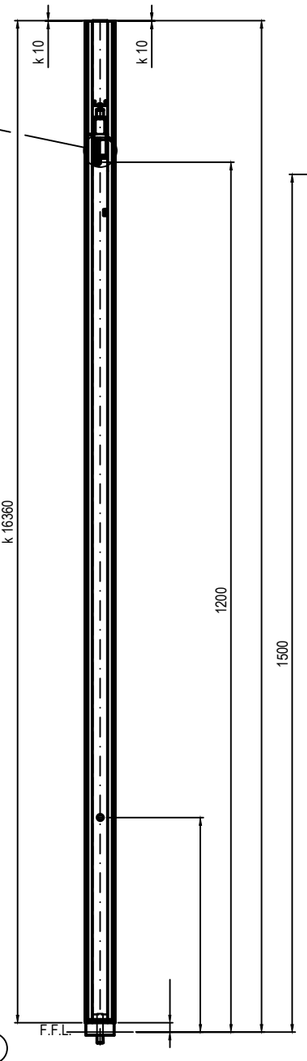


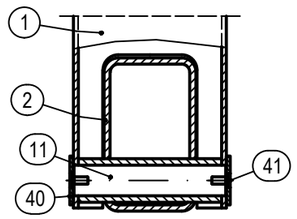


Section through
Mullion Extension Joint, typ.

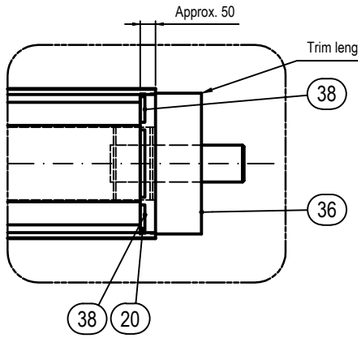


Detail 2, scale 1:10

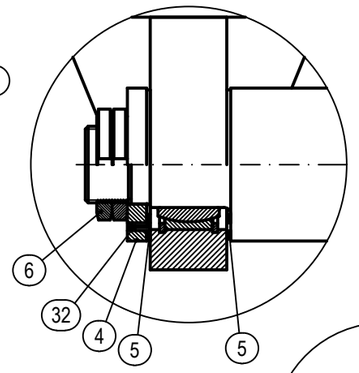


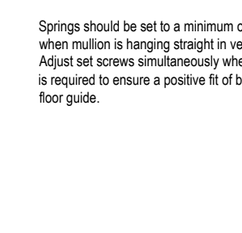


Grease bearing assemblies after mounting

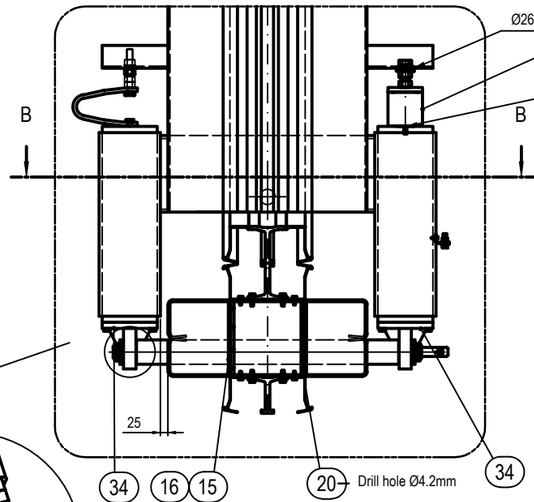


Detail 3, scale 1:10

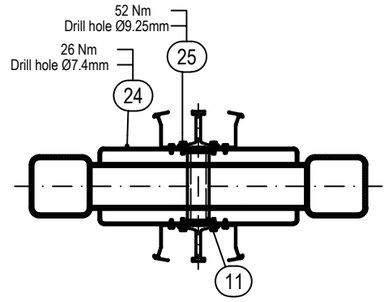


Section B -- B

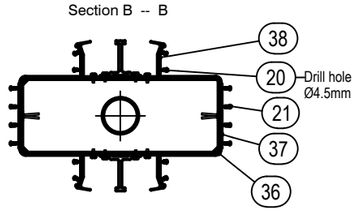

View A -- A, scale 1:10

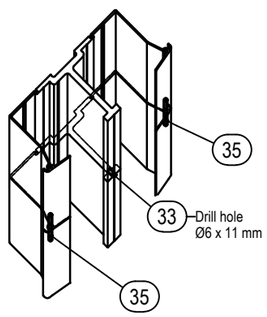


Painting instructions acc. to 44626.dwg

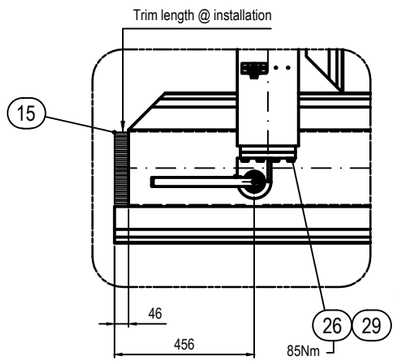


Detail 1, scale 1:10

Welding of shaft at layout with hinge assembly, typ.

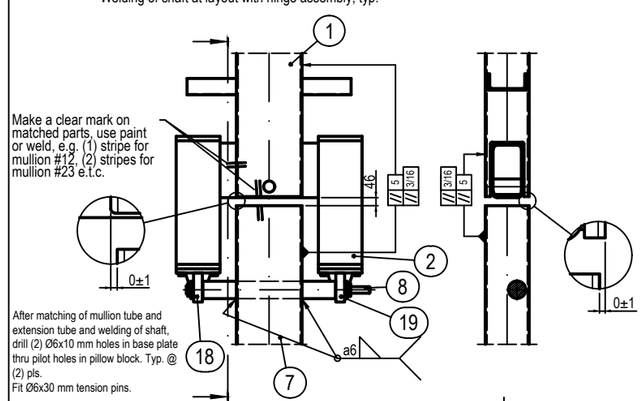


After matching of mullion tube and extension tube and welding of shaft, drill (2) Ø6x10 mm holes in base plate thru pilot holes in pillow block. Typ. @ (2) pls.
Fit Ø6x30 mm tension pins.

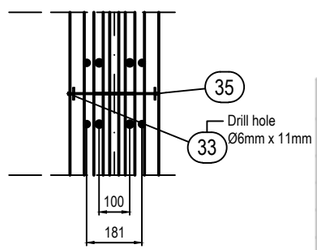



Detail @ System 1500
Guide Rail Joint, typ.


TITLE - MEGA DOOR				NIHVA TECHNOLOGIES PVT.LTD.PUNE
DWG NO -			QTY - 1	Website - www.nihva.com
	NAME	SIGNATURE	DATE	PROJECT NO -
DRAWN	S.W		17-07-2025	PRODUCT -
CHK'D	P.M.		17-72025	SITE LOCATION -
APPV'D	V.T.		17-07-2025	
if any queries contact - supportautomation@nihva.com				REVISION -
ALL DIMENSION ARE IN mm		A3		SCALE - SHEET 1 OF 1


This document is the property of ASSA ABLOY Entrance Systems AB and shall not be used without permission, nor disclosed to a third party or used for any other unauthorized purpose.

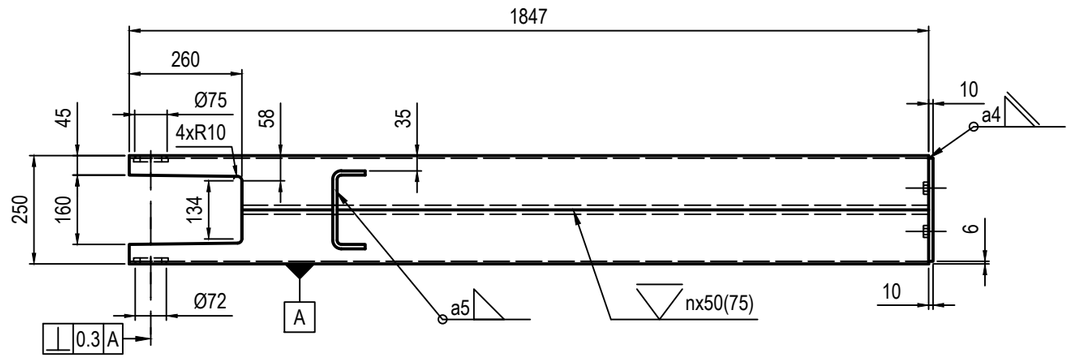

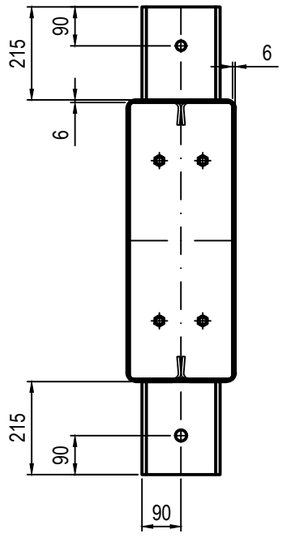


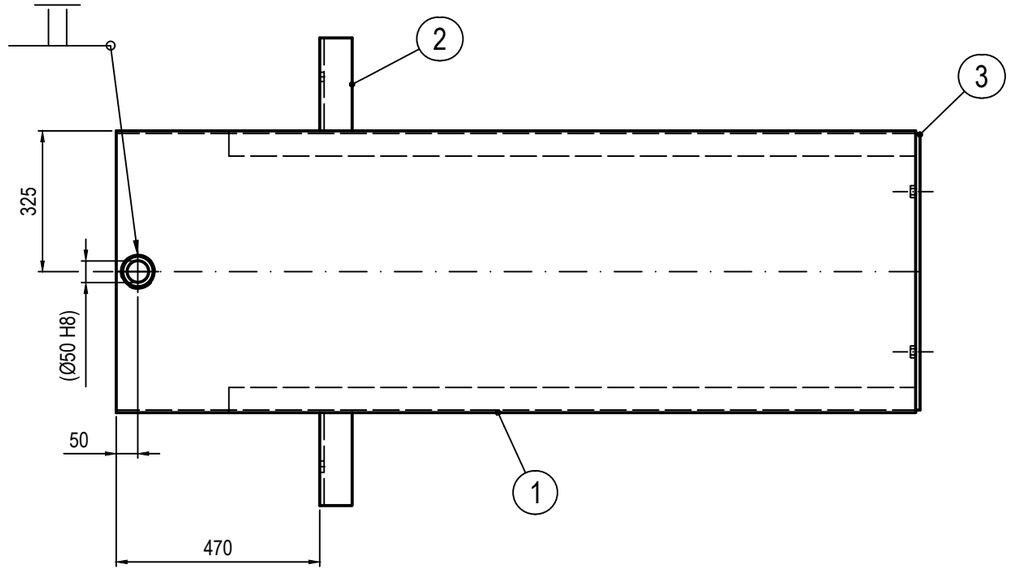

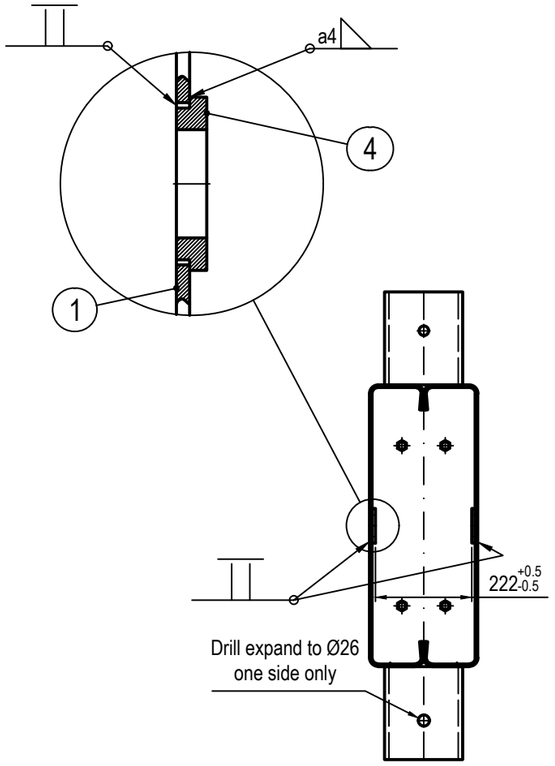

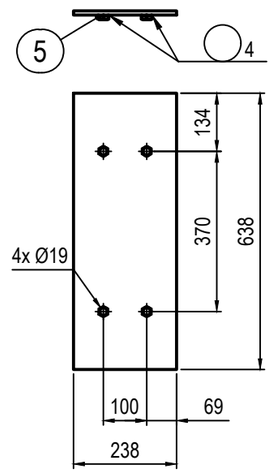

Item #3 & #5

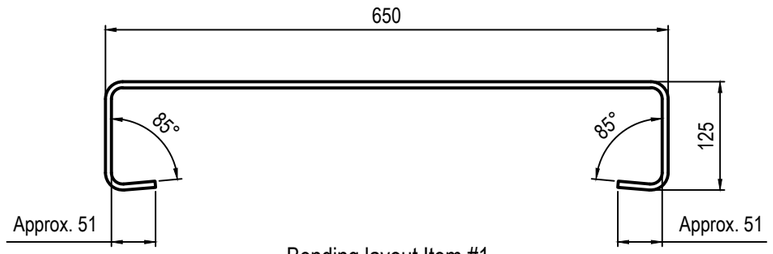



Bending layout Item #1,
scale1:5


Painted colour light grey (RAL 7047). Standard acc. to A4-1500
Painting instructions acc. to 44626.dwg
Section area item #1= 5755 (mm^2)
Surface treatment area= 3.3 (m^2)
Weight= 189 (kg)


TITLE - MEGA DOOR				NIHVA TECHNOLOGIES PVT.LTD.PUNE
DWG NO -			QTY - 1	Website - www.nihva.com
	NAME	SIGNATURE	DATE	PROJECT NO -
DRAWN	S.W		17-07-2025	PRODUCT -
CHK'D	P.M.		17-72025	SITE LOCATION -
APPV'D	V.T.		17-07-2025	
if any queries contact - supportautomation@nihva.com				REVISION -
ALL DIMENSION ARE IN mm			A3	SCALE - SHEET 1 OF 1


This document is the property of ASSA ABLOY Entrance Systems AB and shall not without our written permission be copied, imparted to a third party or used for any other unauthorized purpose.

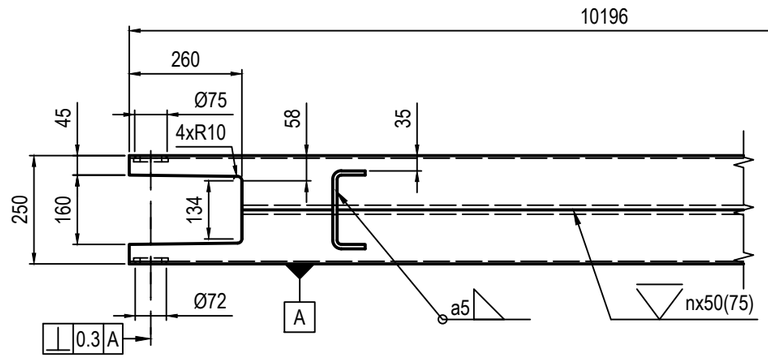


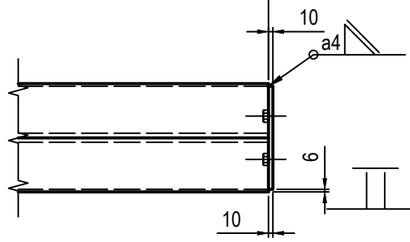


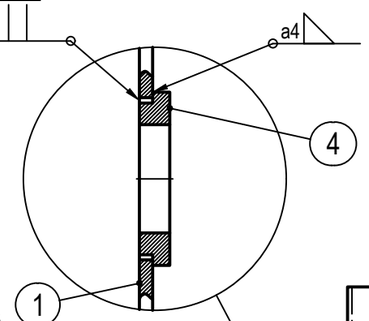


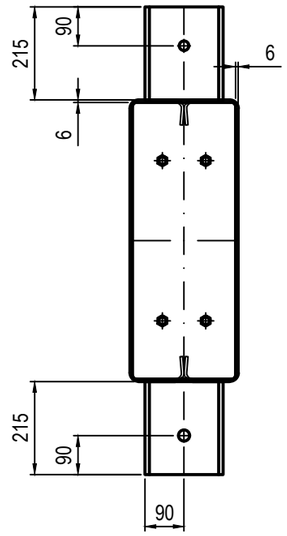

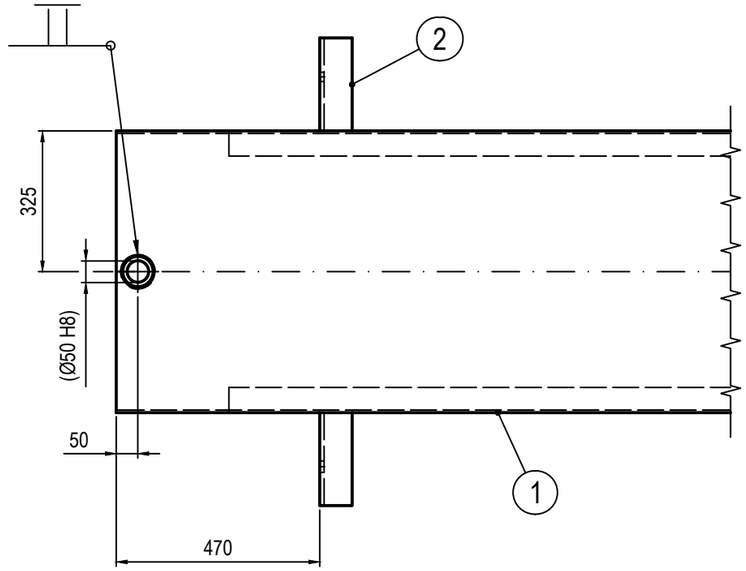


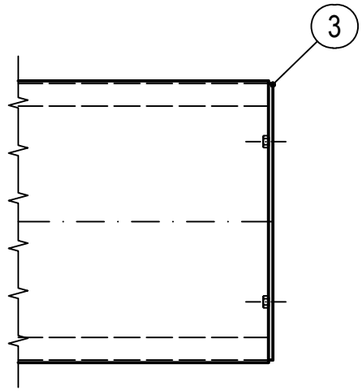

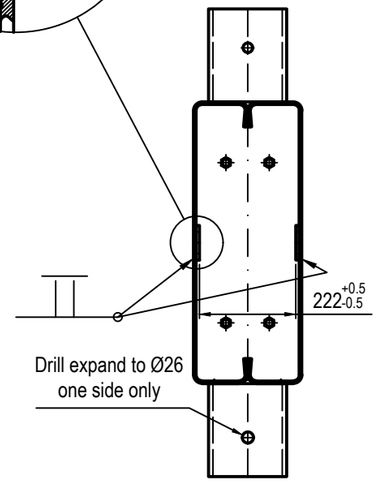

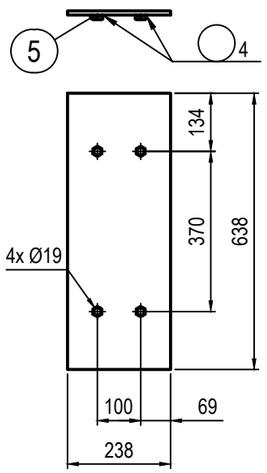

Item #3 & #5

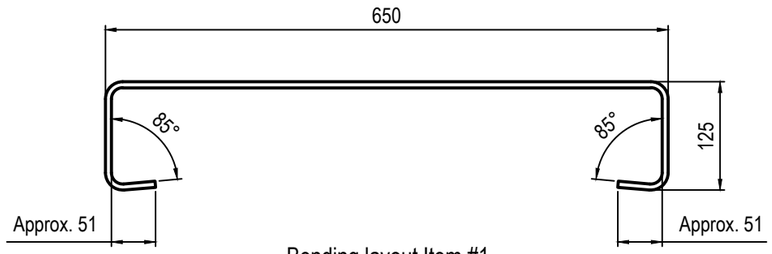



Bending layout Item #1,
scale1:5

Painted colour light grey (RAL 7047). Standard acc. to A4-1500
Painting instructions acc. to 44626.dwg
Section area item #1= 5755 (mm^2)
Surface treatment area= 18.4 (m^2)
Weight= 944 (kg)


TITLE - MEGA DOOR				NIHVA TECHNOLOGIES PVT.LTD.PUNE
DWG NO -			QTY - 1	Website - www.nihva.com
	NAME	SIGNATURE	DATE	PROJECT NO -
DRAWN	S.W		17-07-2025	PRODUCT -
CHK'D	P.M.		17-72025	SITE LOCATION -
APPV'D	V.T.		17-07-2025	
if any queries contact - supportautomation@nihva.com				REVISION -
ALL DIMENSION ARE IN mm			A3	SCALE - SHEET 1 OF 1

This document is the property of ASSA ABLOY Entrance Systems AB and shall not without our written permission be copied, imparted to a third party or used for any other unauthorized purpose.

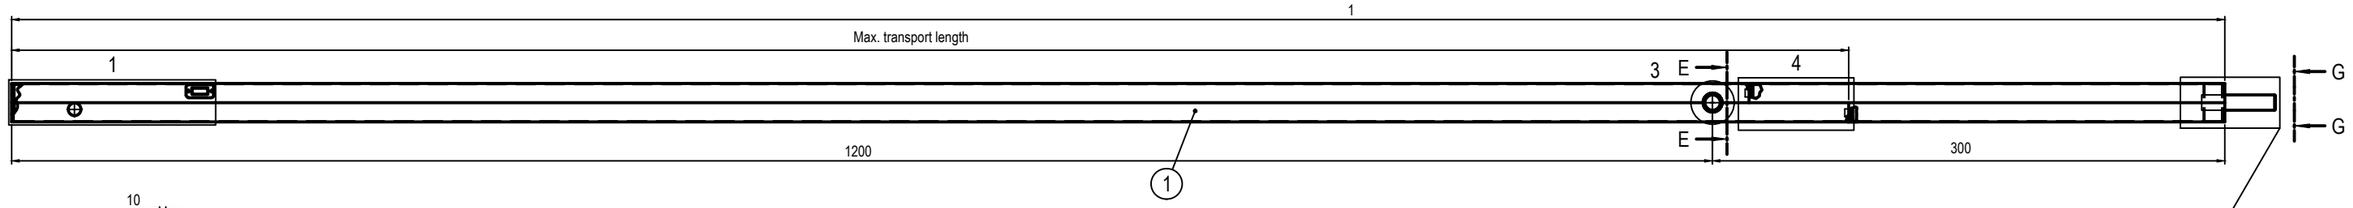


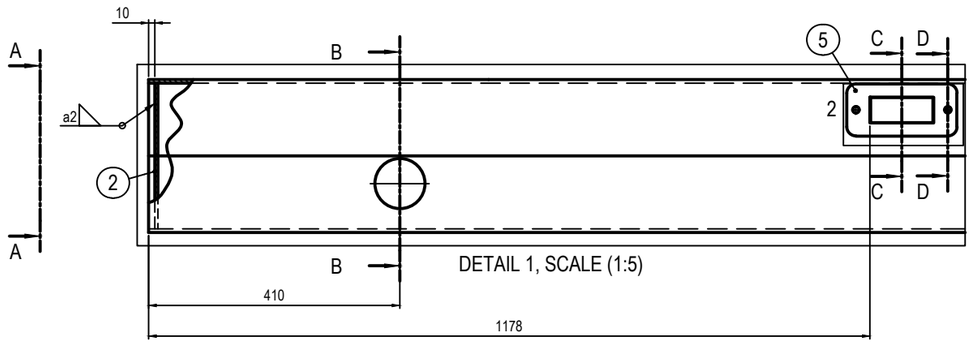


DETAIL 1, SCALE (1:5)

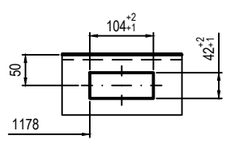


DETAIL 2, SCALE (1:5)
Item 5 not shown.

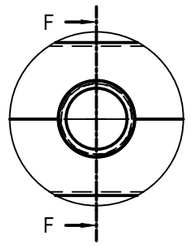


DETAIL 3, SCALE (1:5)

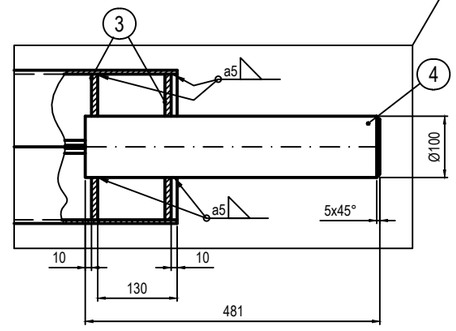

SCALE (1:5)

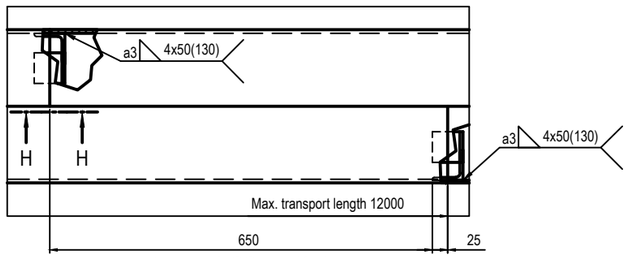


DETAIL 4, SCALE (1:5)
Splice method item #1.

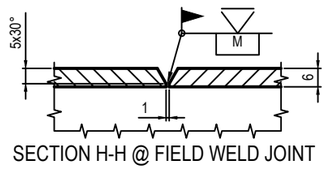


SECTION H-H @ FIELD WELD JOINT

ELECTRODES:
ESAB OK 48.00
Filarc 88S
Maxeta 22
Lincoln 7018
Hyundai SM-70
or similar.

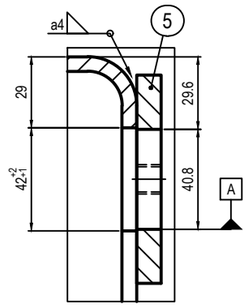

DETAIL 5, SCALE (1:5)

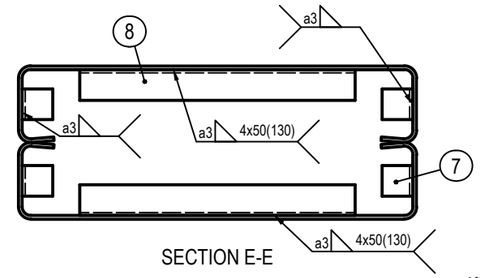


SECTION E-E


After welding item 5 to mullion tube,drill 4xØ10,2 and tap for M12 screw.




SECTION A-A (1:5)

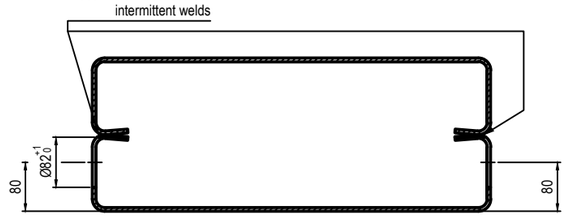


SECTION B-B(1:5)

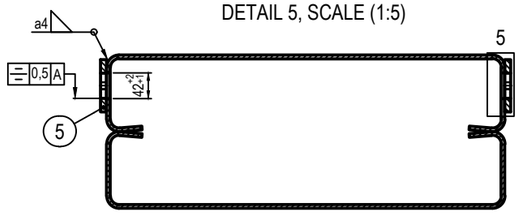


SECTION C-C (1:5)

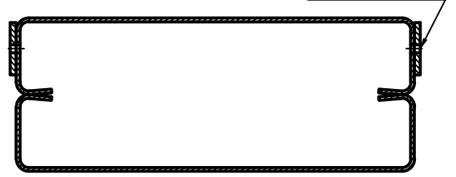


SECTION D-D

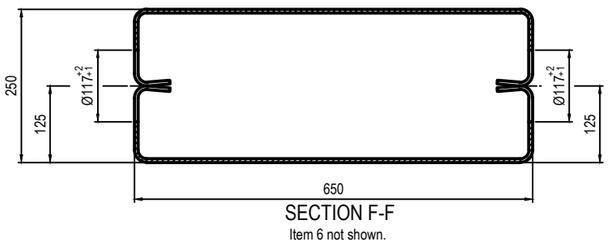


SECTION F-F
Item 6 not shown.

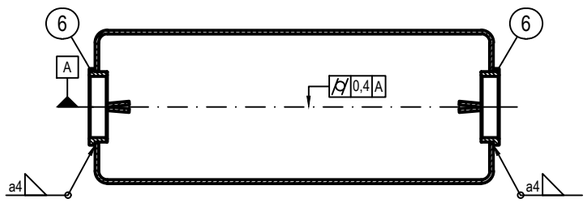


SECTION F-F'

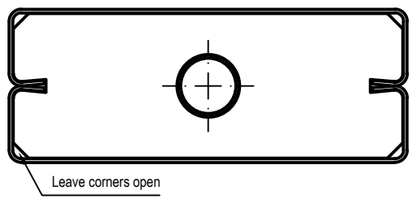


SECTION G-G

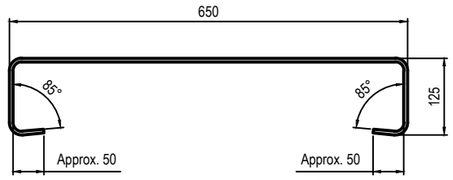

Bending layout item #1, scale 1:5

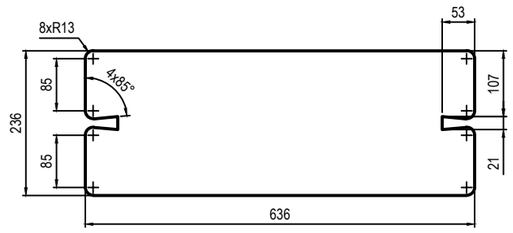

Item #2 (1:5)

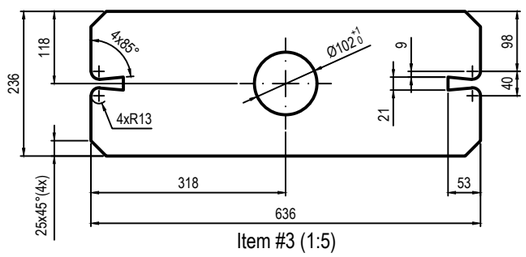

Item #3 (1:5)

TITLE - MEGA DOOR				NIHVA TECHNOLOGIES PVT.LTD.PUNE
DWG NO -			QTY - 1	NIHVA Technologies Pvt. Ltd. Website - www.nihva.com
	NAME	SIGNATURE	DATE	PROJECT NO -
DRAWN	S.W		17-07-2025	PRODUCT -
CHK'D	P.M.		17-72025	SITE LOCATION -
APPV'D	V.T.		17-07-2025	
if any queries contact - supportautomation@nihva.com				REVISION -
ALL DIMENSION ARE IN mm			A3	SCALE - SHEET 1 OF 1

This document is the property of ASSA ABLOY Entrance Systems AB and shall not be reproduced or disclosed to any third party or used for any other unauthorized purpose.

100	1	Guide rail, fixed straight		500		51529	4,3
99	1	Guide rail, fixed angled		660		51530	4,7
81	1	Seal angle		1846		19114552	2,7
80	1	Seal angle		1846		19114552	2,7
71	1	Seal angle		962		19114552	1,4
70	1	Seal angle		962		19114552	1,4
61	1	Seal angle		2012		19114552	2,9
60	1	Seal angle		2012		19114552	2,9
51	1	Seal angle		916		19114552	1,3
50	1	Seal angle		916		19114552	1,3
41	2	Seal angle		5500		19114552	7,9
40	2	Seal angle		5500		19114552	7,9
31	2	Seal angle		6000		19114552	8,7
30	2	Seal angle		6000		19114552	8,7
11	2	Seal angle		2041		19114552	2,9
10	2	Seal angle		2041		19114552	2,9
8	1	Guide rail		1346		19149911	11,9
7	1	Guide rail		962		19149911	8,5
6	1	Guide rail		1352		19149911	12,0
5	1	Guide rail		916		19149911	8,1
4	2	Guide rail		5500		19149911	48,8
3	2	Guide rail		6000		19149911	53,2
2	2	Guide rail		642		19149911	5,7
1	2	Guide rail		1399		19149911	12,4
item	**qty**	**description**	**material**	**length**	**remarks**	**art.no.**	**weight kg/pc**

GMR Aero Technic Hangar1
India
Megadoor 79014x23000/14000
Swing-up Mullions, Guide rails #12 & 45
Parts list no. 77824.xls
Ref. to assy. Drwng. no. 77824.dwg

Date: 2022-11-02
Project no: 84800
Designed by: EB
Revision: ---

Total weight / mullion (kg): 385