PO NO: 206

DOOR NO:- D1 TO D3

QTY- 03 NOS

MATERIAL:-G.I

DOOR HANDLING:
SINGLE DOOR ???? HAND ACTIVE

INFILL: HONEY COMB

RAL NO FRAME:- ????
RAL NO LEAF:- ????

PANIC BAR :
MODEL NO.- LOCKWOOD MAKE
PE RM501P
PHT LOCK :
MODEL NO. LOCKWOOD MAKE
PE ACC004


DOOR CLOSER : STD ARM - MODEL NO-YADC 6003 -YALE MAKE

ACCESSORIES:-
1.SS BALL BEARING HINGES
3S2BB403030-CE-M =YALE MAKE
2.SMOKE SEAL-S88BL-PEMKO MAKE


FRAME SHEET THIK.1.2mm
LEAF SHEET THIK.0.8 mm

POWDER COATED METAL CAP WITH RAL


2 HRS FIRE RATED

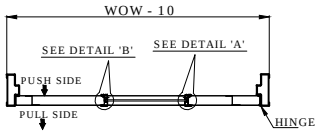

TOP VIEW

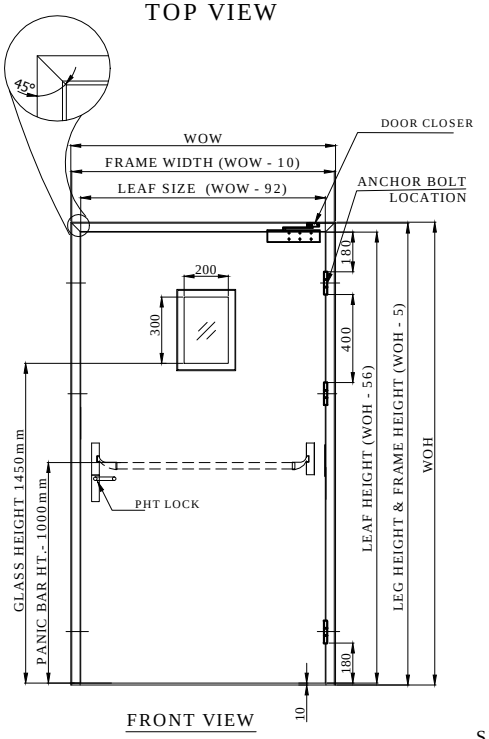


FRONT VIEW

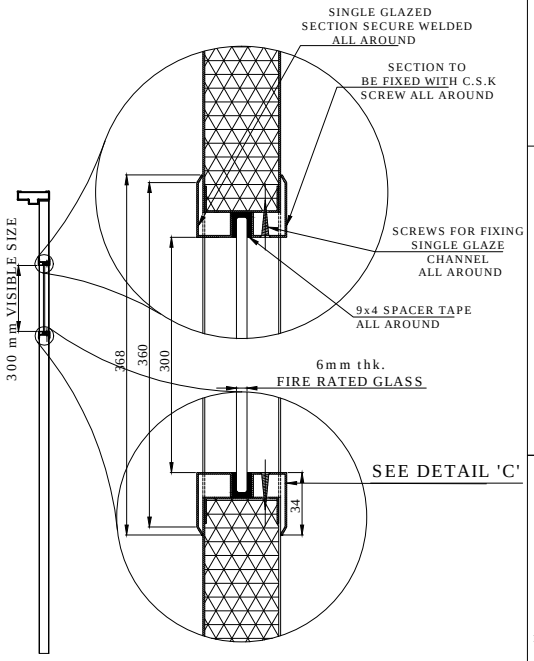


SIDE VIEW
SECTION A-A'

SINGLE GLAZE FIXING DETAIL

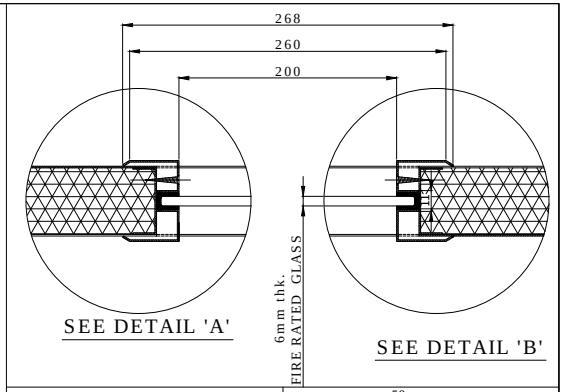



SEE DETAIL 'A'

SEE DETAIL 'B'

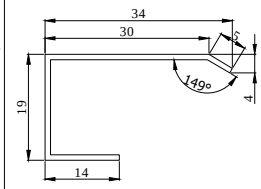


SEE DETAIL 'C'

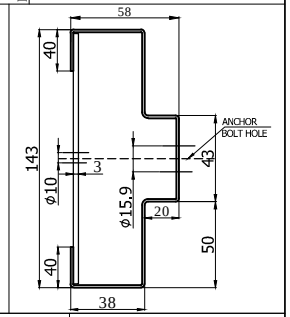

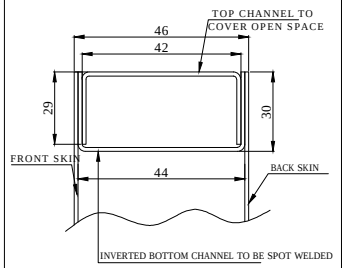

DOOR TOP SECTION DETAIL

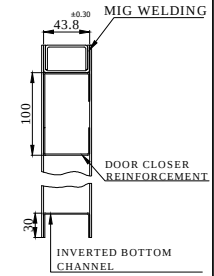

DOOR BOTTOM & TOP DETAIL

SR. NO	WALL OPENING WIDTH	WALL OPENING HEIGHT	QTY	RAL	LOCATION	HARDWARE
12	900	1800	02	3020	Admin Building (IH) - Fire Shaft	Single leaf Metal door with vision panel
11	900	2375	01	9002	Block G - Security cabin - white colour	Single leaf metal door with Vision Panel, Hinges , Door closer , Single point panic bar, with external trim
10	900	2380	01	9002	Block G - Security cabin - white colour	Single leaf metal door with Vision Panel, Hinges , Door closer , Single point panic bar, with external trim
09	1200	2100	12	3020	Block F	Hinges , Door closer , Single point panic bar, with external trim
08	1200	2100	04	3020	Block D	Hinges , Door closer , Single point panic bar, with external trim
07	1200	2100	12	3020	Block C	Hinges , Door closer , Single point panic bar, with external trim
06	1200	2400	01	3020	Block B - First floor	Single leaf metal door with vision panel, Hinges , Door closer , Single point panic bar with external trim
05	1200	2100	01	9002	Block B - Metering Kiosk (GD6B)	Hinges , Door closer , Single point panic bar , Non-Fire rated Glass 300X300mm
04	1200	2100	01	9002	Block D - Metering Kiosk (GD6B)	Hinges , Door closer , Single point panic bar , Non-Fire rated Glass 300X300mm
03	1200	2100	01	9002	Block C - Metering Kiosk (GD6B)	Hinges , Door closer , Single point panic bar , Non-Fire rated Glass 300X300mm
02	1200	2100	01	9002	RMU 2 (GD6B)	Hinges , Door closer , Single point panic bar , Non-Fire rated Glass 300X300mm
01	1200	2100	01	3020	A-Block North Side Mezzanine Exit Door (GD2)	Hinges , Door closer , Single point panic bar

TOLERANCE - ±05mm

This drawing & design is the property of NIHVA TECHNOLOGIES. Not to be sold or copied to any other concern.

TITLE: FIRE RATED SINGLE LEAF STEEL DOOR

NIHVA TECHNOLOGIES PVT. LTD.

NIHVA TECHNOLOGIES PVT. LTD. PUNE
Tel : 020 66304033
Email:- info@nihva.com
Website:- www.nihva.com

	NAME	SIGN	DATE
DRAWN	P.V.A		16.03.2019
CHECK	V.M.T		16.03.2019
APPRD.			

CLIENT - SYNERGY
PROJECT - EMBASSY
SITE LOCATION - CHAKAN, PUNE.

If any queries contact : design@nihva.com

DWG. NO. : NIHVA/18-19/0291 REV- 0

ALL DIMENSION ARE IN mm

SCALE: NTS WT: SHEET: 01 OF 01