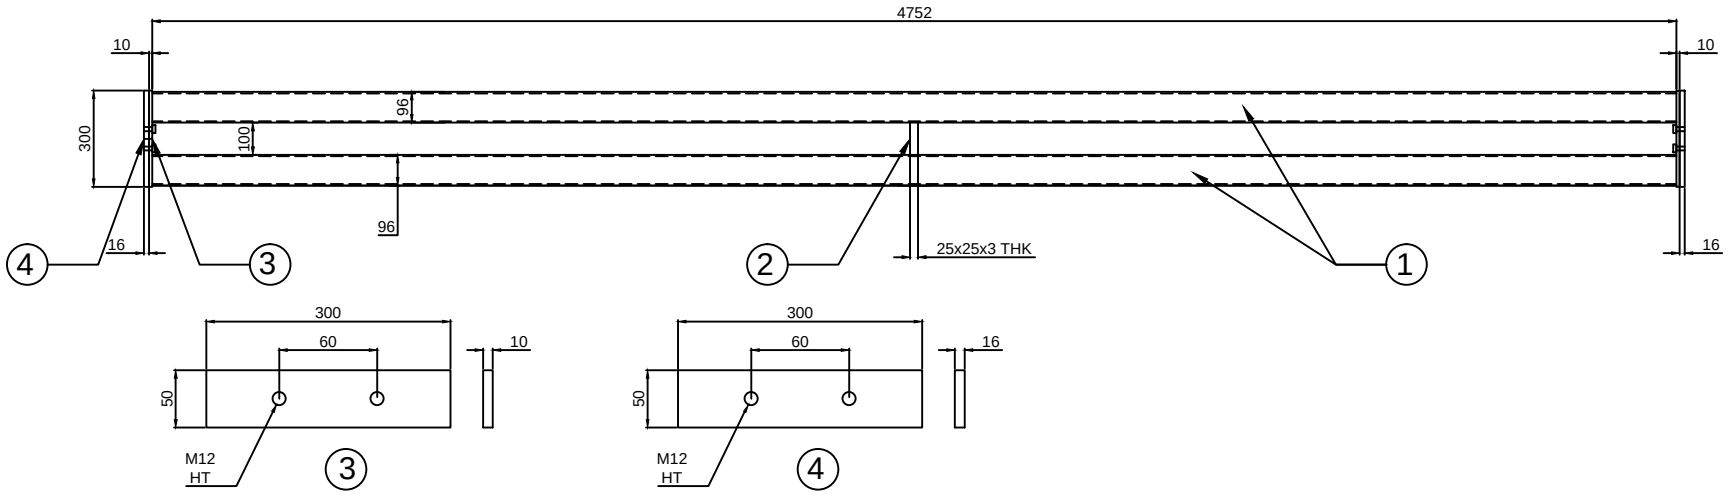

TOP SIDE

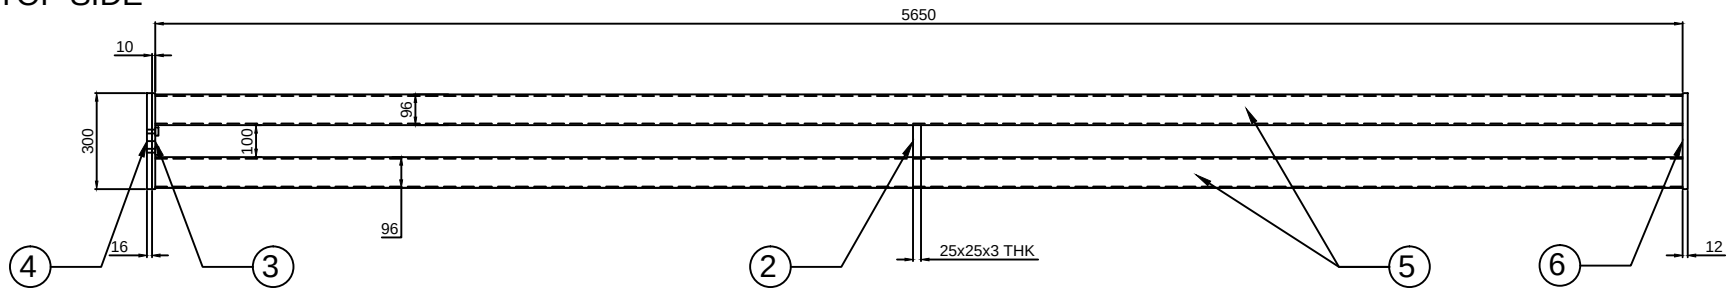

SR NO	DESCRIPTION	SPECIFICATION	QTY
6	MS FLAT	300 X 12 THK X 500L	8 NOS
5	R. TUBE	96 X 48 X 4.8 THK X 5650L	28 NOS
4	MS FLAT	50 X 16 X 300L	26 NOS
3	MS FLAT	50 X 10 X 300L	26 NOS
2	SQ. TUBE	38 X 38 X 4 THK X 100L	4 NOS
1	R. TUBE	96 X 48 X 4.8 THK X 4750L	8 NOS

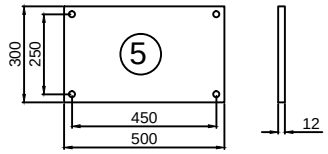

This drawing & design is the property of NIHVA TECHNOLOGIES. Not to be sold or copied to any other concern.

TITLE: STRUCTURE COLUMN

	NAME	SIGN	DATE
DRAWN	P.A		11.12.19
CHECK	G.J		11.12.19
APPRD.			

If any queries contact : design@nihva.com

ALL DIMENSION ARE IN mm

NIHVA TECHNOLOGIES PVT. LTD.
NIHVA TECHNOLOGIES PVT. LTD. PUNE
Tel : 020 66304033
Email:- info@nihva.com
Website:- www.nihva.com

CLIENT -

PROJECT -

SITE LOCATION -

DWG. NO. : NIHVA/19-20/VDR/243

SCALE: NTS | WT: | REV- 00