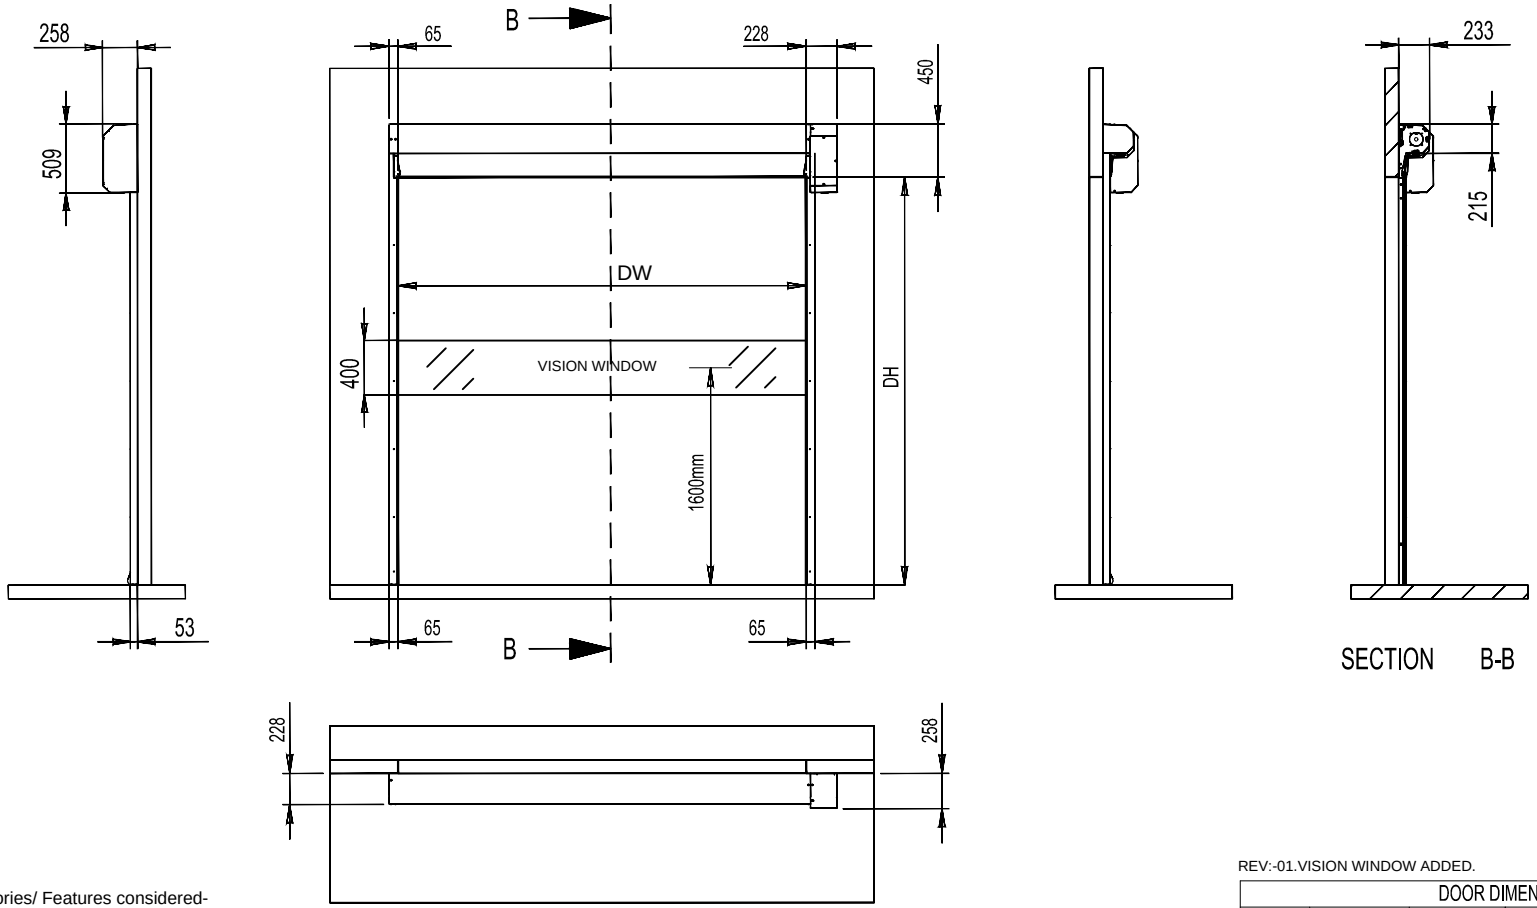


REV:-01.VISION WINDOW ADDED.

DOOR DIMENSION				
SR NO	DW	DH	MOTOR LOCATION	QUANTITY
1	2420	3000	RIGHT HAND SIDE	18
2	2420	3000	LEFT HAND SIDE	01

Accessories/ Features considered-
1. Soft bottom safety edge.
2. Push buttons both side.
3. Magnetic loop detector - Outside
4. Emmergency stop
5. Safety catch
6. Flashing lights both side
7. Manual Hand Crank from One Side

Power Supply(Supply & UPS is in client's scope)

1. If motor is single phase then Single phase 230V, 50 Hz supply required. UPS Capacity- 2 KVA/ door
2. If motor is three phase then Three phase 430V, 50 Hz supply required. UPS Capacity- 3 KVA/ door

Door Curtain color- Grey (RAL 7035)
Note- All required civil work will be client's scope.

This drawing & designing is the property of NIHVA TECHNOLOGIES. Not to be sold or copied to any other concern.

TITLE: HIGH SPEED DOOR HS9020

NIHVA TECHNOLOGIES PVT. LTD.

NIHVA TECHNOLOGIES PVT. LTD. PUNE
Tel : 020 66304033
Email:- info@nihva.com
Website:- www.nihva.com

	NAME	SIGN	DATE
DRAWN	SURAJ		07/03/18
CHECK	OMKAR		07/03/18
APPROVAL	SHEKHAR		07/03/18

If any queries contact : design@nihva.com

ALL DIMENSION ARE IN mm

CLIENT - DEV TECHNOSKILL
PROJECT - AMAR TEA PROJECT
SITE - UMARGAON, GUJARAT
DWG. NO. : NIHVA/17-18/0357/R01 REV- 01
SCALE: NTS WT: SHEET: 01 OF 01