
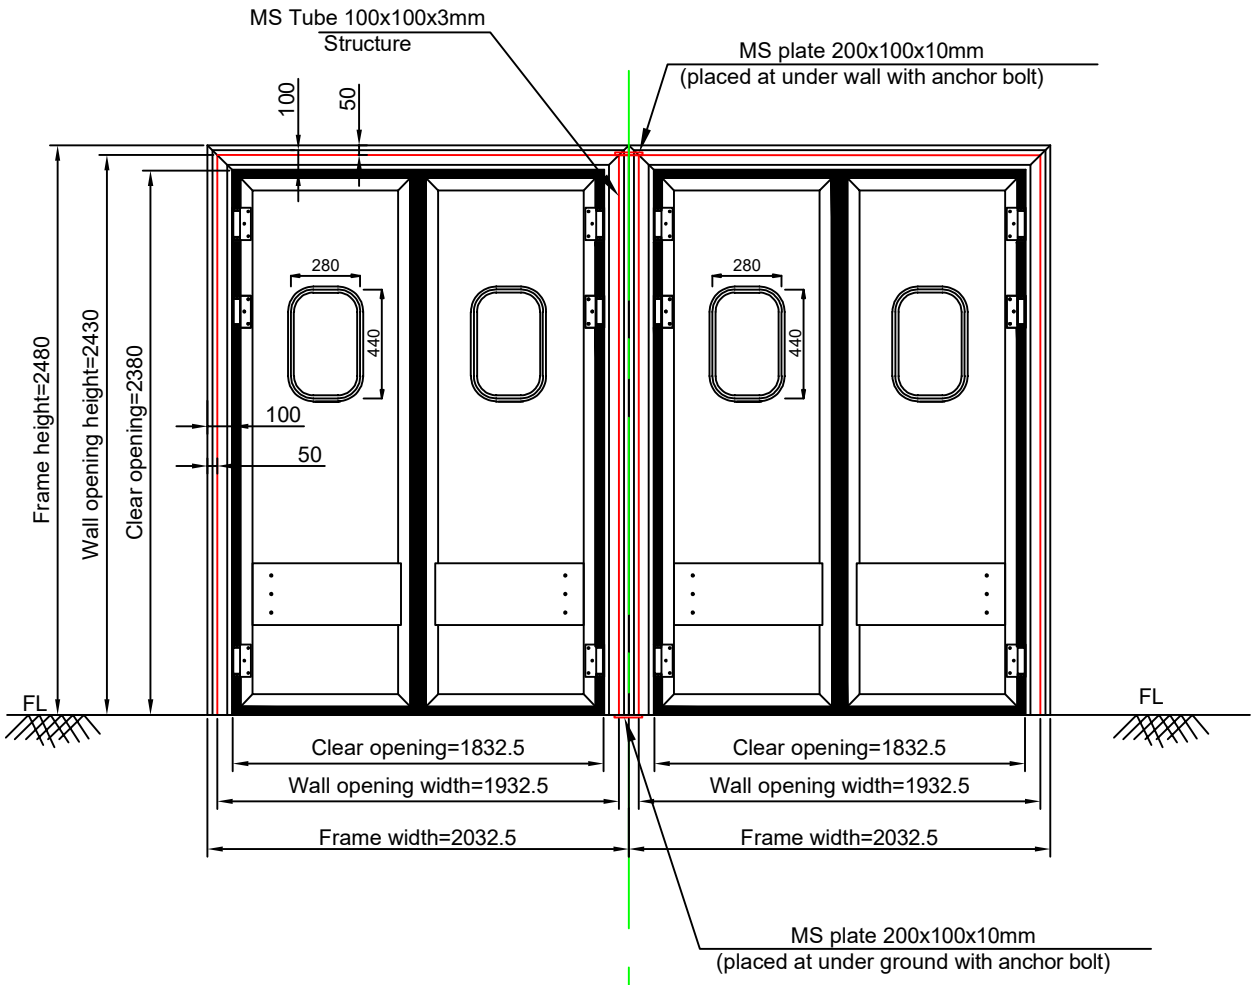


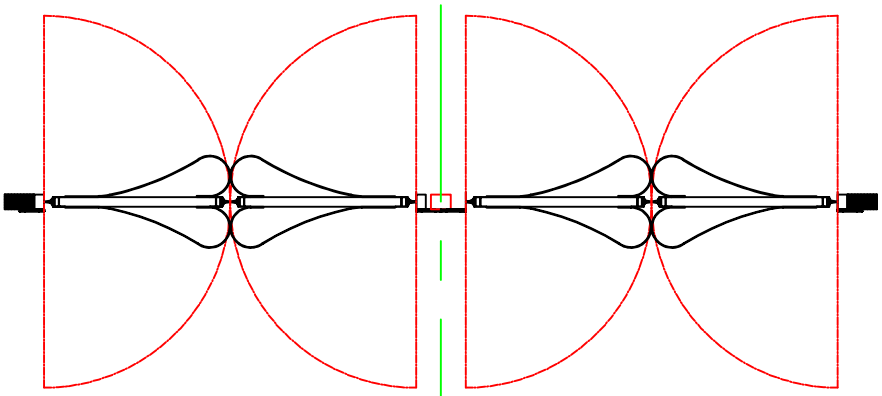

LEAF FINISH : PE / PCGI
LEAF THICKNESS : 40 MM
HINGES MOC : DOUBLE ACTION STAINLESS STEEL
VIEW WINDOW : 1 UNIT ON EACH LEAF
VIEW WINDOW HEIGHT : 440 MM
VIEW WINDOW WIDTH : 280 MM
VIEW WINDOW POSITION FROM FFL : 1500 MM

Note:
1.All dimension are in mm
2.All Civil work and structure will be in client scope
3.Structure place at the front side(same line in existing wall)

This drawing & design is the property of NIHVA TECHNOLOGIES. Not to be sold or copied to any other concern.

TITLE:- NIHVA Make NFF3 Flip Flap Door

NIHVA TECHNOLOGIES PVT. LTD.
NIHVA TECHNOLOGIES PVT. LTD. PUNE
Tel : 020 66304033
Email:- info@nihva.com
Website:- www.nihva.com

	NAME	DATE	SIGN
DRAWN	SUJATA	22-03-2022	
CHECK	G.P	22-03-2022	
APPRD.	P.J	22-03-2022	

If any queries contact : design@nihva.com

ALL DIMENSION ARE IN mm

CLIENT - RBCC
LOCATION - PUNE
PRODUCT - FLIP FLAP DOOR
DWG NO:-NIHVA/21-22/CLT/0378 | REV- 01
SCALE: NTS | SCALE:-- 1:1 | SHEET: 01 OF 01

Rev No.	Revision	Date	Revised By
1	Clear opening and clear height of the door has been changed	25/03/2022	Sujata