


DRAWING



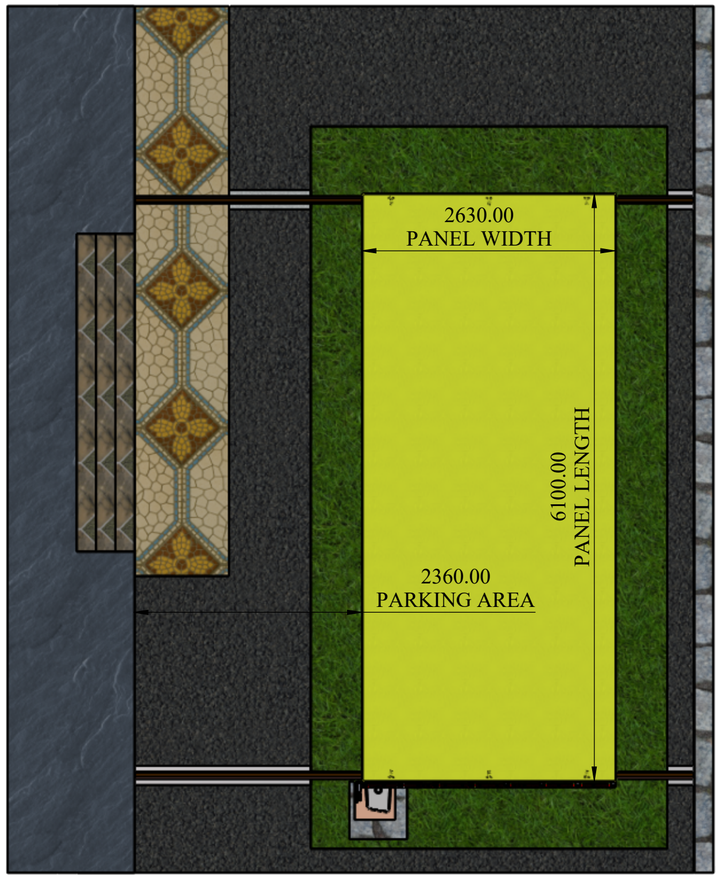


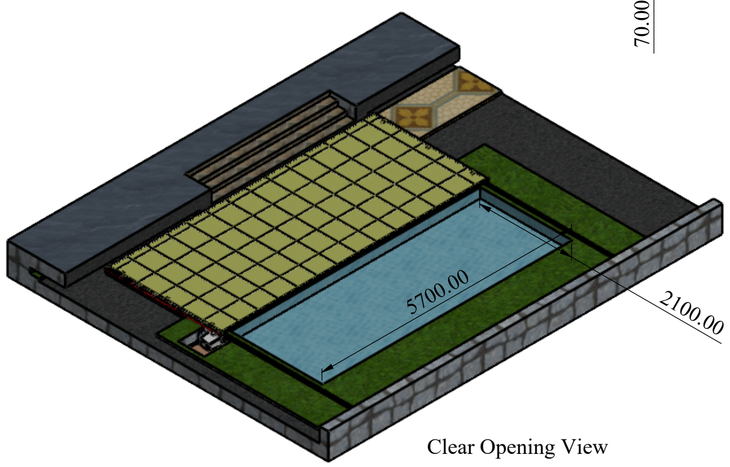


Clear Opening View

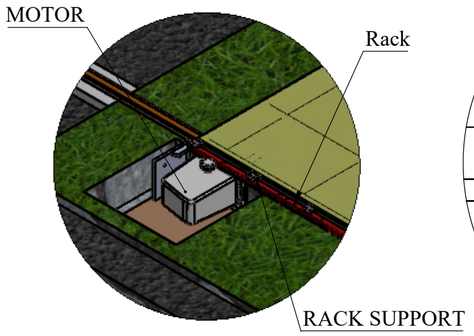


DETAIL A
SCALE 1 : 20

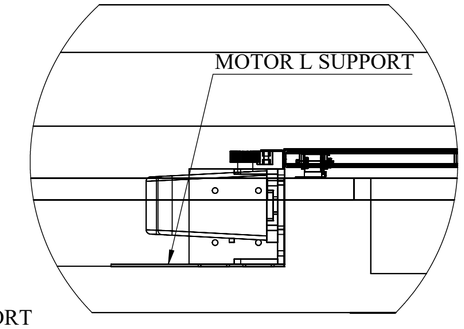

DETAIL B
SCALE 1 : 10

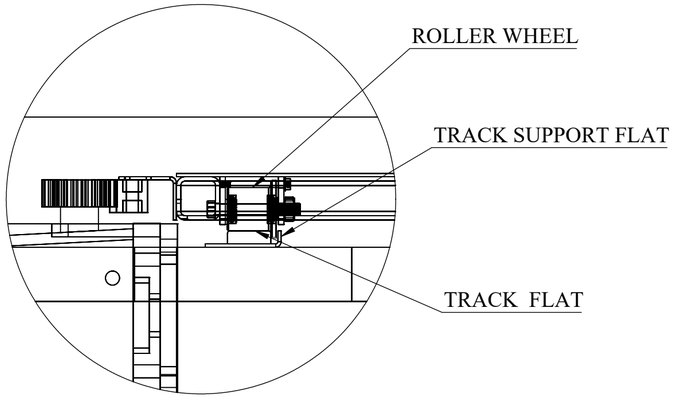

DETAIL C
SCALE 1 : 4

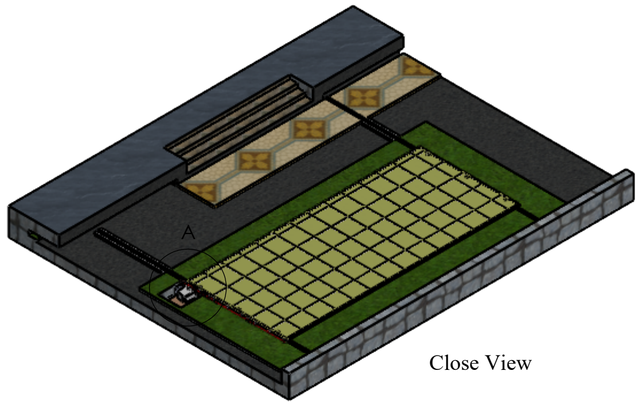

Close View

REV DESCRIPTION	DATE	REV NO
	29-07-2025	REV 00
1. Panel width Change & Track length change.	22-08-2025	REV 01


NOTE :


GA Drawing
Keep track clean before the panel movement.

SPECIAL INSTRUCTION'S :

TITLE - SWIMMING POOL ENCLOSER			
DWG NO - NTPL-000-PM-001			
NIHVA Technologies Pvt. Ltd.	NIHVA TECHNOLOGIES PVT.LTD.PUNE Website - www.nihva.com		
	NAME	SIGNATURE	DATE
DRAWN	V.W.		22-08-2025
CHK'D	P.M.		23-08-2025
APPV'D	V.T.		23-08-2025
PRODUCT - SWIMMING POOL DECK			
PROJECT NO - NTPL-000-PM	REVISION - 01		
SITE LOCATION - PUNE	WEIGHT -		
MATRIAL -	QTY - 1		
If any queries contact - design@nihva.com	PROJECTION METHOD:	SCALE :	
ALL DIMENSION ARE IN mm	A2	SHEET 1 OF 2	

DRAWING

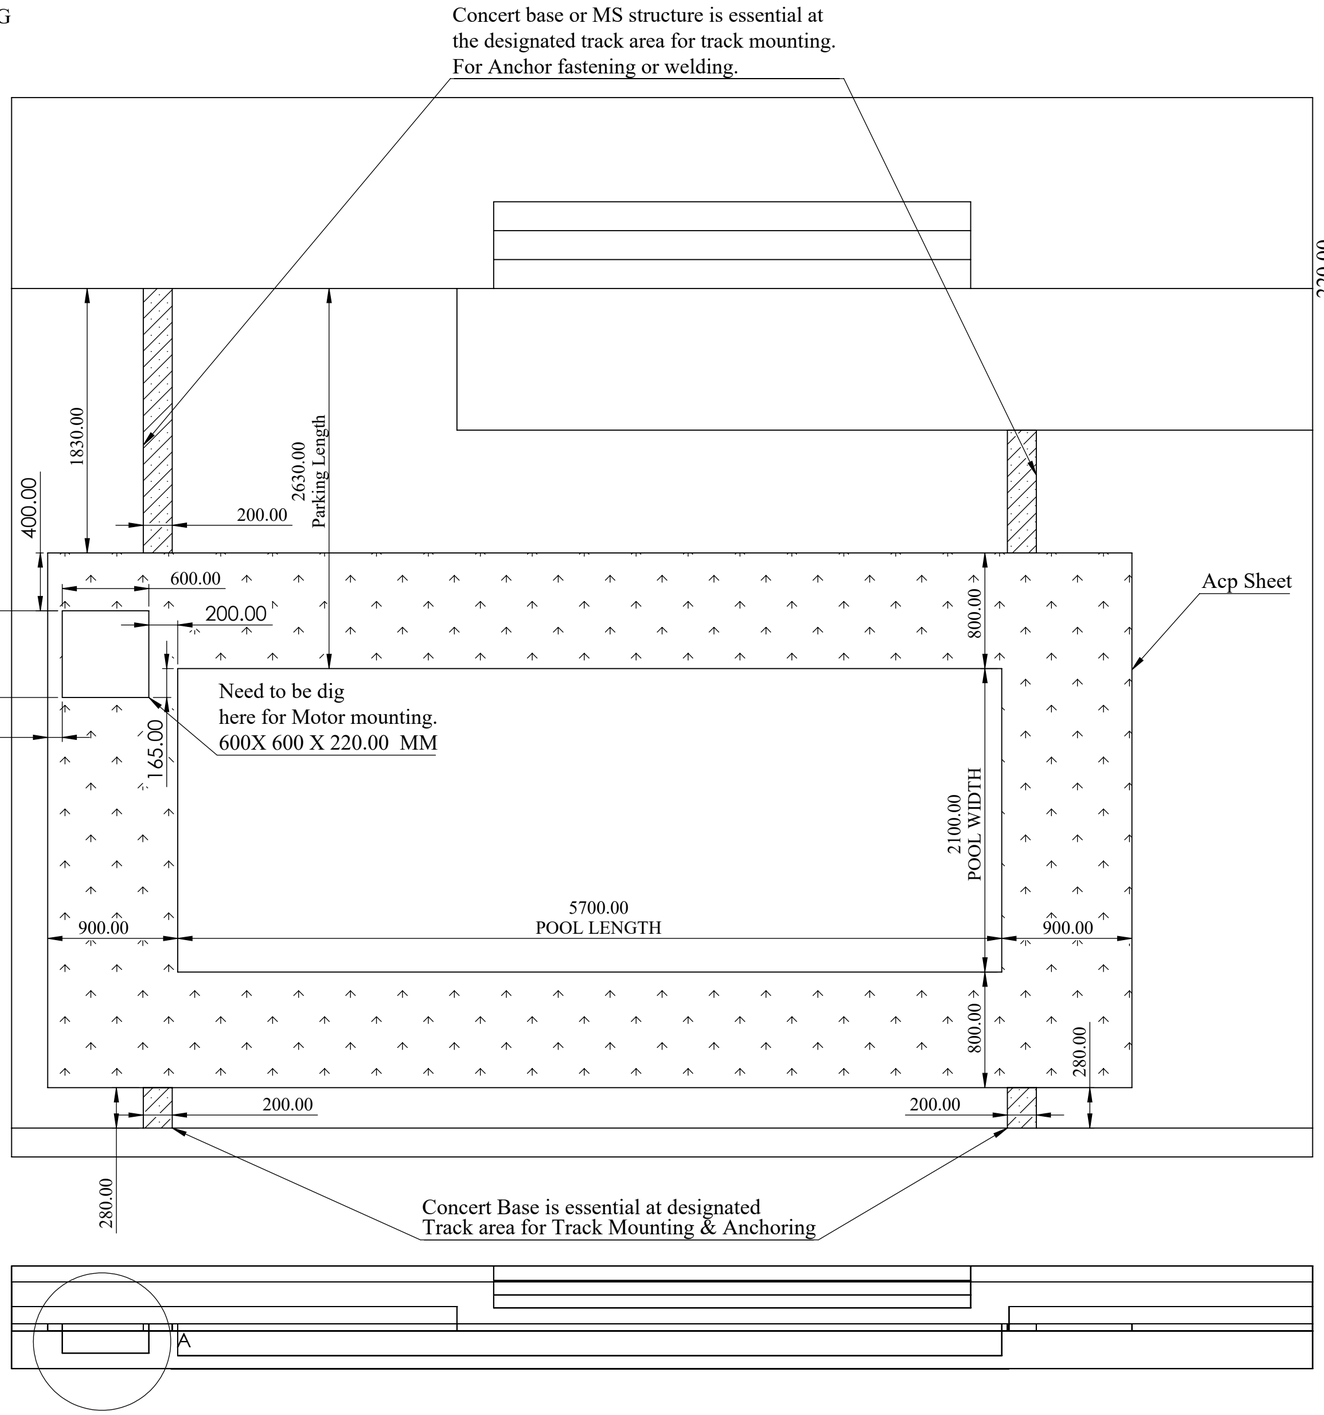

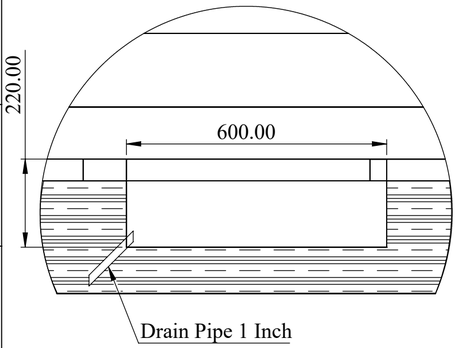

DETAIL A
SCALE 1 : 10

REV DESCRIPTION	DATE	REV NO
		REV 00
1.		

NOTE :

Civil Drawing
All civil work is under the end client scope.

SPECIAL INSTRUCTION'S :

	NAME	SIGNATURE	DATE
DRAWN	V.W.		22-08-2025
CHK'D	P.M.		23-08-2025
APPV'D	V.T.		23-08-2025

TITLE - SWIMMING POOL ENCLOSER
DWG NO - NTPL-000-PM-001

NIHVA Technologies Pvt. Ltd.
NIHVA TECHNOLOGIES PVT.LTD.PUNE
Website - www.nihva.com

PRODUCT - SWIMMING POOL DECK
PROJECT NO - NTPL-000-PM | REVISION - 00
SITE LOCATION - PUNE | WEIGHT -
MATRIAL - | QTY - 1
If any queries contact - design@nihva.com
PROJECTION METHOD: | SCALE :
ALL DIMENSION ARE IN mm | A2
SHEET 2 OF 2