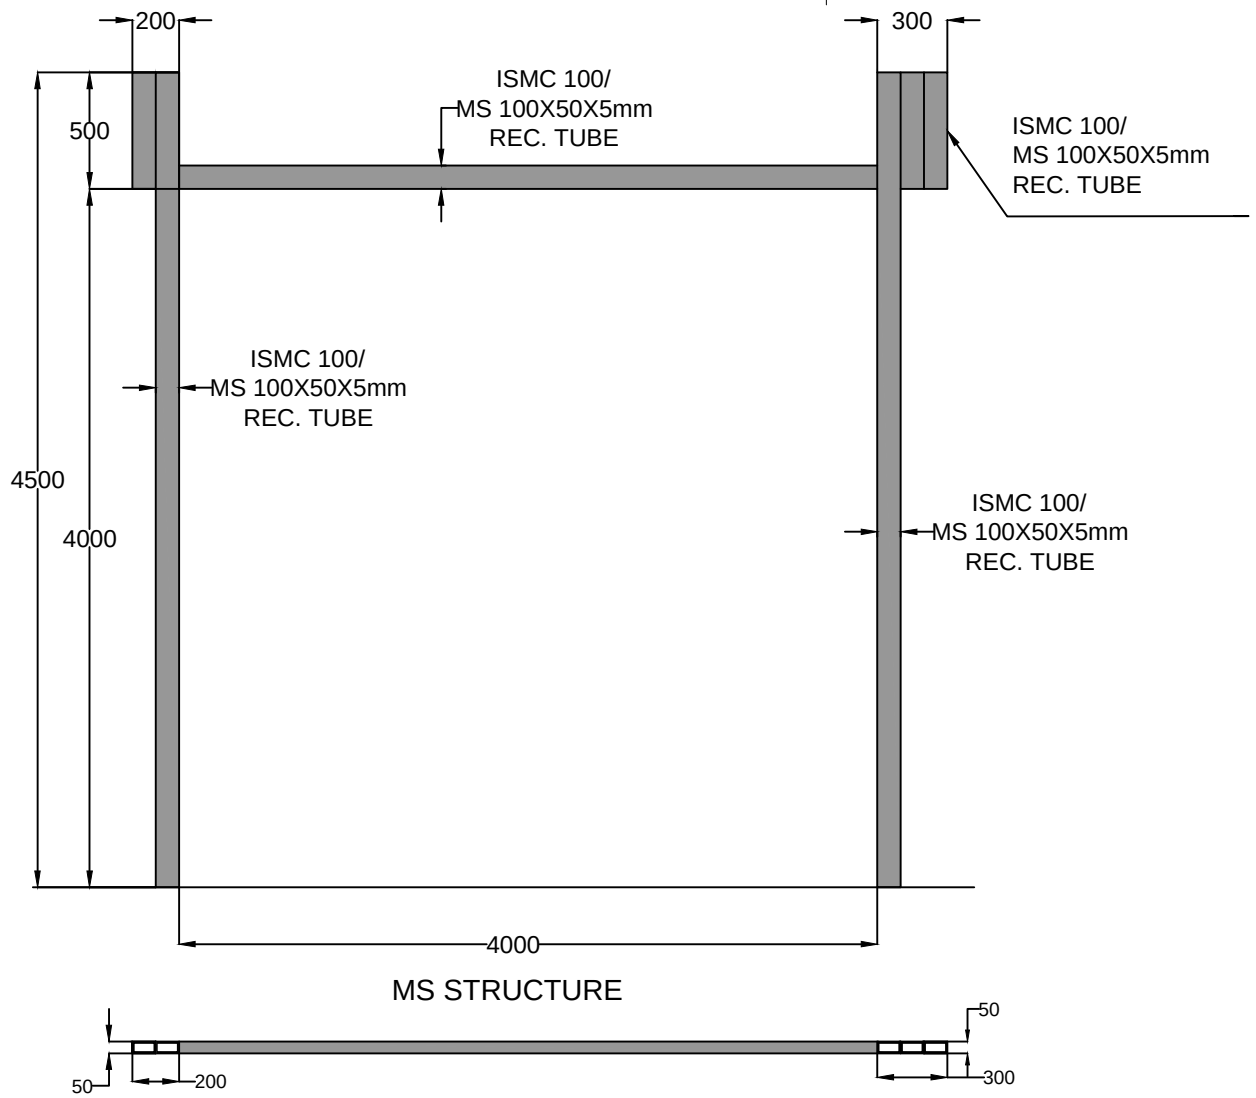


MS STRUCTURE

TOLERANCE - ±10mm

CLEAR WIDTH	CLEAR HEIGHT	QTY.
4000 mm	4000 mm	01NOS

This drawing & design is the property of NIHVA TECHNOLOGIES. Not to be sold or copied to any other concern.

TITLE
MOTORISED ROLLING SHUTTER STRUCTURE

NIHVA TECHNOLOGIES PVT. LTD.

NIHVA TECHNOLOGIES PVT. LTD. PUNE
Tel : 020 66304033
Email:- info@nihva.com
Website:- www.nihva.com

	NAME	SIGN	DATE
DRAWN	SURAJ		12-10-2018
CHECK	PRADEEP		12-10-2018
APPRD.	R.D		12-10-2018

CLIENT - VAICHAL CONSTRUCTIONS PVT. LTD
PROJECT -CNH
SITE LOCATION - CHAKAN
If any queries contact : design@nihva.com
DWG. NO. : NIHVA/18-19/0145
REV- 0
ALL DIMENSION ARE IN mm
SCALE: NTS
WT:
SHEET: 01 OF 01