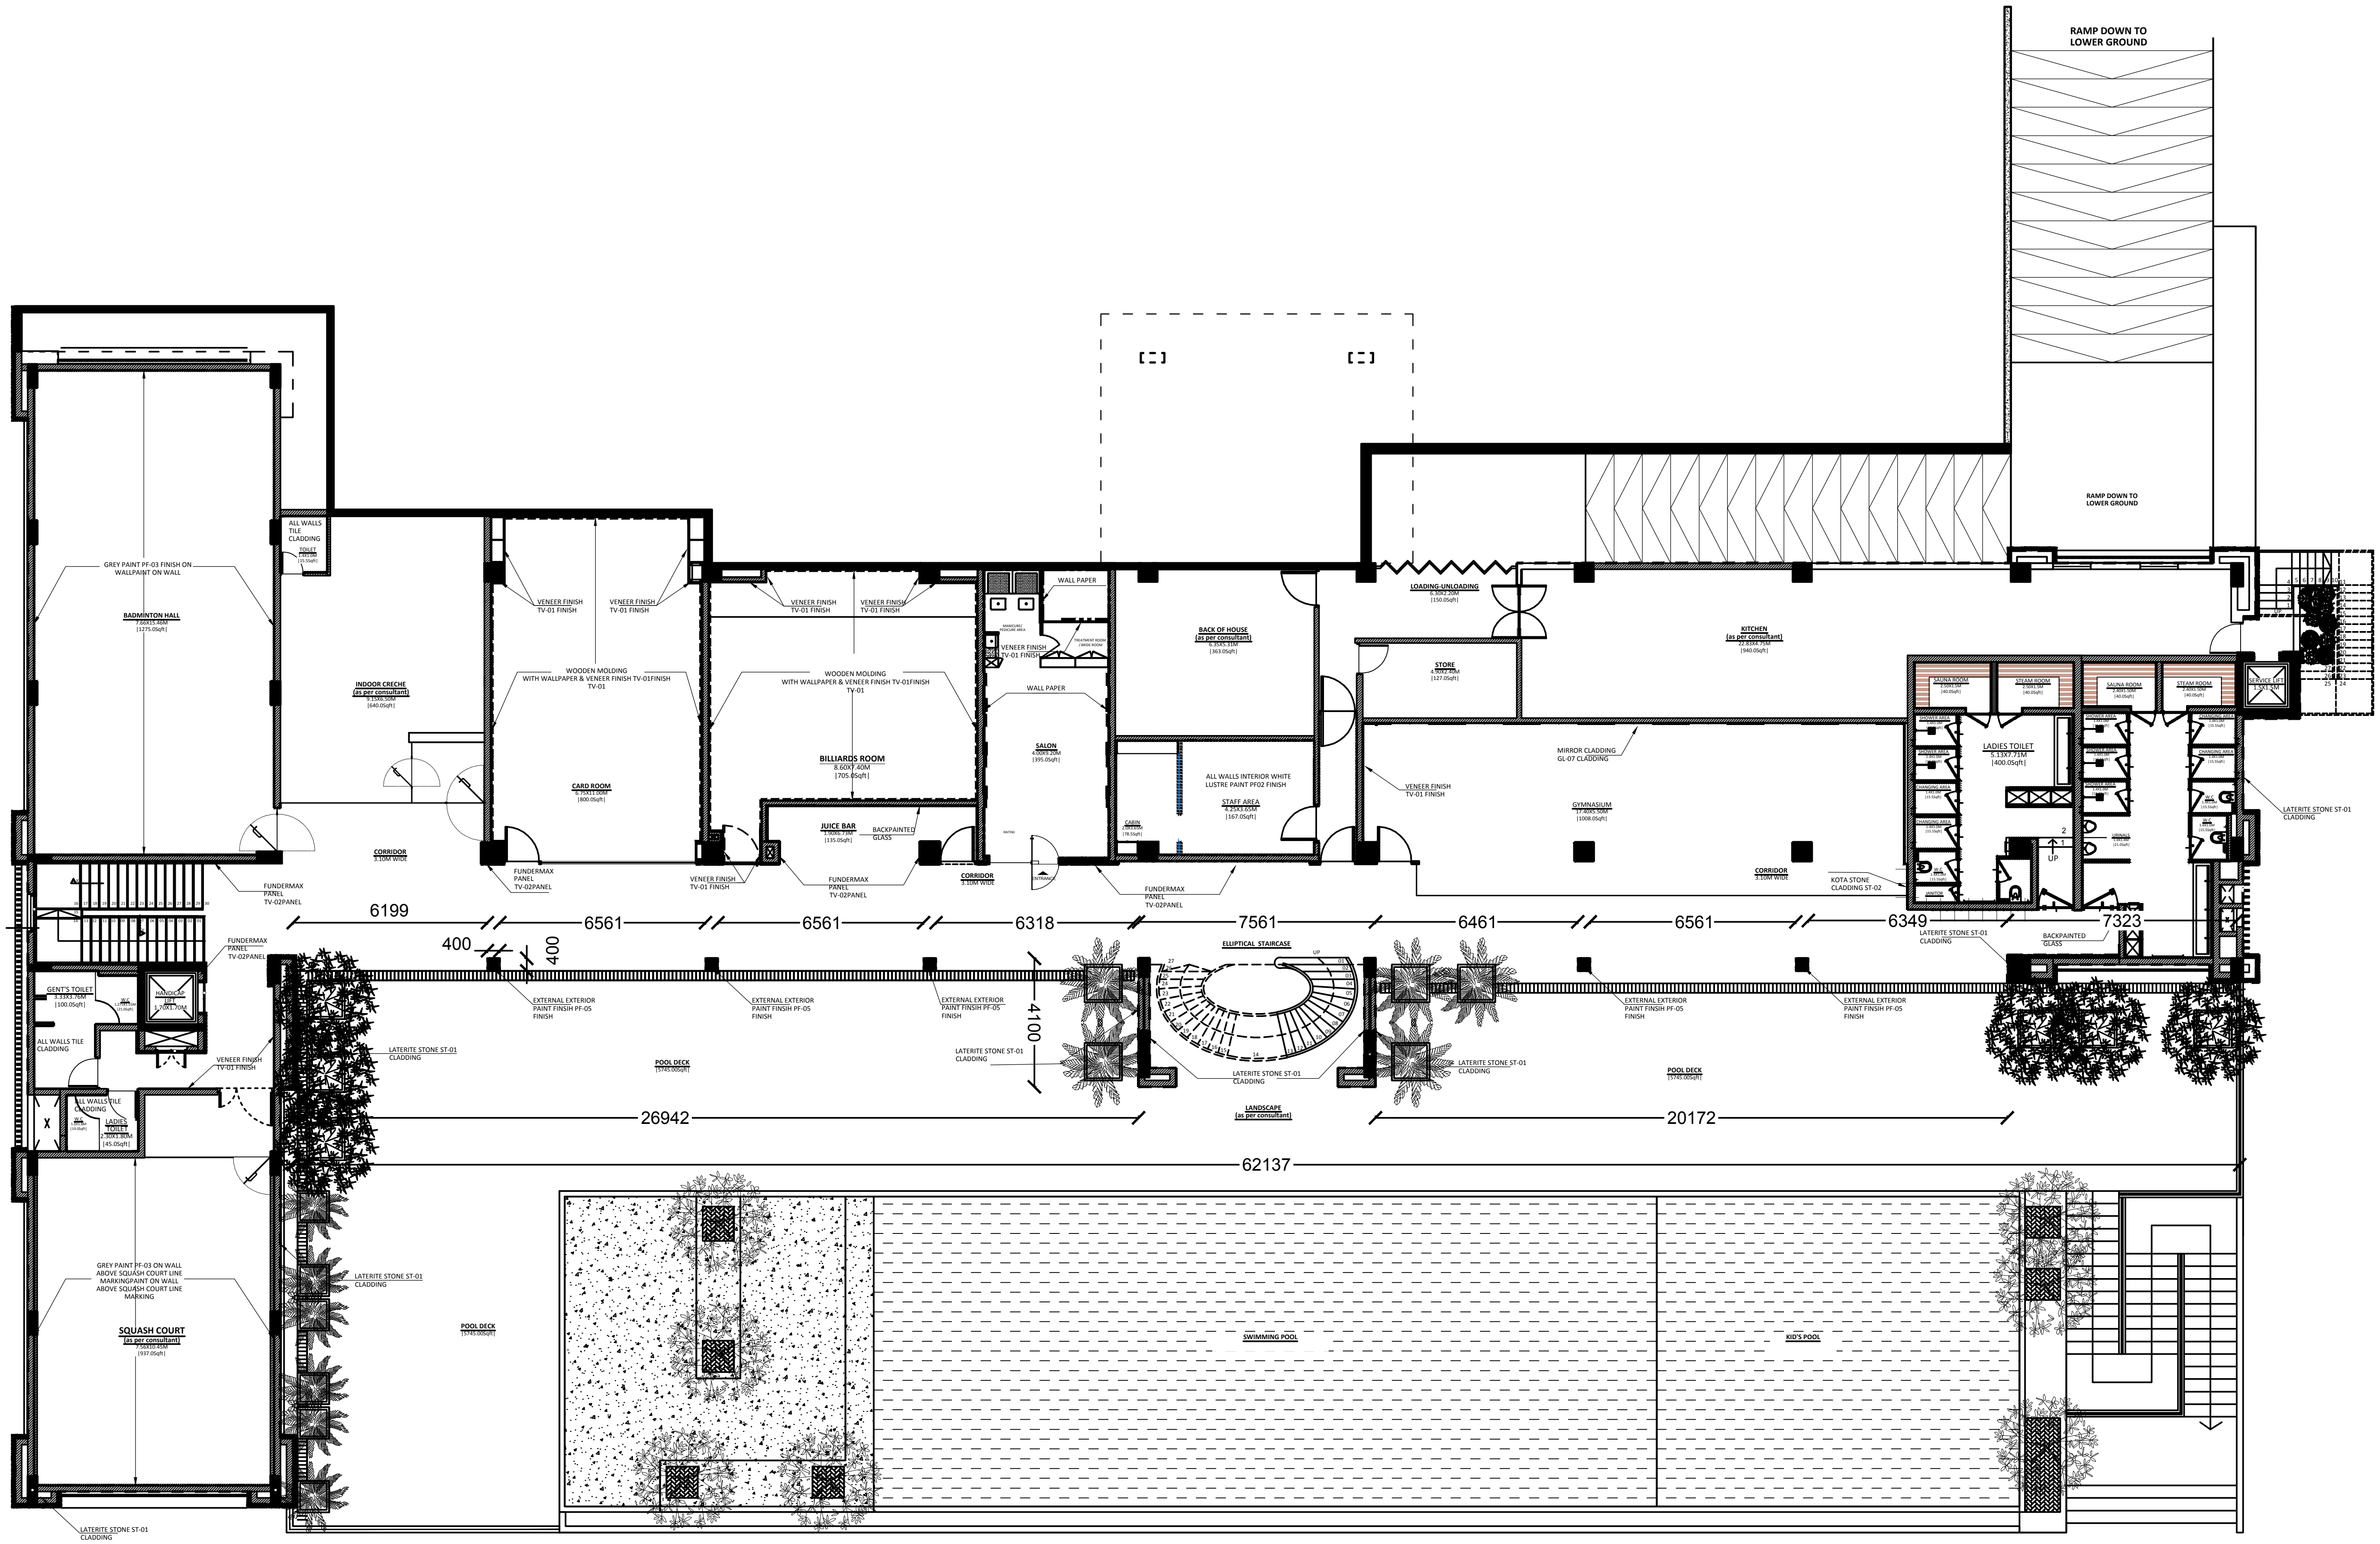
RAMP DOWN TO LOWER GROUND
RAMP DOWN TO LOWER GROUND
GREY PAINT PF-03 FINISH ON WALLPAINT ON WALL
BADMINTON HALL
7.66X15.46M
|1275.0Sqft|
ALL WALLS TILE CLADDING
TOILET
1.4X1.0M
|15.5Sqft|
INDOOR CRECHE
(as per consultant)
9.15X6.50M
|640.0Sqft|
VENEER FINISH TV-01 FINISH
VENEER FINISH TV-01 FINISH
WOODEN MOLDING WITH WALLPAPER & VENEER FINISH TV-01FINISH TV-01
CARD ROOM
6.75X11.00M
|800.0Sqft|
VENEER FINISH TV-01 FINISH
VENEER FINISH TV-01 FINISH
WOODEN MOLDING WITH WALLPAPER & VENEER FINISH TV-01FINISH TV-01
BILLIARDS ROOM
8.60X7.40M
|705.0Sqft|
JUICE BAR
1.90X6.73M
|135.0Sqft|
BACKPAINTED GLASS
WALL PAPER
MANICURE/ PEDICURE AREA
TREATMENT ROOM / BRIDE ROOM
VENEER FINISH TV-01 FINISH
WALL PAPER
SALON
4.00X9.20M
|395.0Sqft|
WAITING
ENTRANCE
BACK OF HOUSE
(as per consultant)
6.35X5.31M
|363.0Sqft|
ALL WALLS INTERIOR WHITE LUSTRE PAINT PF02 FINISH
STAFF AREA
4.25X3.65M
|167.0Sqft|
CABIN
2.0X3.65M
|78.5Sqft|
LOADING-UNLOADING
6.30X2.20M
|150.0Sqft|
STORE
4.90X2.40M
|127.0Sqft|
KITCHEN
(as per consultant)
22.83X4.75M
|940.0Sqft|
MIRROR CLADDING GL-07 CLADDING
VENEER FINISH TV-01 FINISH
GYMNASIUM
17.40X5.50M
|1008.0Sqft|
CORRIDOR
3.10M WIDE
KOTA STONE CLADDING ST-02
SAUNA ROOM
2.50X1.5M
|40.0Sqft|
STEAM ROOM
2.50X1.5M
|40.0Sqft|
SAUNA ROOM
2.40X1.50M
|40.0Sqft|
STEAM ROOM
2.40X1.50M
|40.0Sqft|
SERVICE LIFT
1.5X1.5M
SHOWER AREA
1.4X1.0M
CHANGING AREA
1.4X1.0M
|15.5Sqft|
W.C
1.4X1.0M
|15.5Sqft|
JANITOR
LADIES TOILET
5.13X7.71M
|400.0Sqft|
UP
URINALS
1.4X1.4M
|21.0Sqft|
LATERITE STONE ST-01 CLADDING
CORRIDOR
3.10M WIDE
FUNDERMAX PANEL TV-02PANEL
FUNDERMAX PANEL TV-02PANEL
VENEER FINISH TV-01 FINISH
FUNDERMAX PANEL TV-02PANEL
CORRIDOR
3.10M WIDE
FUNDERMAX PANEL TV-02PANEL
CORRIDOR
3.10M WIDE
6199
6561
6561
6318
7561
6461
6561
6349
7323
400
400
LATERITE STONE ST-01 CLADDING
BACKPAINTED GLASS
FUNDERMAX PANEL TV-02PANEL
GENT'S TOILET
3.33X3.76M
|100.0Sqft|
W.C
1.275X1.55M
|21.0Sqft|
HANDICAP LIFT
1.70X1.70M
ALL WALLS TILE CLADDING
VENEER FINISH TV-01 FINISH
ALL WALLS TILE CLADDING
W.C
1.0X1.8M
|19.0Sqft|
LADIES TOILET
2.30X1.80M
|45.0Sqft|
EXTERNAL EXTERIOR PAINT FINSIH PF-05 FINISH
EXTERNAL EXTERIOR PAINT FINSIH PF-05 FINISH
EXTERNAL EXTERIOR PAINT FINSIH PF-05 FINISH
LATERITE STONE ST-01 CLADDING
ELLIPTICAL STAIRCASE
UP
4100
LATERITE STONE ST-01 CLADDING
LATERITE STONE ST-01 CLADDING
LATERITE STONE ST-01 CLADDING
EXTERNAL EXTERIOR PAINT FINSIH PF-05 FINISH
EXTERNAL EXTERIOR PAINT FINSIH PF-05 FINISH
POOL DECK
|5745.00Sqft|
POOL DECK
|5745.00Sqft|
LANDSCAPE
(as per consultant)
26942
20172
62137
GREY PAINT PF-03 ON WALL ABOVE SQUASH COURT LINE MARKINGPAINT ON WALL ABOVE SQUASH COURT LINE MARKING
SQUASH COURT
(as per consultant)
7.56X10.45M
|937.0Sqft|
LATERITE STONE ST-01 CLADDING
POOL DECK
|5745.00Sqft|
SWIMMING POOL
KID'S POOL
LATERITE STONE ST-01 CLADDING