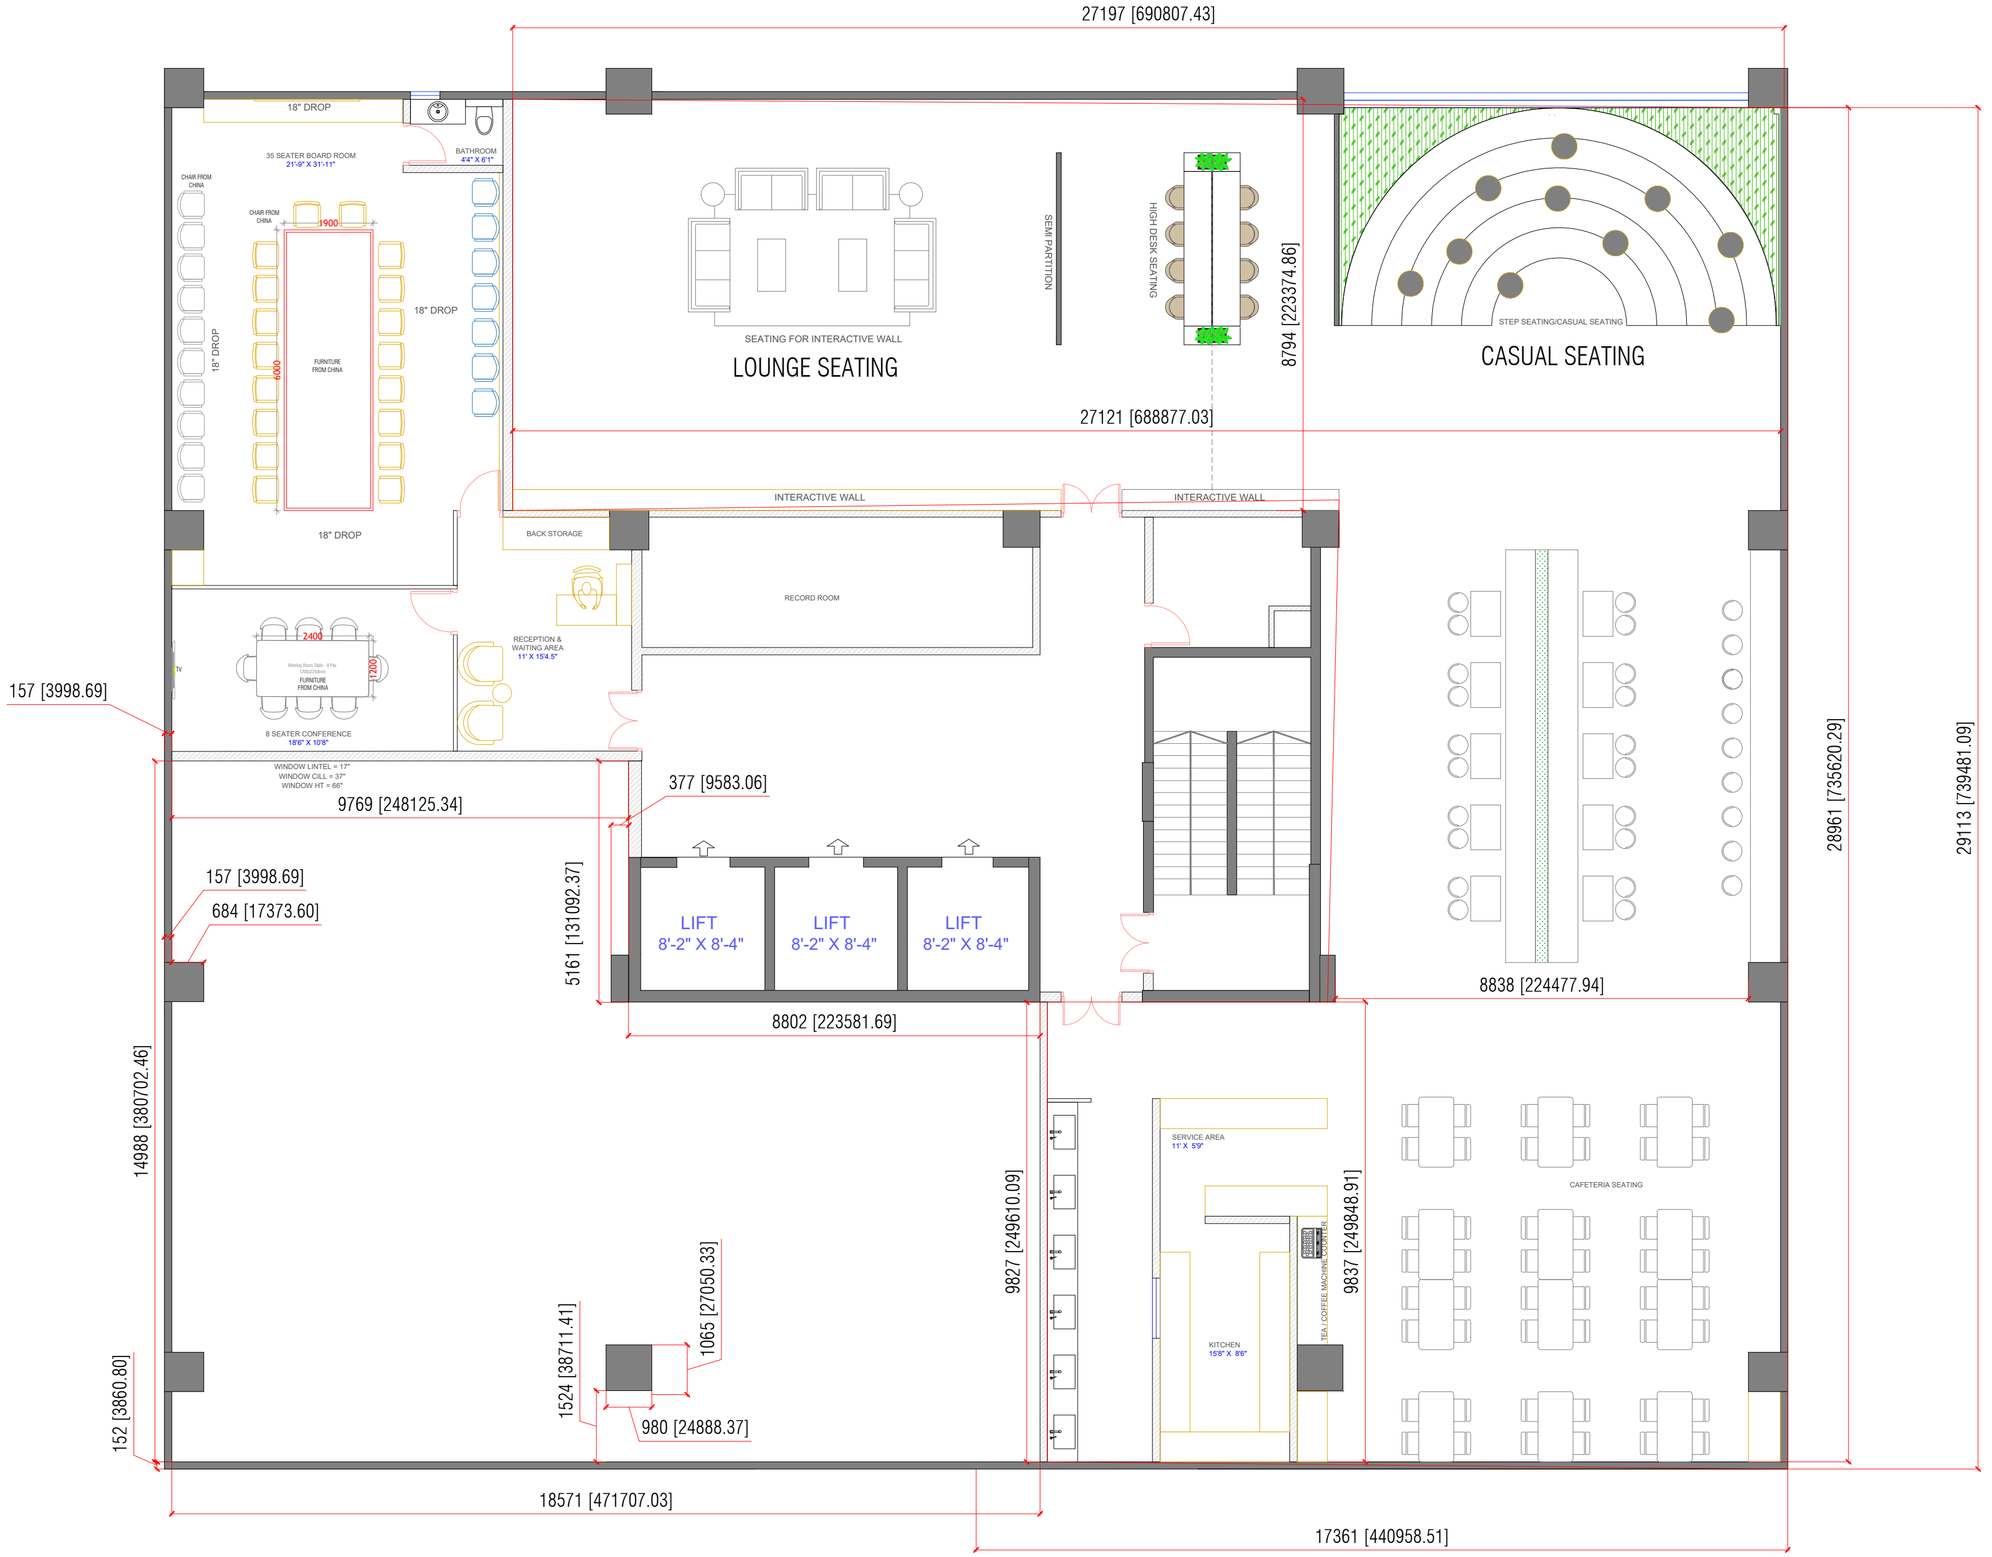

27197 [690807.43]
18" DROP
35 SEATER BOARD ROOM
21'-9" X 31'-11"
BATHROOM
4'4" X 6'1"
CHAIR FROM CHINA
CHAIR FROM CHINA
1900
18" DROP
18" DROP
FURNITURE FROM CHINA
6000
18" DROP
SEATING FOR INTERACTIVE WALL
LOUNGE SEATING
SEMI PARTITION
HIGH DESK SEATING
8794 [223374.86]
STEP SEATING/CASUAL SEATING
CASUAL SEATING
27121 [688877.03]
INTERACTIVE WALL
INTERACTIVE WALL
BACK STORAGE
RECORD ROOM
RECEPTION & WAITING AREA
11' X 15'4.5"
2400
7200
FURNITURE FROM CHINA
8 SEATER CONFERENCE
18'6" X 10'8"
157 [3998.69]
WINDOW LINTEL = 17"
WINDOW CILL = 37"
WINDOW HT = 66"
9769 [248125.34]
377 [9583.06]
157 [3998.69]
684 [17373.60]
5161 [131092.37]
LIFT
8'-2" X 8'-4"
LIFT
8'-2" X 8'-4"
LIFT
8'-2" X 8'-4"
8802 [223581.69]
8838 [224477.94]
14988 [380702.46]
SERVICE AREA
11' X 5'9"
CAFETERIA SEATING
KITCHEN
15'8" X 8'6"
TEA / COFFEE MACHINE
9827 [249610.09]
9837 [249848.91]
1065 [27050.33]
1524 [38711.41]
980 [24888.37]
152 [3860.80]
18571 [471707.03]
17361 [440958.51]
28961 [735620.29]
29113 [739481.09]