
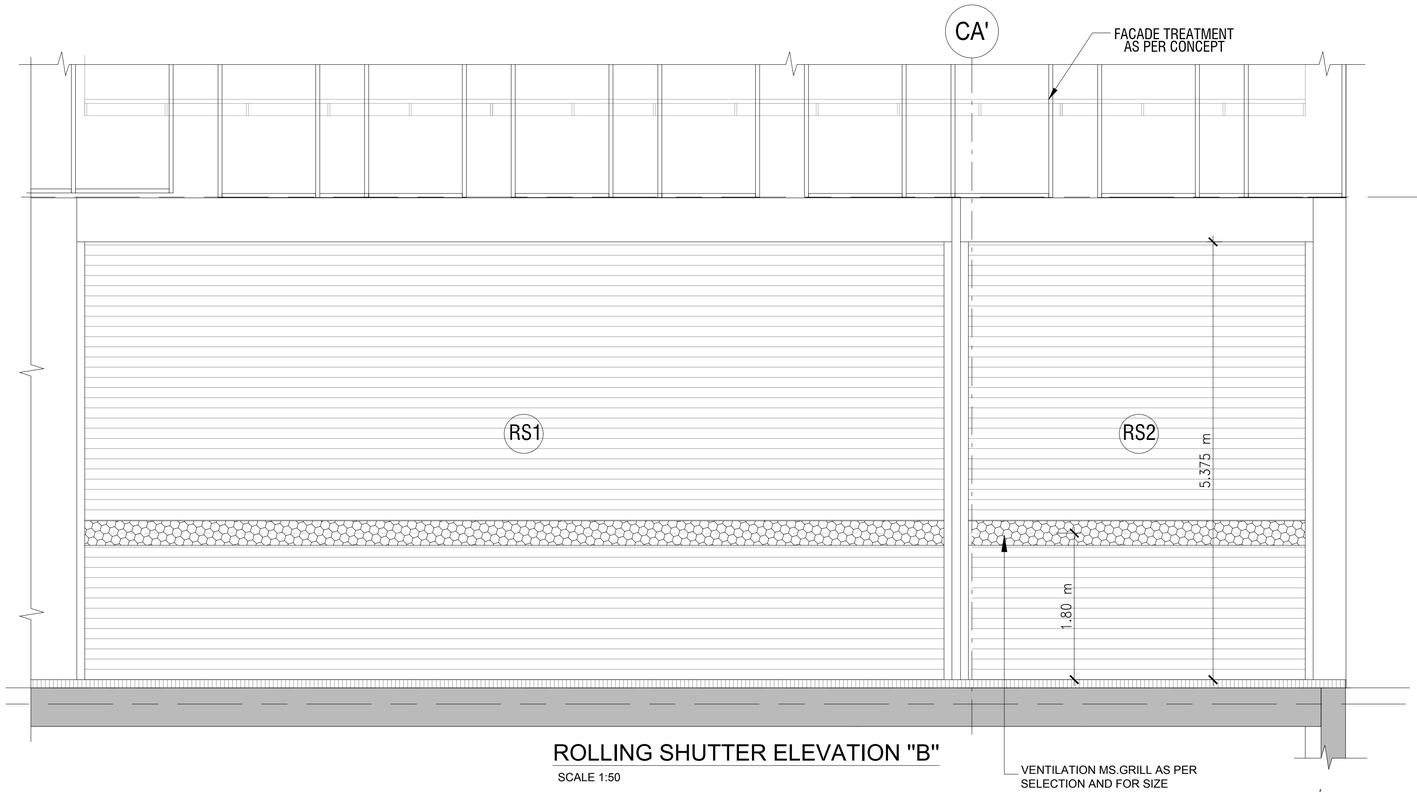



ROLLING SHUTTER ELEVATION "B"

SCALE 1:50

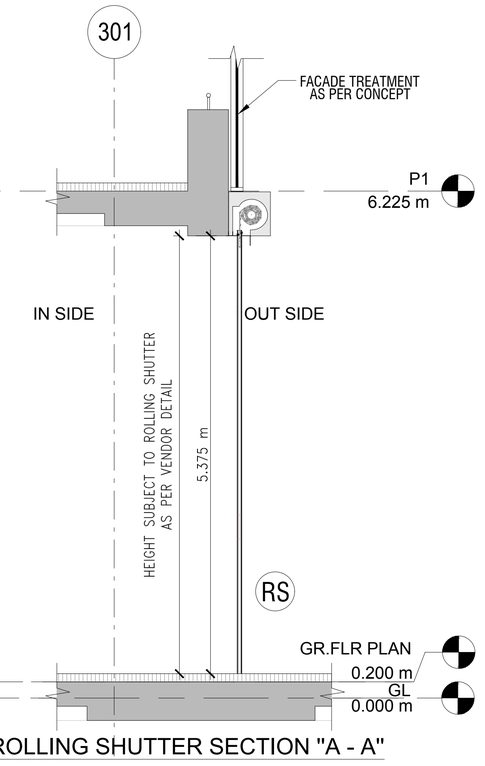

ROLLING SHUTTER SECTION "A - A"

SCALE 1:50

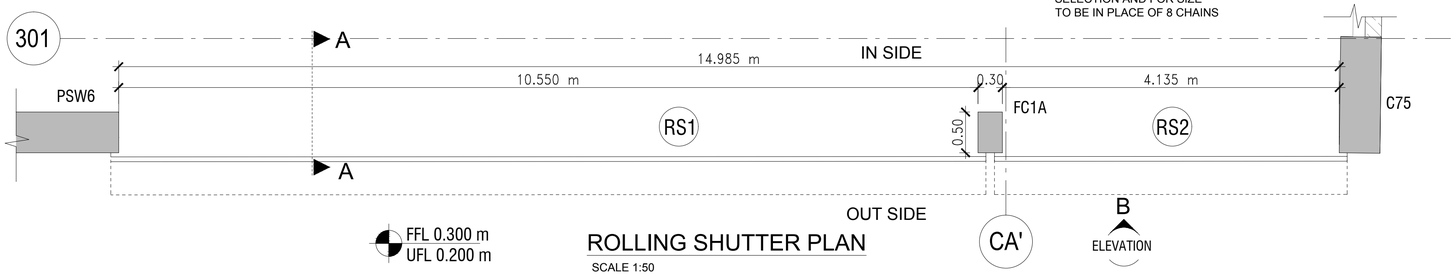


ROLLING SHUTTER PLAN

SCALE 1:50

RS	DESCRIPTION:	ROLLING SHUTTER
	LOCATION:	GROUND PPL ENTRY
NOTE - ROLLING SHUTTER AND BOX AS PER VENDOR DETAIL		

Rolling Shutter Opening Schedule

Type Mark	Height	Width	Count
RS1	5.375 m	10.550 m	1
RS2	5.375 m	4.135 m	1

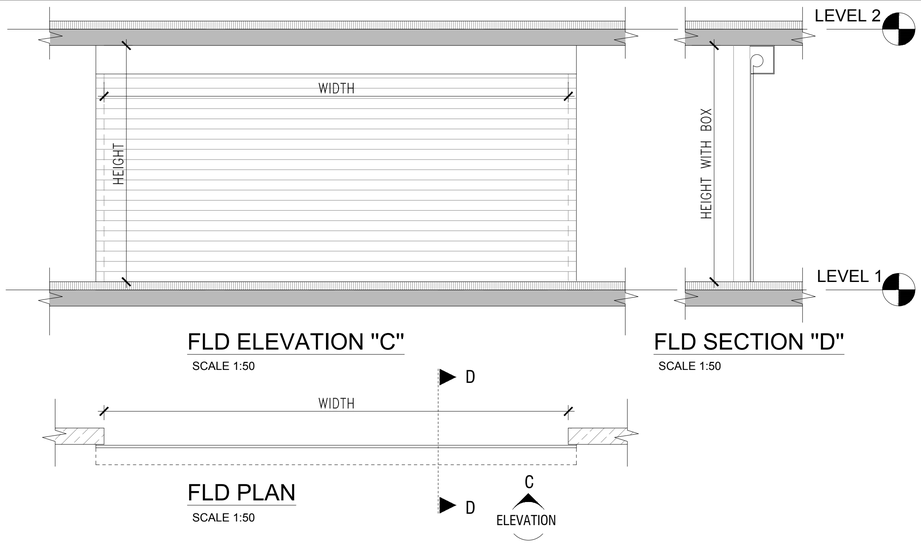

FLD ELEVATION "C"

SCALE 1:50

FLD SECTION "D"

SCALE 1:50

FLD PLAN

SCALE 1:50

FUSE LINK DOOR SCHEDULE

Door Opening Schedule (Basement 1)

Type Mark	Height (FLD with box of size 300x350)	Width	Count
FLD4	4.450 m	7.500 m	1
FLD 1	4.225 m	7.500 m	1
FLD 2	4.450 m	6.000 m	1
Grand total: 3			3

Door Opening Schedule (Basement 2)

Type Mark	Height (FLD with box of size 300x350)	Width	Count
FLD3	2.900 m	5.500 m	2
FLD5	2.900 m	5.400 m	2
FLD6	2.850 m	6.000 m	1
Grand total: 5			5

Door Opening Schedule (Basement 3)

Type Mark	Height (FLD with box of size 300x350)	Width	Count
FLD3	2.900 m	5.500 m	2
FLD5	2.900 m	5.400 m	2
FLD6	2.850 m	6.000 m	1
Grand total: 5			5

NOTE:
A mechanical fusible link is a device consisting of two strips of metal soldered together with a fusible alloy that is designed to melt at a specific temperature, thus allowing the two pieces to separate. Mechanical fusible links come in a variety of designs and different temperature ratings
AS PER VENDOR DETAIL.

NOTES AND INSTRUCTIONS

1. THIS DRAWING IS ISSUED IN TERMS OF M.O.U DEFINING SCOPE AND RESPONSIBILITIES OF CONCERN PARTIES .OUR LIABILITY SHALL REMAIN LIMITED AS PROVIDED IN M.O.U.
2. THIS DRAWING TO BE READ ALONG WITH STRUCTURAL AND MEP CONSULTANT'S DRAWING RESPECTIVELY.
3. IN CASE OF ANY DOUBT/DISCREPANCY DIMENSIONS SHOWN AND THOSE AVAILABLE ON SITE, THE CONTRACTOR SHOULD CLARIFY BEFORE EXECUTION.
4. THIS DRAWING TO BE READ IN CONJUCTION WITH MEP CONSULTANTS DRAWING

NO	DESCRIPTION	DATE
R0	RELEASED FOR CONSTRUCTION	03/08/2018
R1	FUSE LINK DOOR (FLD) SIZE REVISED	04/02/2019
R2	FLOATING COLUMN (FC1A) ADDED AND ROLLING SHUTTER WIDTH REVISED	10/04/2019

REVISIONS

PROJECT
SALSETTE 27

CLIENT
M/S GOODTIME REAL ESTATE DEVELOPEMENT PVT.LTD.MUMBAI.

PROJECT ARCHITECT
SAMIR CHINAI ARCHITECTS
Neelam Center,B-Wing,401-404,4th Floor,
Hind Cycle Road,Worli,Mumbai-400030
TEL. 22 6231 1000

DESIGN ARCHITECT
HBD
8 JALAN KILANG TIMOR,#02-01,KEWALRAM HOUSE,
SINGAPORE 159305

CIVIL & STRUCTURAL ENGINEER
STERLING
ENGINEERING CONSULTANCY SERVICES PVT. LTD.
QUEENS MANSION, PRESCOT ROAD, MUMBAI 400001.

MECHANICAL & ELECTRICAL ENGINEER
AECOM
UNIT NO.2,8th FLOOR TIMES SQUARE WING A ANDHERI KURLA ROAD,MAROL,ANDHERI (E),MUMBAI 400059

TITLE
ROLLING SHUTTER DETAIL
AND FUSE LINK DOOR (FLD) DETAILS

PROJECT ID	STAGE	DRAWING NUMBER	REVISION
SS	E	SS.ID.E.05.15	R2

DATE:	10/04/2019	SCALE:	1:50	RVT NO:	
APP BY:	NM	CHK BY:	NM	DRN BY:	PV
RVT REF:					

N

ISSUED FOR:
EXECUTION

THIS DRAWING AND THE DESIGN IT COVERS ARE THE PROPERTY OF SCA THEY ARE MERELY THE BORROWERS EXPRESS AGREEMENT THAT THEY WILL NOT BE REPRODUCED COPIED LOANED EXHIBITED NOR USED EXCEPT IN THE LIMITED WAY AND PRIVATE USE PERMITTED AND WRITTEN CONSENT GIVEN BY SCA TO THE BORROWER.