

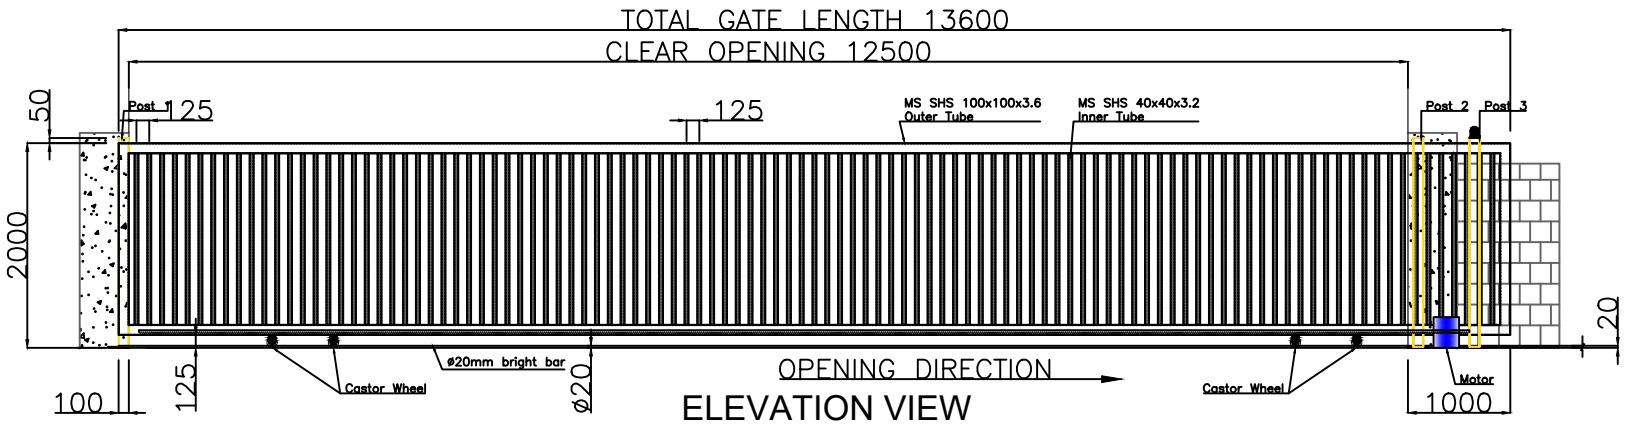



ELEVATION VIEW

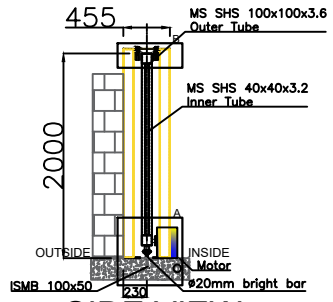


SIDE VIEW

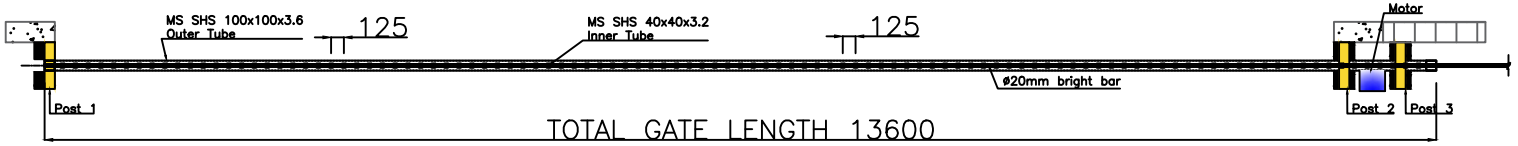

PLAN

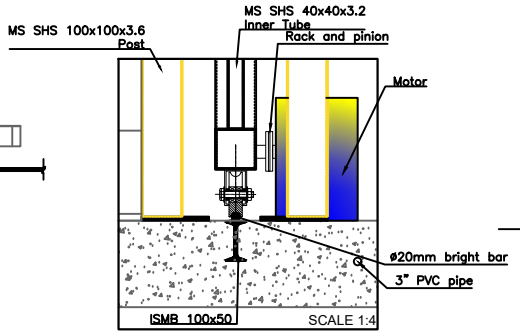

DETAIL A

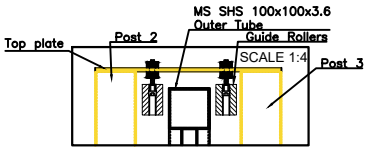

DETAIL B

Note-

1. All dimension are in mm.
2. All civil work is under client scope.
3. 3" PVC pipe in the foundation to be provided by client.
4. Power supply single phase 230v, 50hz.
5. Cable for power supply 2.5 sqmm 3 core
6. Cable for photocell - 1.5 sqmm 4 core

Technical Specs of Motorized Sliding Gate

1. Opening length - 12500mm
2. Gate Height - 2000mm
3. Parking length required - 13500mm
4. Outer tube size - MS SHS 100x100x3.6mm
5. Inner tube size - MS SHS 40x40x3.2mm
6. Pitch between tube - 125mm
7. Bottom Rail - Bright bar Ø20mm
8. Post size - MS SHS 100x100x3.6mm
9. Total leaf weight ≈1100 kg
10. Safety feature - Photocell and flashing light
11. Operation - Push button from side

This drawing & design is the property of NIHVA TECHNOLOGIES. Not to be sold or copied to any other concern.

TITLE
MOTORIZED SLIDING GATE

NIHVA
NIHVA TECHNOLOGIES PVT. LTD.

NIHVA TECHNOLOGIES PVT. LTD. PUNE
Tel : 020 66304033
Email:- info@nihva.com
Website:- www.nihva.com

	NAME	SIGN	DATE
DRAWN	G.J.		10.08.21
CHECK	A.K.		10.08.21
APPRD.	V.T.		10.08.21

If any queries contact : projectsautomation@nihva.com

ALL DIMENSION ARE IN mm

CLIENT -M/s FUJI SILVERTECH CONCRETE P. LTD.

LOCATION - AURANGABAD

PRODUCT - MOTORIZED SLIDING GATE

NIHVA\20-21\0198 | REV- A

SCALE: NTS | SHEET: 01 OF 01