

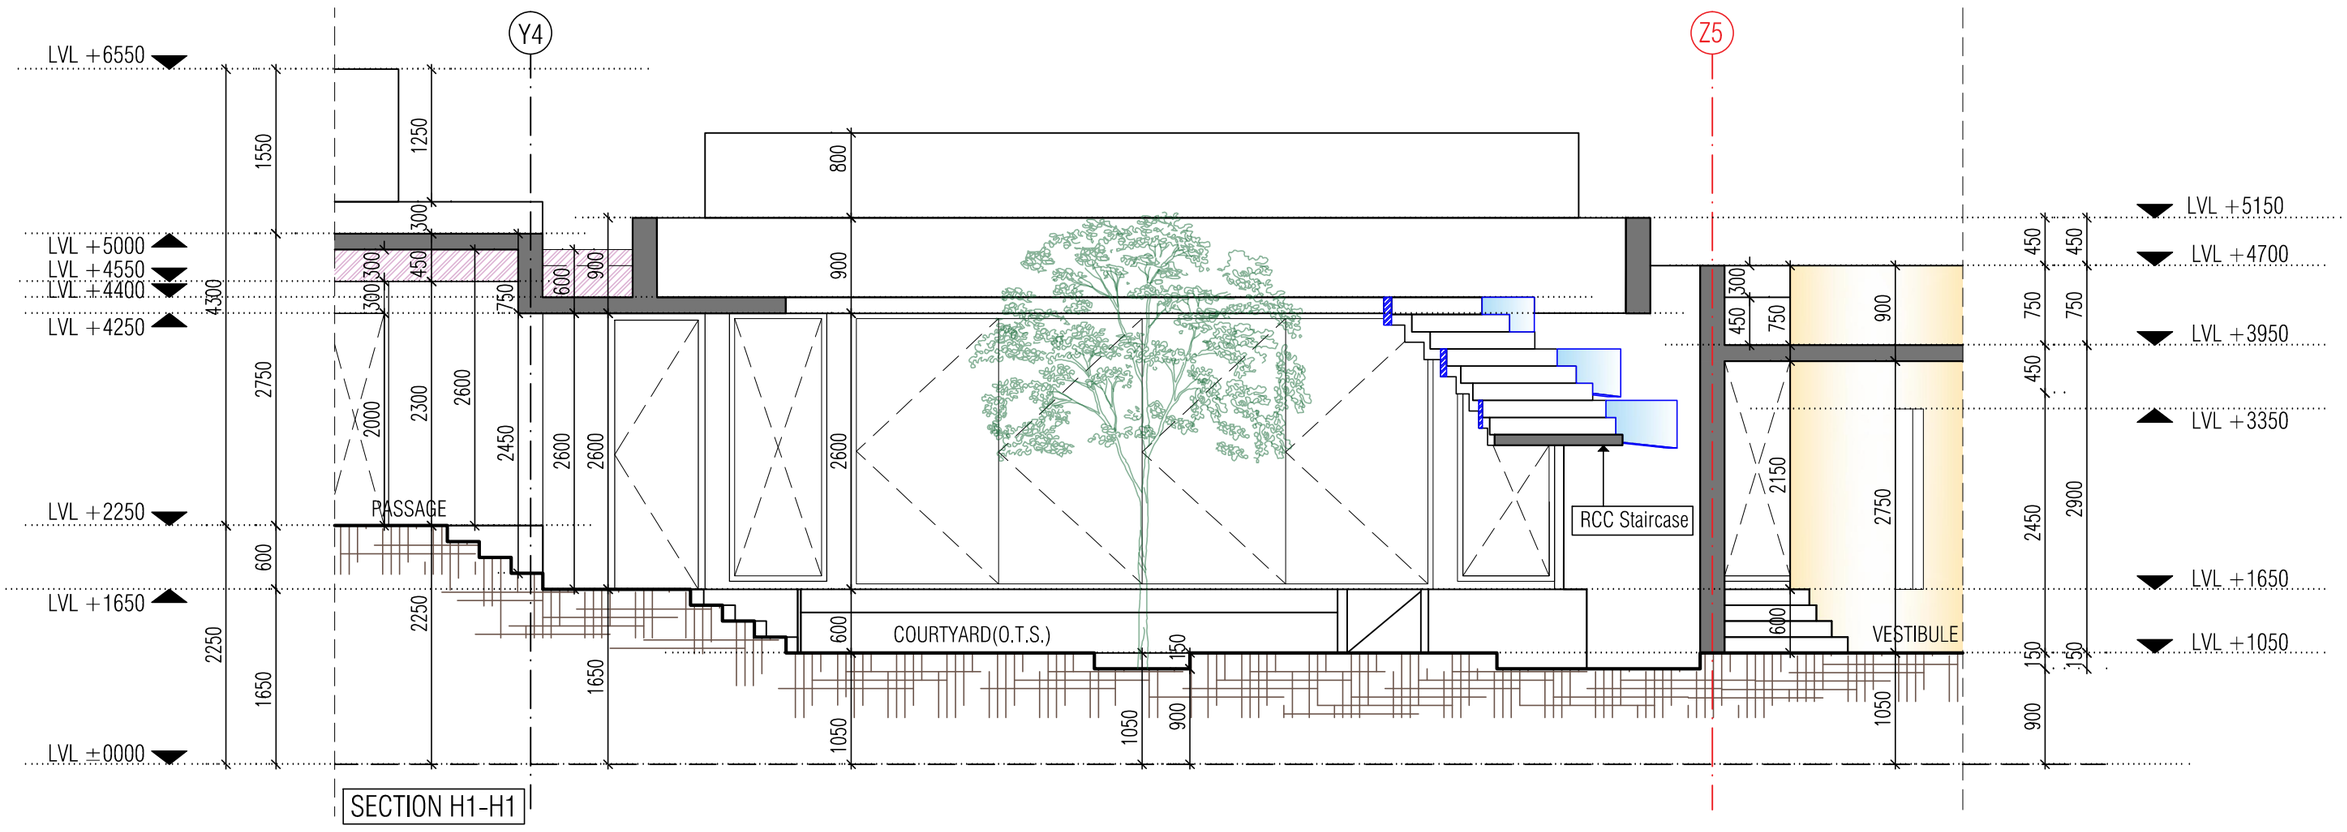



SECTION H1-H1

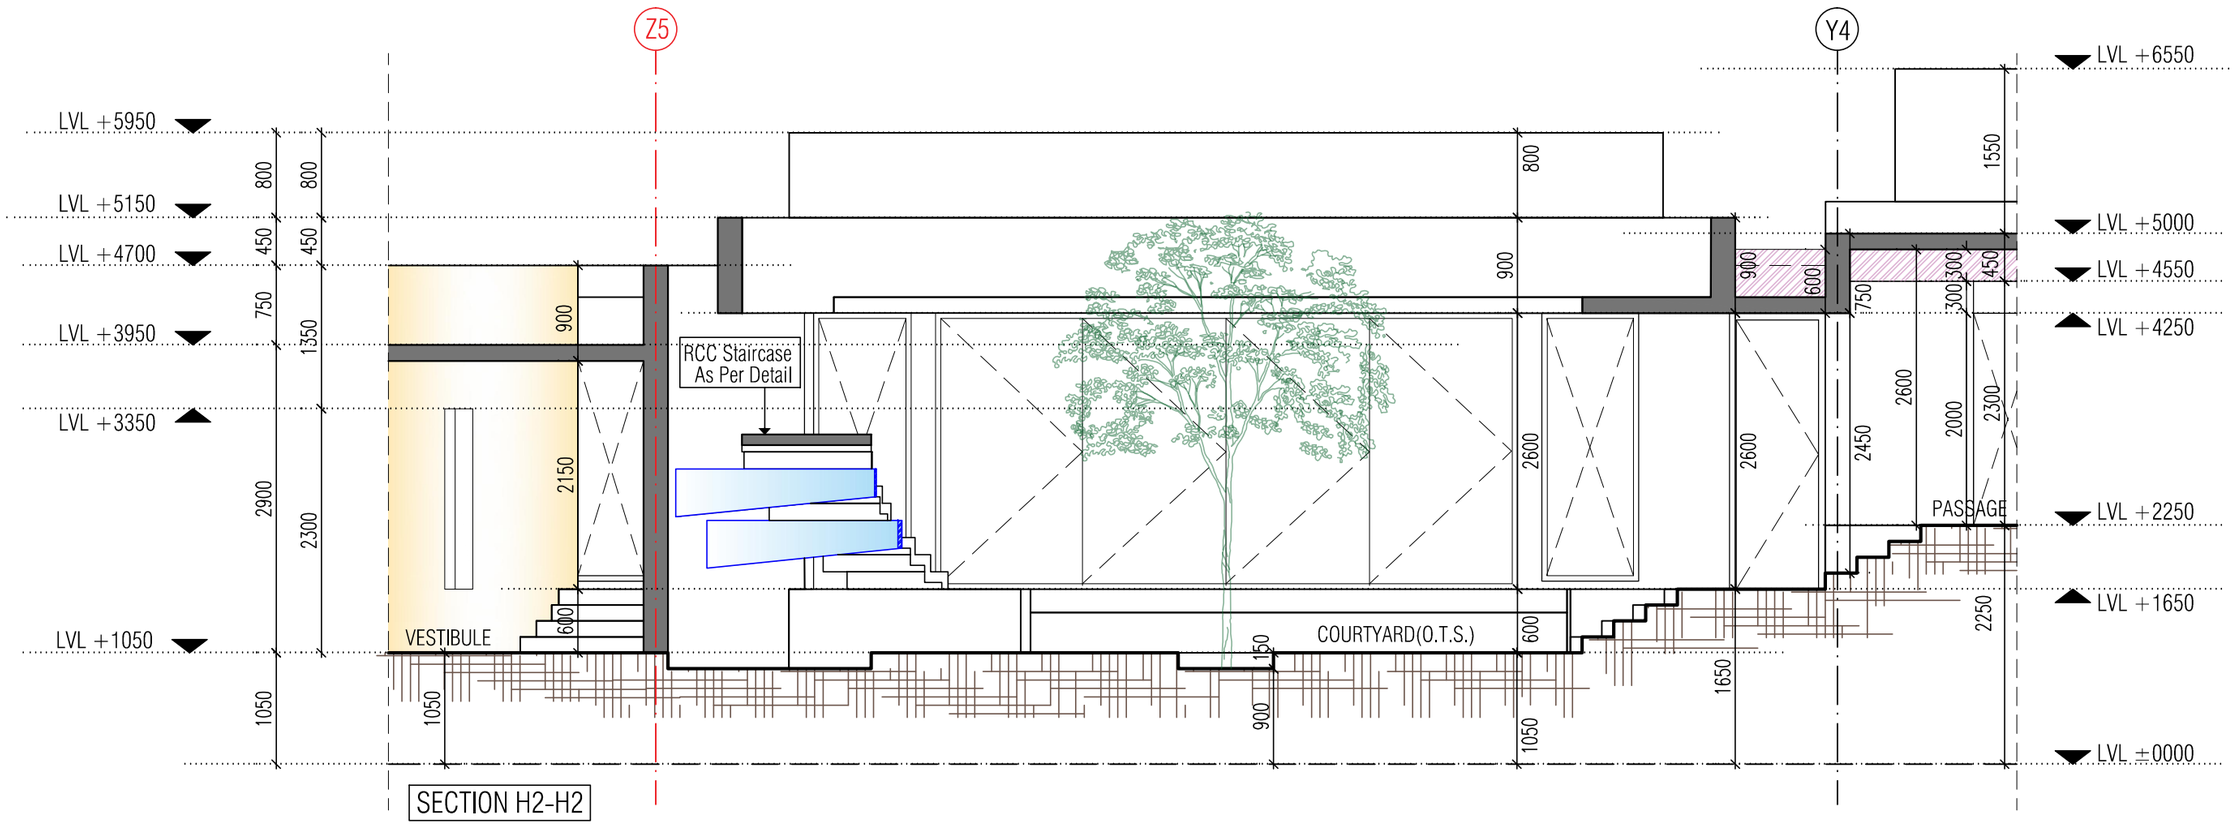

SECTION H2-H2

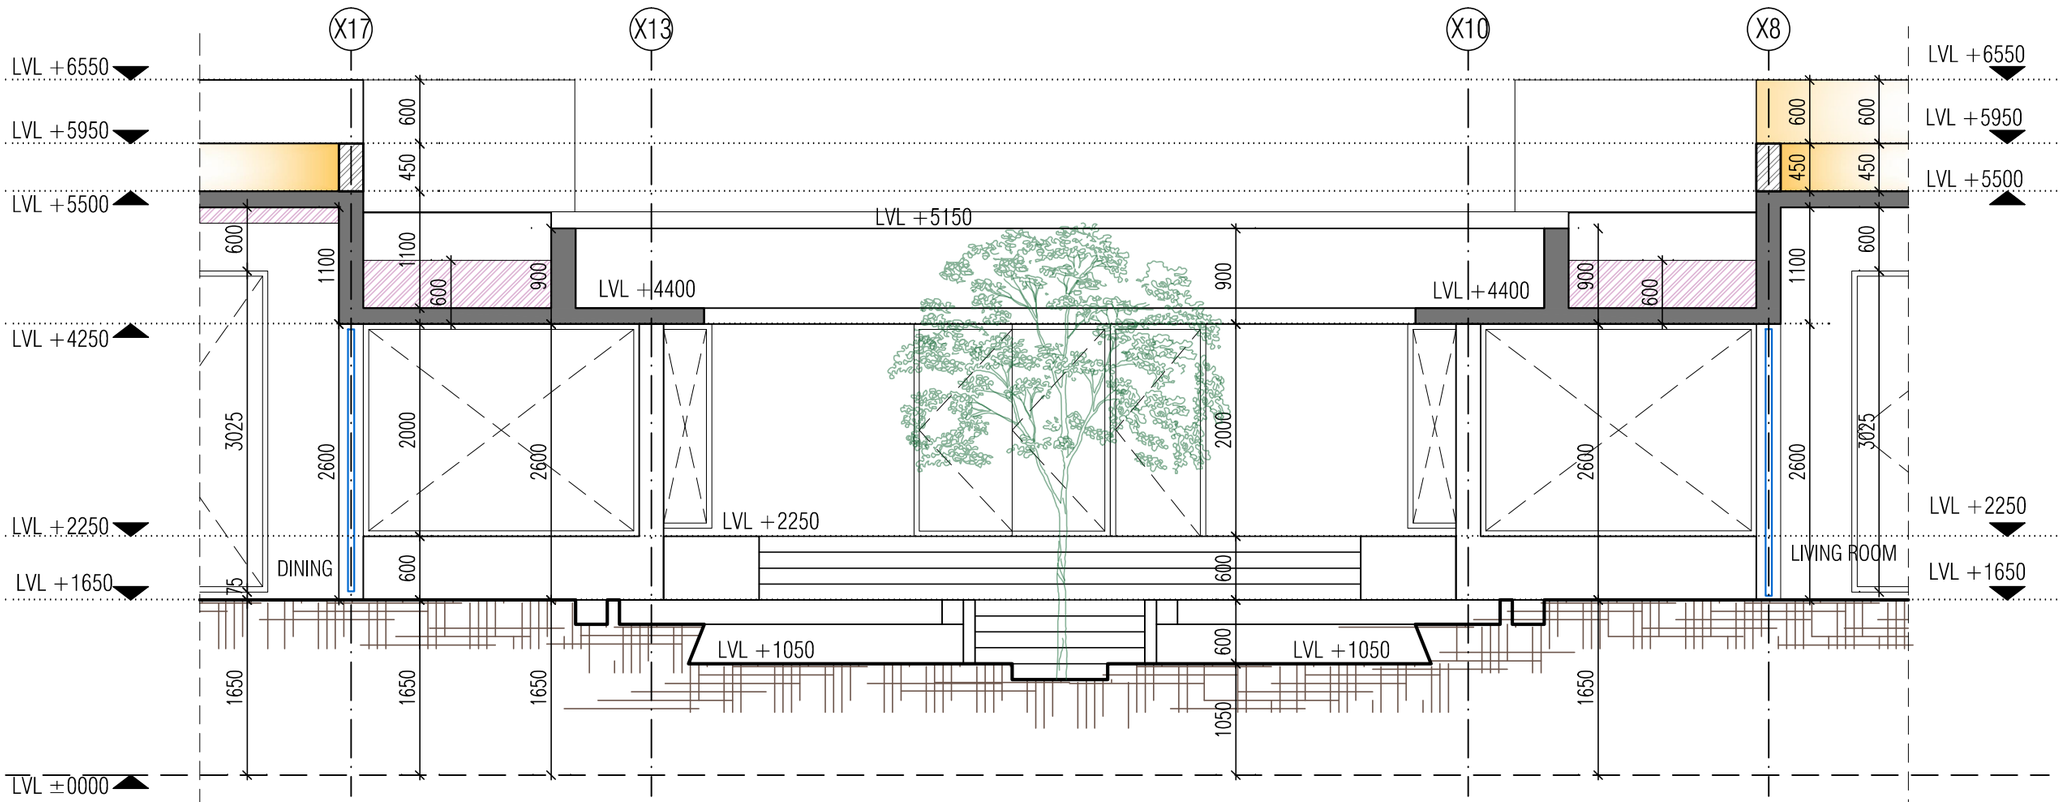

SECTION R1-R1

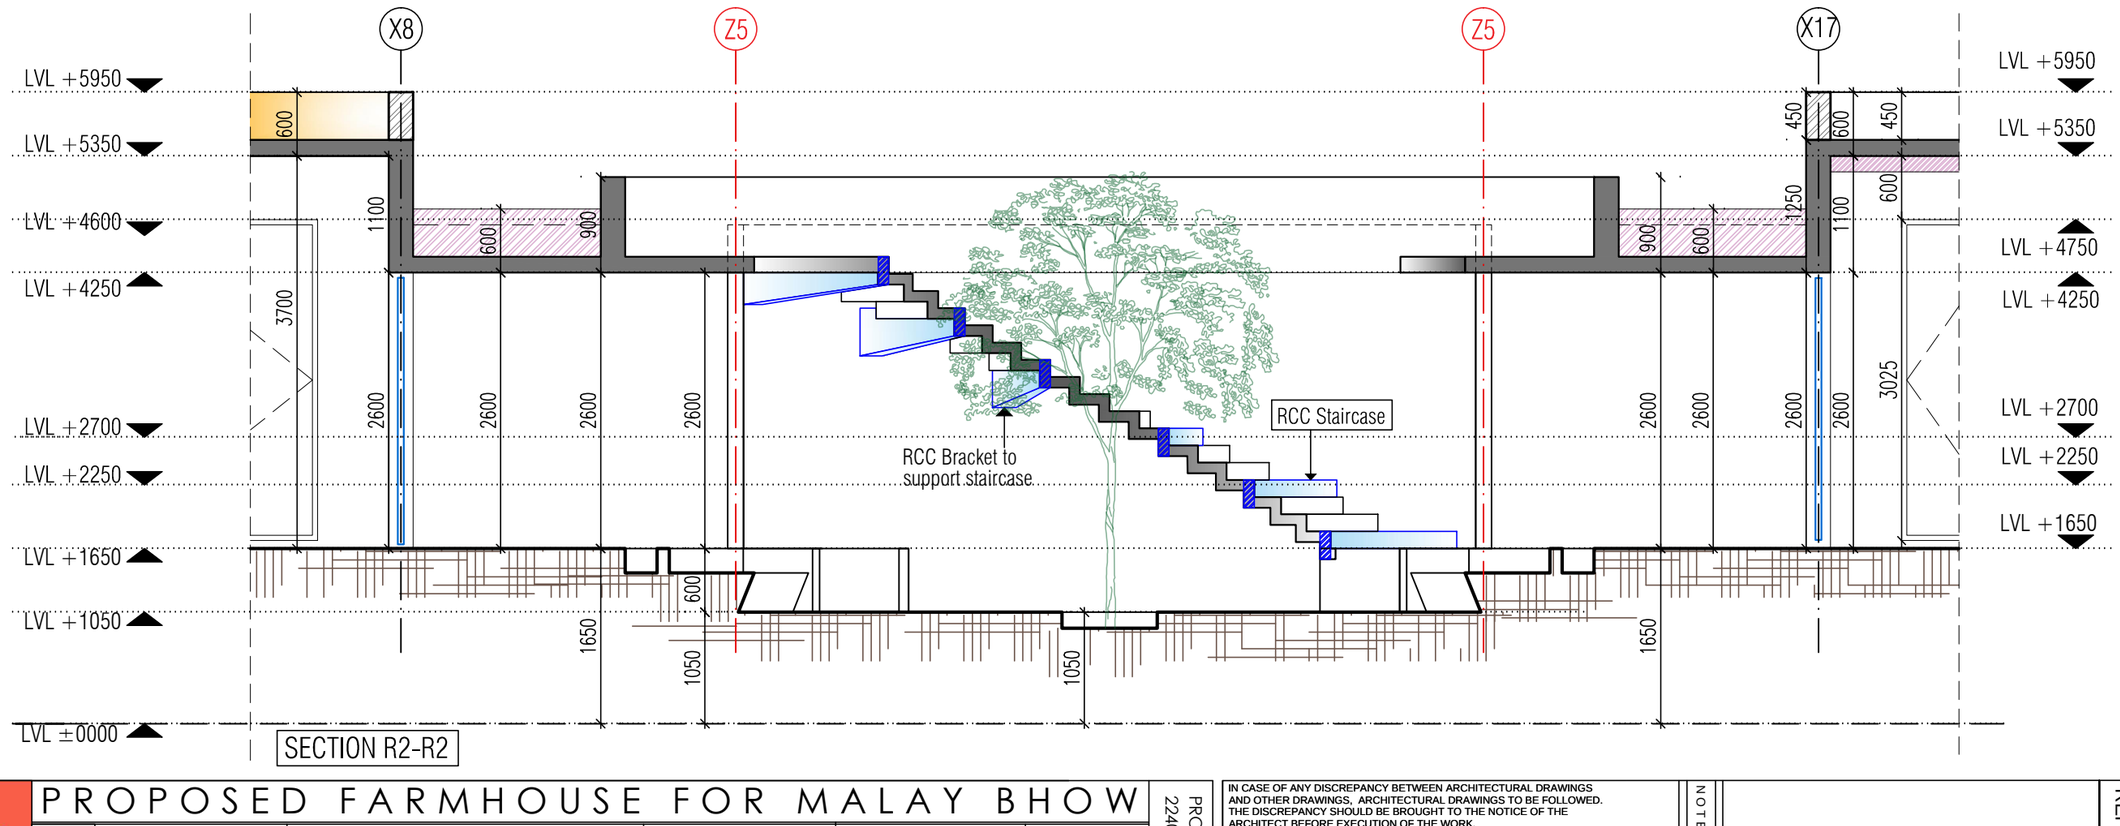

SECTION R2-R2

PROPOSED FARMHOUSE FOR MALAY BHOW

m/s ajit mathews

DRAWING DETAILS				
DRAWING NAME	HORIZONTAL AND VERTICAL SECTIONS	DRAWING NO.		A2
DRAWING PARTICULAR	HORIZONTAL AND VERTICAL SECTIONS	REVISION NO.		
DRAWING SCALE	1 : 60	DRAWN BY	BHRUVI	
DATE	19TH SEPTEMBER, 2024	CHECKED BY	A.M.	

PROJECT NO. 22402

NOTES

IN CASE OF ANY DISCREPANCY BETWEEN ARCHITECTURAL DRAWINGS AND OTHER DRAWINGS, ARCHITECTURAL DRAWINGS TO BE FOLLOWED. THE DISCREPANCY SHOULD BE BROUGHT TO THE NOTICE OF THE ARCHITECT BEFORE EXECUTION OF THE WORK.

ALL DIMENSIONS ARE TO BE READ AND NOT MEASURED.

ALL DIMENSIONS ARE IN MILLIMETERS.

LEVELS AS SHOWN ON THE PLAN ARE TAKEN WITH RESPECT TO THE TOP OF THE ROAD LEVEL OUT SIDE THE MAIN ENTRANCE GATE WHICH IS ASSUMED AS 0' 00" LEVEL

FLOOR LEVELS SHOWN IN THE PLAN TO BE CONSIDERED AS FINISHED FLOOR LEVELS

LEVELS AS MENTIONED IN THE OPENING SCHEDULES IS REFERRED WITH RESPECT TO THE FINISHED FLOOR LEVEL OF THE RESPECTIVE FLOOR.

EMAIL REFERENCE

314, SAMAAN, PREMCHANDNAGAR ROAD, VASTRAPUR, AHMEDABAD-380015, GUJARAT. PH: 26760412 , 9979882327. EMAIL: contact@ajitmathews.com. WEBSITE: WWW.ajitmathews.com