
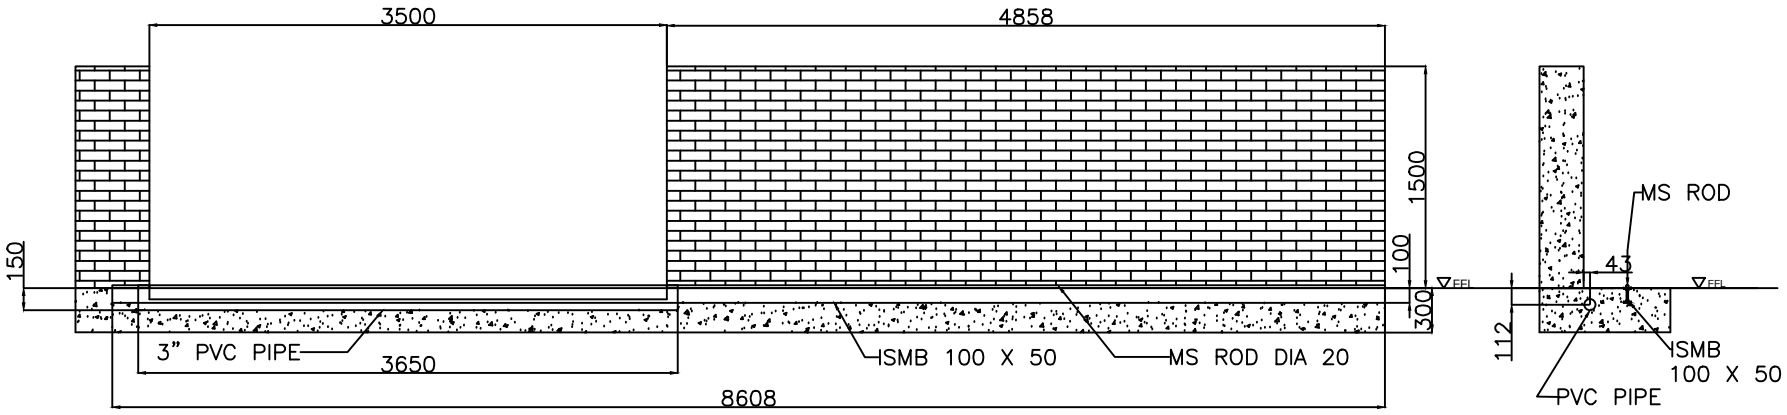


ELEVATION VIEW

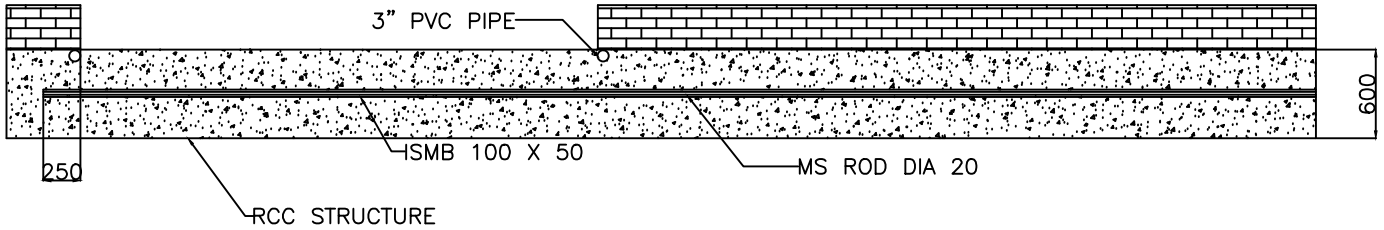

PLAN

Technical Specs of Motorized Sliding Gate

1. Parking length required - 5250mm
2. Bottom Rail - Bright bar Ø20mm
3. Total leaf weight ≈ 790 kg
4. ISMB 100 X 50 positioned in the foundation.

Note-

1. All dimension are in mm.
2. All civil work is under client scope.
3. 3" PVC pipe in the foundation to be provided by NIHVA.
4. Power supply 3 phase 440v, 50hz.
5. Cable for power supply 2.5 sqmm 4 core
6. Cable for photocell - 1.5 sqmm 4 core

This drawing & design is the property of NIHVA TECHNOLOGIES. Not to be sold or copied to any other concern.

TITLE				
SLIDING GATE FOUNDATION DRAWING				NIHVA TECHNOLOGIES PVT. LTD. PUNE Tel : 020 66304033 Email:- info@nihva.com Website:- www.nihva.com
	NAME	SIGN	DATE	
DRAWN	G.P.		08.09.21	CLIENT -HAIMAVATHY PROPERTIES PVT. LTD.
CHECK	A.K.		08.09.21	LOCATION - MUMBAI
APPRD.	V.T.		08.09.21	PRODUCT - SLIDING GATE 3500 X 2000
If any queries contact : design@nihva.com				NIHVA\21-22\0229 / REV- 00
ALL DIMENSION ARE IN mm				SCALE: NTS / SHEET: 02 OF 02