


PRODUCED BY AN AUTODESK EDUCATIONAL PRODUCT
THIS PRINT IS THE PROPERTY OF NIHVA IT IS TO BE USED ONLY FOR THE PURPOSE FOR WHICH IT WAS LENT AND MUST NOT BE USED IN ANY WAY DERTIMENTAL TO THE INTEREST OF THIS COMPANY AND IS SUBJECT TO RETURN ON DEMAND.

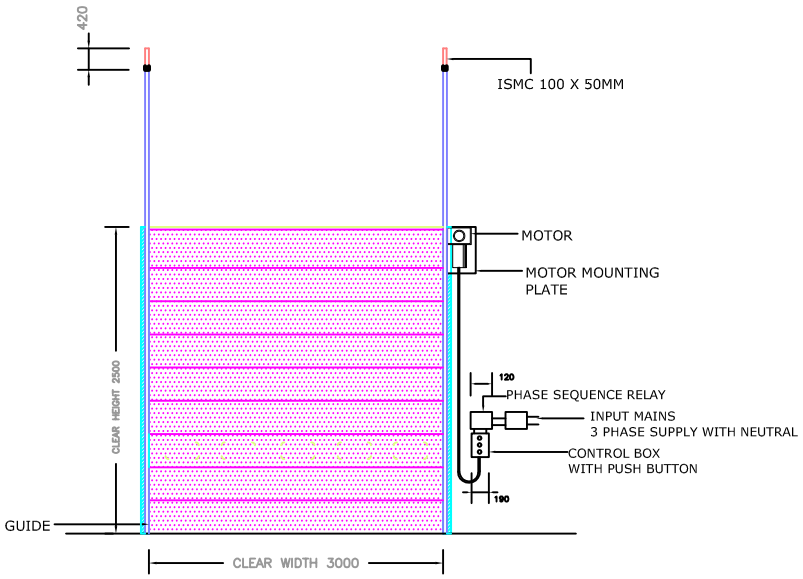


ELEVATION

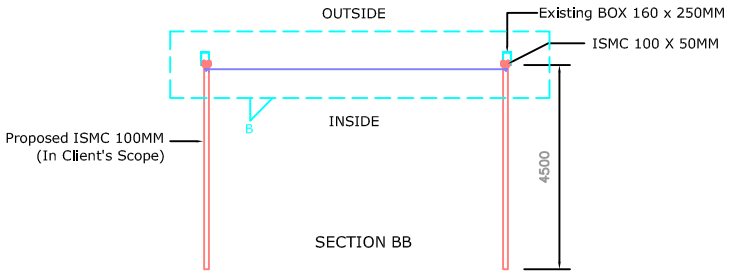

SECTION BB

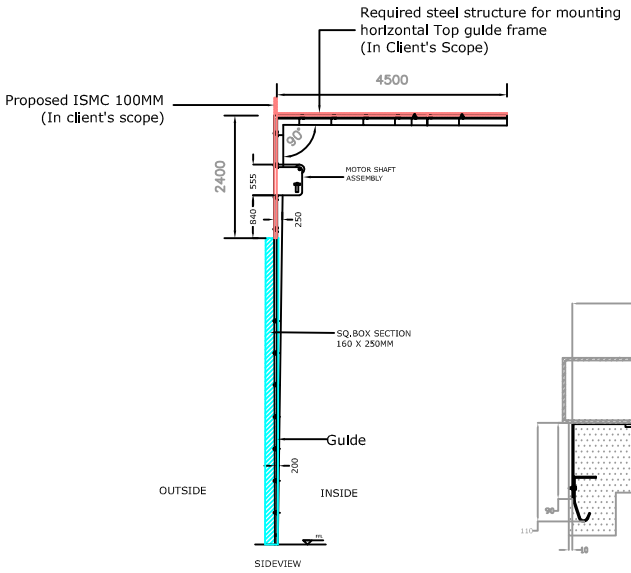

SIDEVIEW

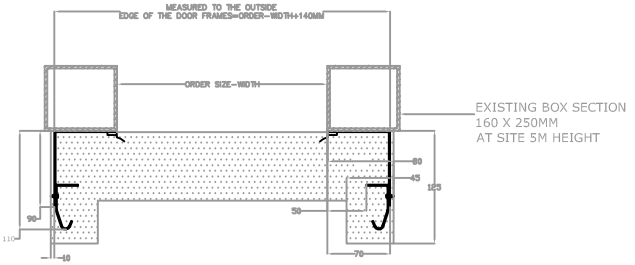

DETAILS OF C

SECTIONAL DOOR SIZE :- 2.5M(W) X 3.5M(H)

TITLE: SECTIONAL DOOR	DO NOT SCALE DRAWING		NIHVA TECHNOLOGIES PVT. LTD. Pune:-411044
		SIGN / DATE	NIHVA TECHNOLOGIES PVT. LTD. Tel :- 020 66304033 Email :- info@nihva.com
CLIENTS APPROVEL:–	DRAWN		CLIENT: CCCL
	CHECK		PROJECT : MCCAIN FOODS(I) PVT LTD
	ENG		PRODUCT NAME: MESHANA-GUJARAT
	APPRD.		DWG. NO.:
ALL DIMENSION ARE IN M.M.	PROD		REV.: 1
If any queries CONTACT: projects@nihva.com	MFG		SCALE: NTS WT: SHEET: 1 OF 1
	Ref. No.		

PRODUCED BY AN AUTODESK EDUCATIONAL PRODUCT