

EXIT GATE

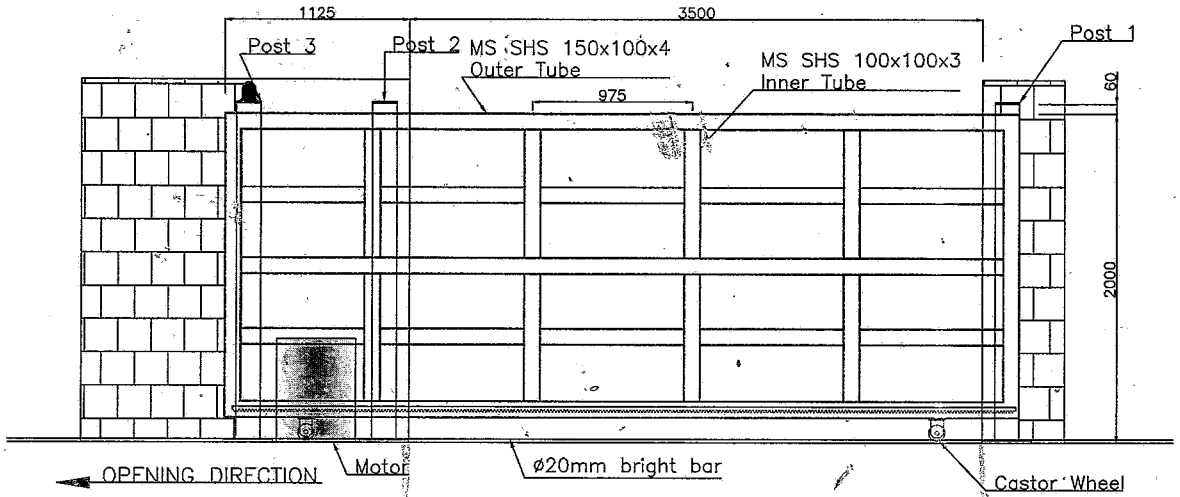


ELEVATION VIEW

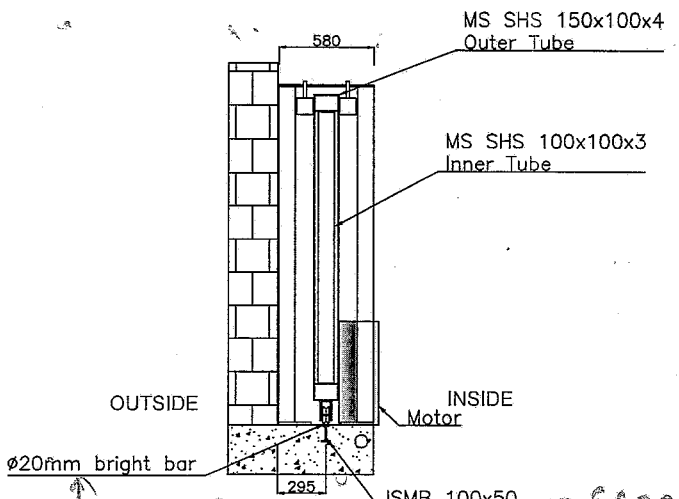

Scope ℓ

INSIDE.

Scope ℓ

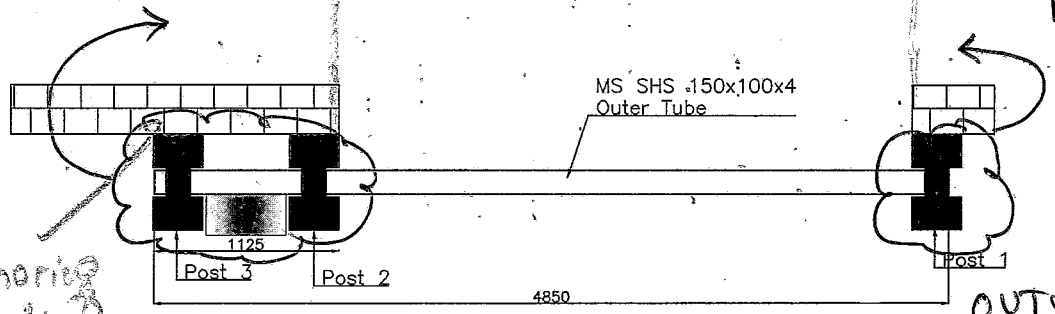

Anchoring details ℓ

OUTSIDE

Scope ℓ

PLAN

SLIDE

SIDE VIEW

Technical Specs of Motorized Sliding Gate


1. Opening length - 3500mm
2. Gate Height - 2000mm
3. Parking length required - 4850mm
4. Outer tube size - MS SHS 150x100x4mm
5. Inner tube size - MS SHS 100x100x3mm
6. Bottom Rail - Bright bar Ø20mm
7. Post size - MS SHS 150x100x4mm
8. Total leaf weight ≈ kg
9. Safety feature - Photocell and flashing light
10. Operation - Push button from side

Note-


1. All dimension are in mm.
2. All civil work is under client scope.
3. 3" PVC pipe in the foundation to be provided by client.
4. Power supply single phase 230v, 50hz.
5. Cable for power supply 2.5 sqmm 3 core
6. Cable for photocell - 1.5 sqmm 4 core

This drawing & design is the property of NIHVA TECHNOLOGIES. Not to be sold or copied to any other concern.

TITLE	SLIDING GATE			NIHVA TECHNOLOGIES PVT. LTD. PUNE
	NAME	SIGN	DATE	NIHVA TECHNOLOGIES PVT. LTD. Tel : 020 66304033 Email:- info@nihva.com Website:- www.nihva.com
DRAWN	G.P.		10.08.21	CLIENT -HAIMAVATHY PROPERTIES PVT. LTD.
CHECK	A.K.		10.08.21	LOCATION - MUMBAI
APPRD.	V.T.		10.08.21	PRODUCT - SLIDING GATE 3500 X 2000
If any queries contact : design@nihva.com				NIHVA\20-21\0191 REV- 0
ALL DIMENSION ARE IN mm				SCALE: NTS SHEET: 01 OF 02

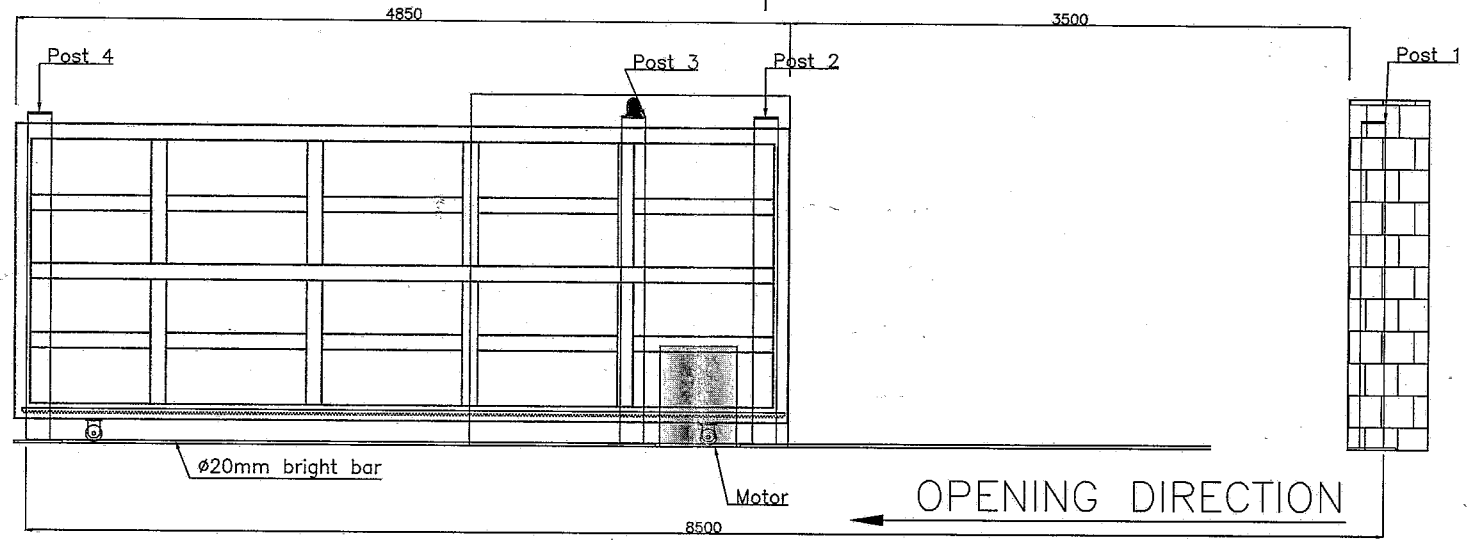

STACKED GATE ELEVATION

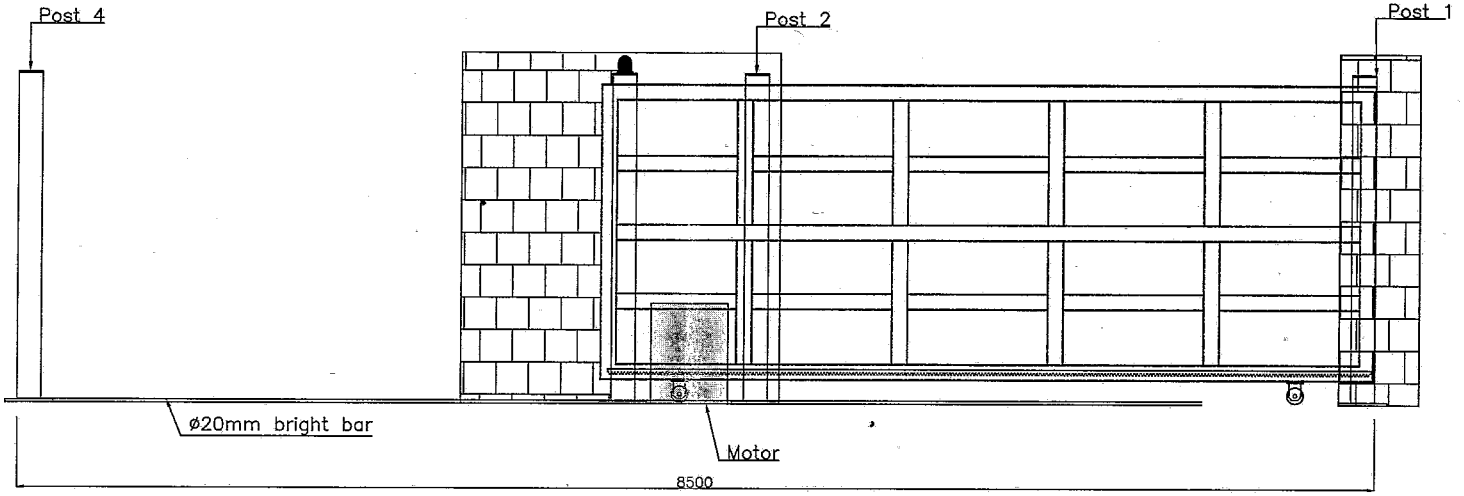


CLOSED GATE ELEVATION

This drawing & design is the property of NIHVA TECHNOLOGIES. Not to be sold or passed to any other person.


TITLE: SLIDING GATE				NIHVA TECHNOLOGIES PVT. LTD. PUNE Tel : 020 66304033 Email:- info@nihva.com Website:- www.nihva.com
	NAME	SIGN	DATE	
DRAWN	G.P.		10.08.21	CLIENT -HAIMAVATHY PROPERTIES PVT. LTD.
CHECK	A.K.		10.08.21	LOCATION - MUMBAI
APPRD.	V.T.		10.08.21	PRODUCT - SLIDING GATE 3500 X 2000
If any queries contact : design@nihva.com				NIHVA\20-21\0191 REV- 0
ALL DIMENSION ARE IN mm				SCALE: NTS SHEET: 02 OF 02

ENTRY GATE

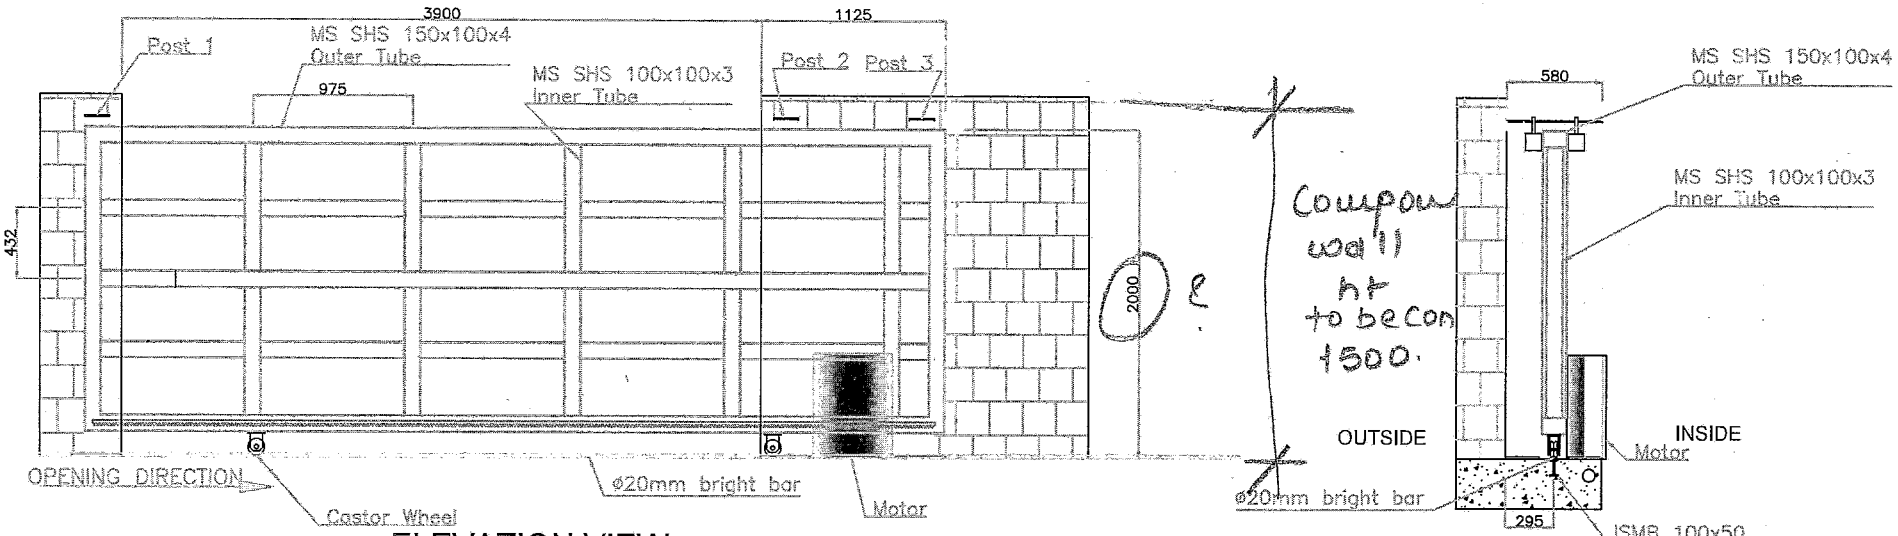

ELEVATION VIEW

SIDE VIEW

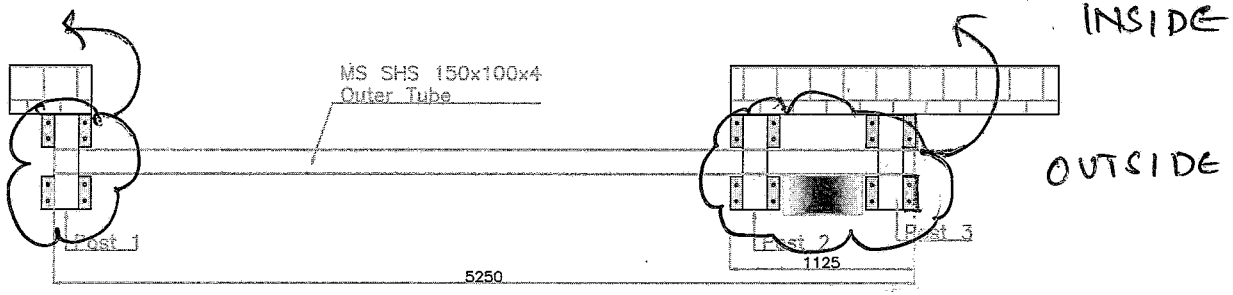

PLAN

Technical Specs of Motorized Sliding Gate

1. Opening length - 3900mm
2. Gate Height - 2000mm
3. Parking length required - 5250mm
4. Outer tube size - MS SHS 150x100x4mm
5. Inner tube size - MS SHS 100x100x3mm
6. Bottom Rail - Bright bar Ø20mm
7. Post size - MS SHS 150x100x4mm
8. Total leaf weight ≈ kg
9. Safety feature - Photocell and flashing light
10. Operation - Push button from side

Note-

1. All dimension are in mm.
2. All civil work is under client scope.
3. 3" PVC pipe in the foundation to be provided by client.
4. Power supply single phase 230v, 50hz.
5. Cable for power supply 2.5 sqmm 3 core
6. Cable for photocell - 1.5 sqmm 4 core

This drawing & design is the property of NIHVA TECHNOLOGIES. Not to be sold or copied to any other concern.


TITLE
SLIDING GATE

NIHVA
NIHVA TECHNOLOGIES PVT. LTD.


NIHVA TECHNOLOGIES PVT. LTD. PUNE
Tel : 020 66304033
Email:- info@nihva.com
Website:- www.nihva.com

	NAME	SIGN	DATE
DRAWN	G.P.		10.08.21
CHECK	A.K.		10.08.21
APPRD.	V.T.		10.08.21

CLIENT -HAIMAVATHY PROPERTIES PVT. LTD.	
LOCATION - MUMBAI	
PRODUCT - SLIDING GATE 3900 X 2000	
If any queries contact : design@nihva.com	NIHVA\20-21\0192 REV- 0
ALL DIMENSION ARE IN mm	SCALE: NTS SHEET: 01 OF 02

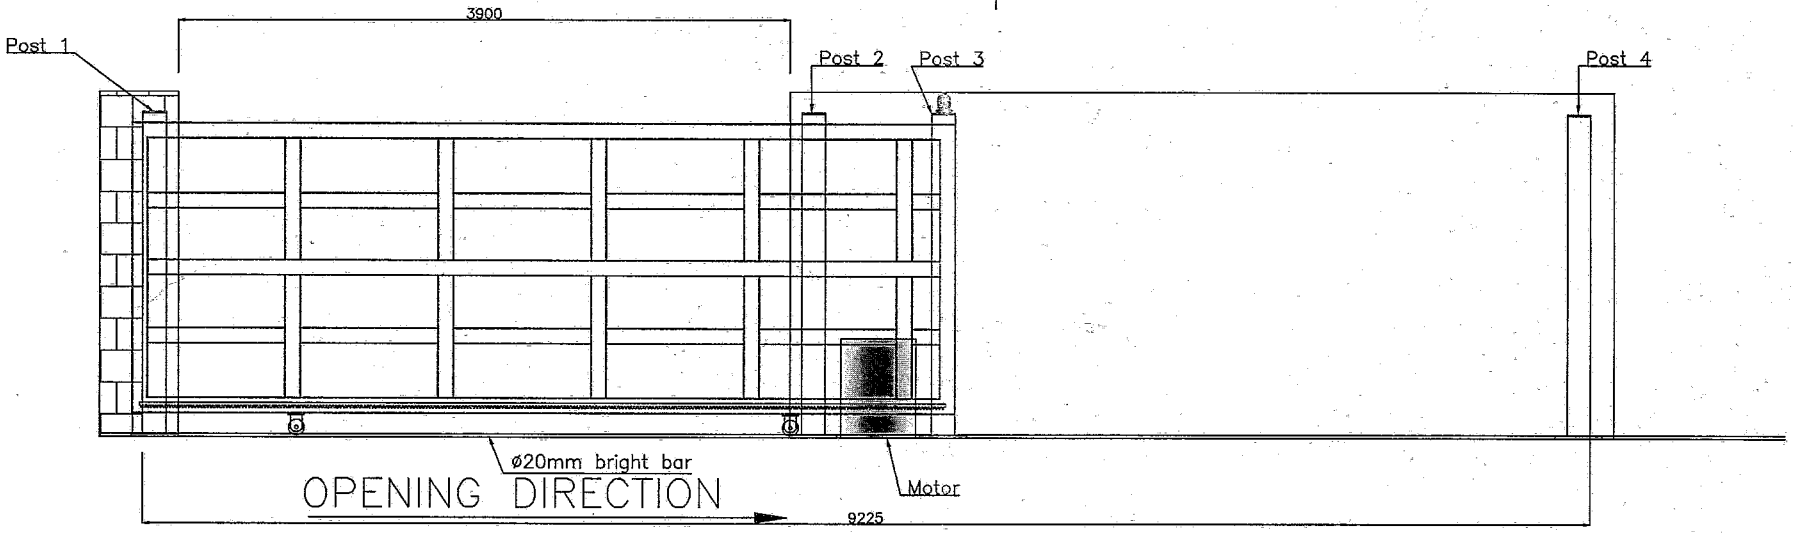

CLOSED GATE ELEVATION

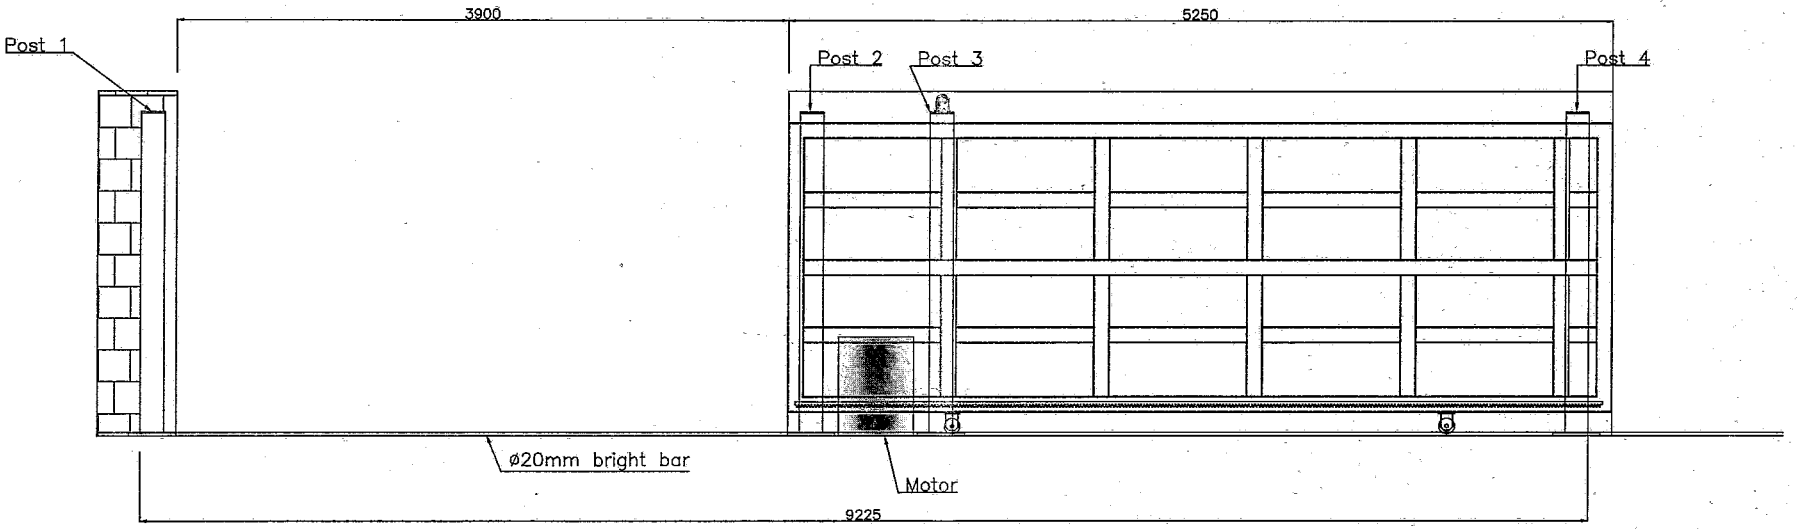

STACKED GATE ELEVATION

This drawing & design is the property of NIHVA TECHNOLOGIES. Not to be sold or copied to any other concern.

TITLE
SLIDING GATE

NIHVA
NIHVA TECHNOLOGIES PVT. LTD.

NIHVA TECHNOLOGIES
PVT. LTD. PUNE
Tel : 020 66304033
Email:- info@nihva.com
Website:- www.nihva.com

	NAME	SIGN	DATE
DRAWN	G.P.		10.08.21
CHECK	A.K.		10.08.21
APPRD.	V.T.		10.08.21

If any queries contact : design@nihva.com

ALL DIMENSION ARE IN mm

CLIENT -HAIMAVATHY PROPERTIES PVT. LTD.


LOCATION - MUMBAI


PRODUCT - SLIDING GATE 3500 X 2000

NIHVA\20-21\0192 | REV- 0

SCALE: NTS | SHEET: 02 OF 02

WICKET ENTRY GATE

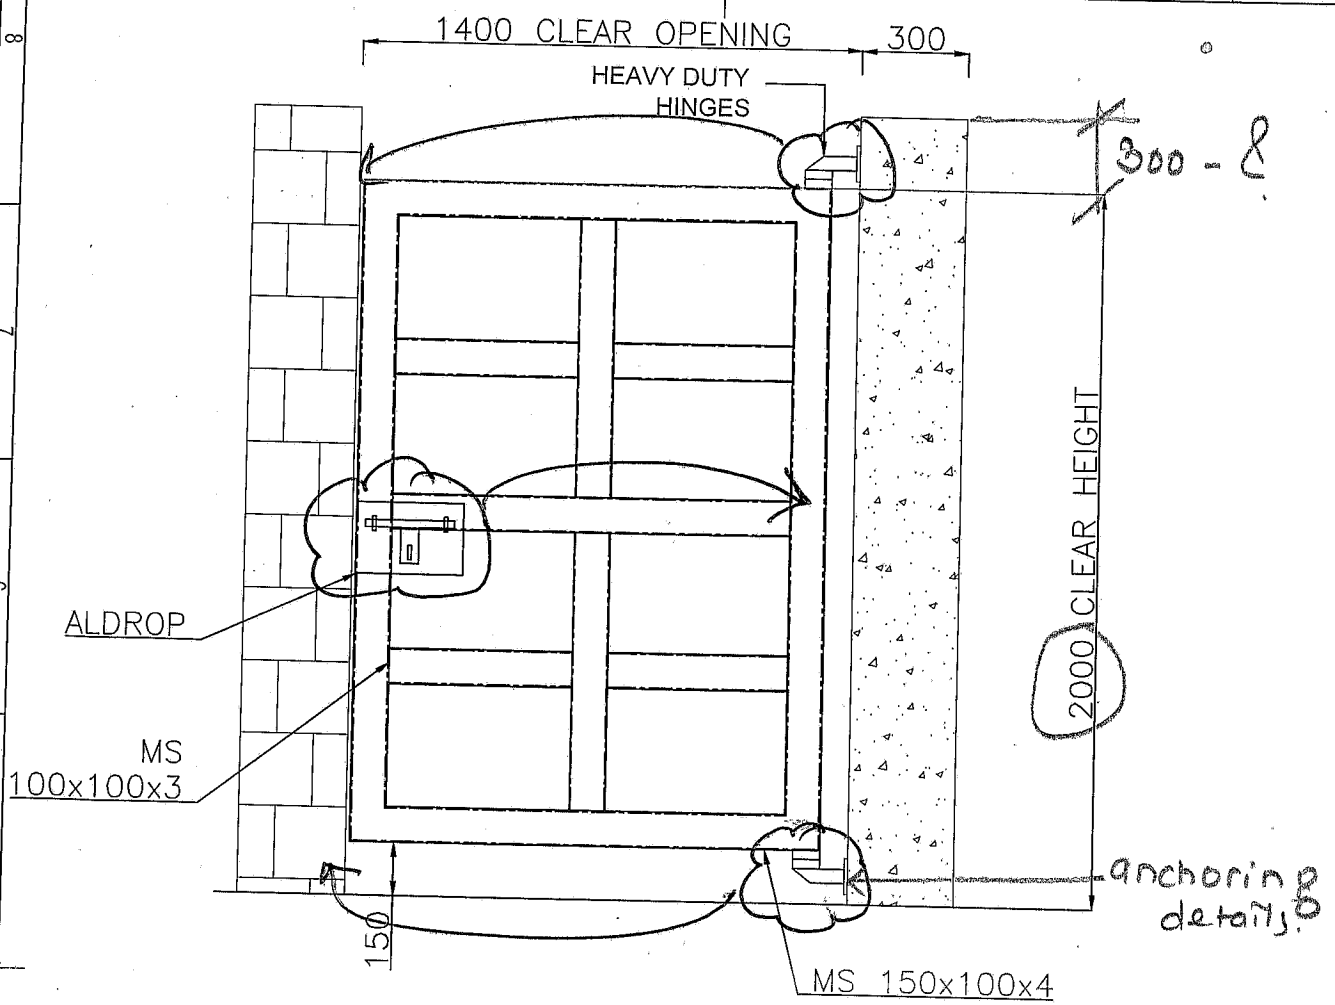

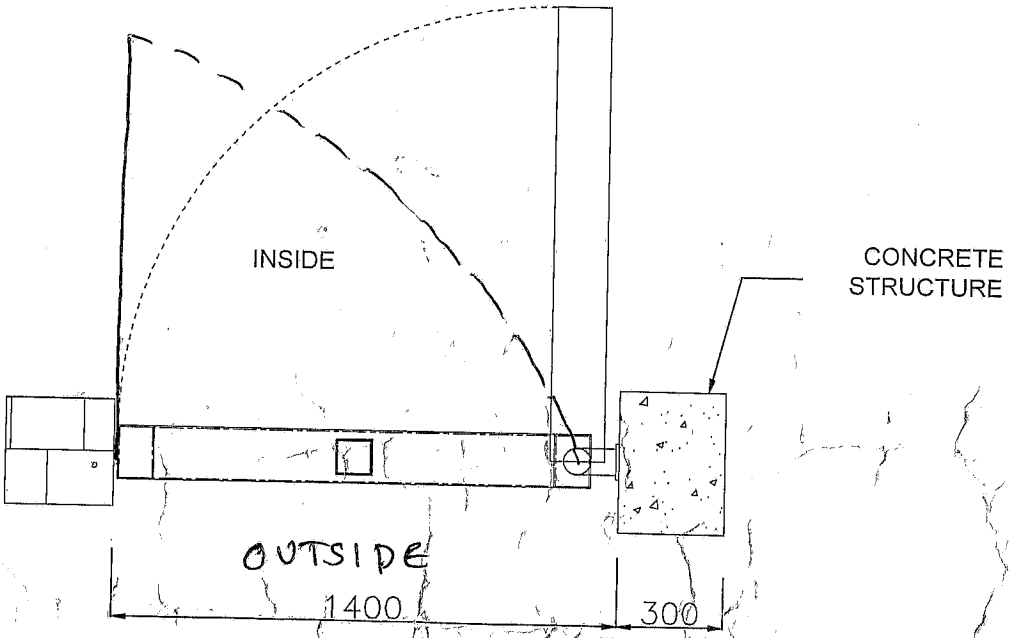

Technical Specs of Swing Gate

1. Opening Width - 1400mm
2. Gate Height - 2000mm
3. Outer tube size - MS SHS 150x100x4mm
4. Inner tube size - MS SHS 100x100x3mm
5. Total leaf weight ≈ 180 kg
6. Operation - Manual

Note

1. All dimension are in mm.
2. All civil work is under client scope.


This drawing is the property of NIHVA TECHNOLOGIES PVT. LTD. and is not to be used without permission.

TITLE: WICKET GATE			
	NAME	SIGN	DATE
DRAWN	G.P.		09.08.21
CHECK	A.K.		09.08.21
APPRD.	V.T.		09.08.21


NIHVA TECHNOLOGIES PVT. LTD.
NIHVA TECHNOLOGIES PVT. LTD. PUNE
Tel.: 020 66304033
Email:- info@nihva.com
Website:- www.nihva.com

CLIENT -HAIMAVATHY PROPERTIES PVT. LTD.
LOCATION - MUMBAI
PRODUCT - WICKET GATE 1400 X 2000
NIHVA\20-21\0193 REV- 0
If any queries contact : design@nihva.com
ALL DIMENSION ARE IN mm
SCALE: NTS
SHEET: 01 OF 01


SWING EXIT GATE

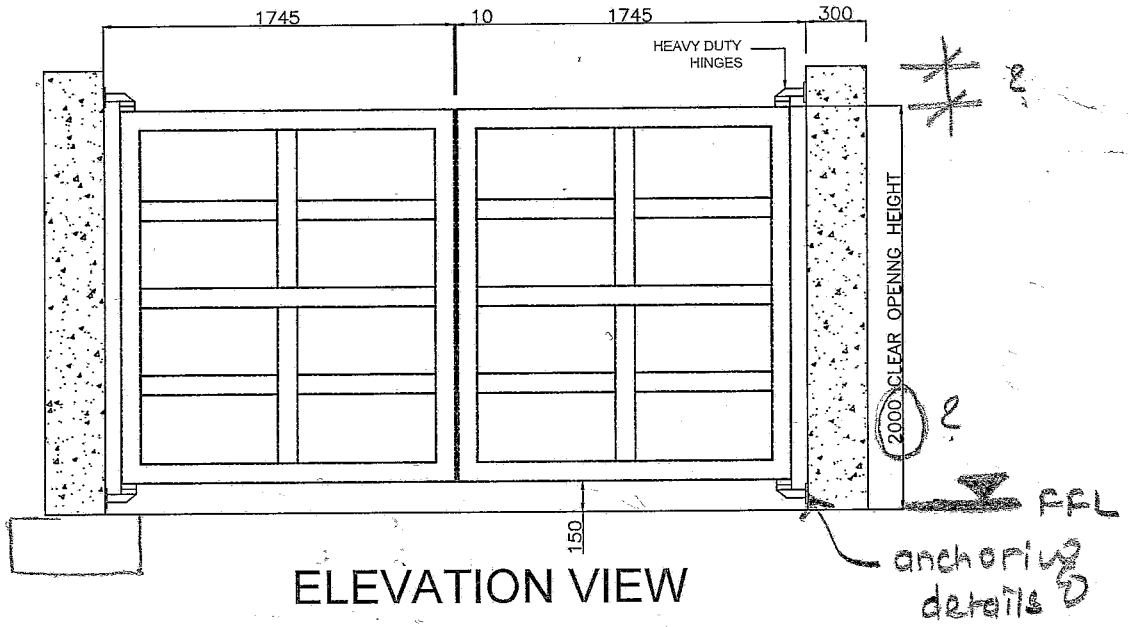

ELEVATION VIEW

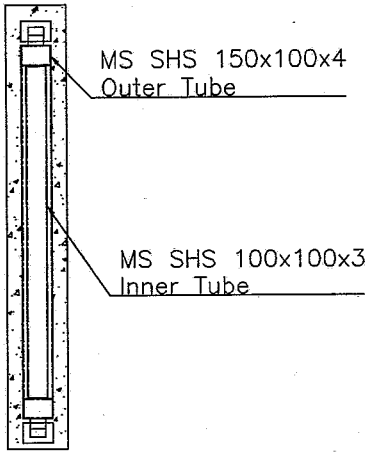

SIDE VIEW

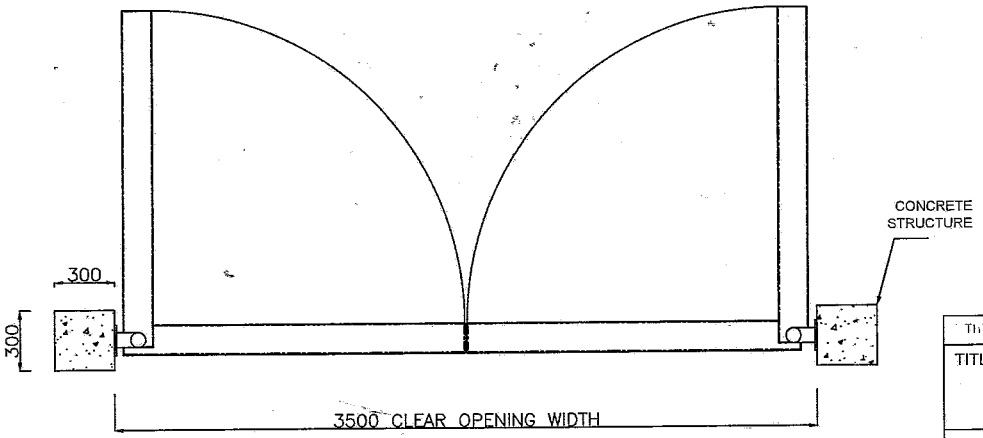

PLAN

Technical Specs of Swing Gate

1. Opening Width - 3500mm
2. Gate Height - 2000mm
3. Outer tube size - MS SHS 150x100x4mm
4. Inner tube size - MS SHS 100x100x3mm
5. Total leaf weight ≈ kg
6. Operation - Manual

Note-

1. All dimension are in mm.
2. All civil work is under client scope.

This drawing & design is the property of NIHVA TECHNOLOGIES. It is not to be sold or copied to any other concern.

TITLE			
SWING GATE			
	NAME	SIGN	DATE
DRAWN	G.P.		10.08.21
CHECK	A.K.		10.08.21
APPRD.	V.T.		10.08.21


NIHVA TECHNOLOGIES PVT. LTD.
NIHVA TECHNOLOGIES PVT. LTD. PUNE
Tel : 020 66304033
Email:- info@nihva.com
Website:- www.nihva.com

CLIENT -HAIMAVATHY PROPERTIES PVT. LTD.	
LOCATION - MUMBAI	
PRODUCT - SWING GATE 3500 X 2000	
NIHVA\20-21\0194	REV- 0
SCALE: NTS	SHEET: 01 OF 01

If any queries contact : design@nihva.com


ALL DIMENSION ARE IN mm

TENANT GATE

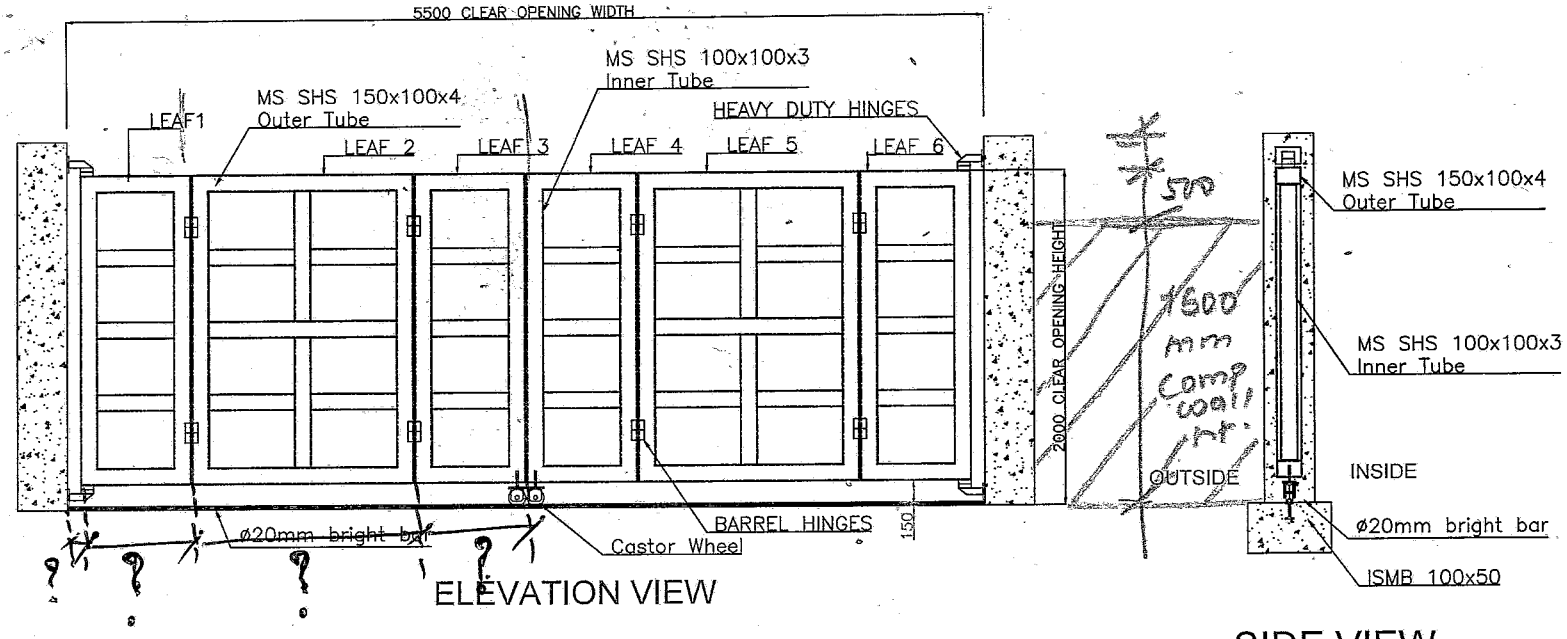

ELEVATION VIEW

SIDE VIEW

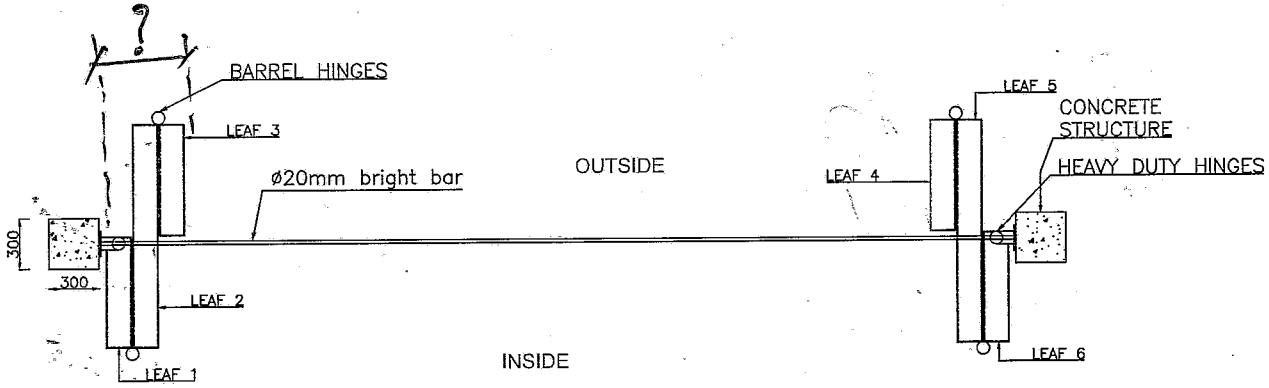

PLAN

Technical Specs of Swing Gate

1. Opening Width - 5500mm
2. Gate Height - 2000mm
3. No of Leaf : 6 nos
4. Outer tube size - MS SHS 150x100x4mm
5. Inner tube size - MS SHS 100x100x3mm
6. Operation - Manual

Note-

1. All dimension are in mm.
2. All civil work is under client scope.

This drawing & design is the property of NIHVA TECHNOLOGIES. Not to be sold or copied to any other concern.

TITLE

SLIDING AND FOLDING GATE

	NAME	SIGN	DATE
DRAWN	G.P.		10.08.21
CHECK	A.K.		10.08.21
APPRD.	V.T.		10.08.21

If any queries contact : design@nihva.com

ALL DIMENSION ARE IN mm

NIHVA

NIHVA TECHNOLOGIES PVT. LTD.

NIHVA TECHNOLOGIES PVT. LTD. PUNE
Tel : 020 66304033
Email:- info@nihva.com
Website:- www.nihva.com

CLIENT -HAIMAVATHY PROPERTIES PVT. LTD.

LOCATION - MUMBAI

PRODUCT - SLIDING & FOLDING GATE 5500 X 2000

NIHVA\20-21\0203 REV- 0

SCALE: NTS

SHEET: 01 OF 02