


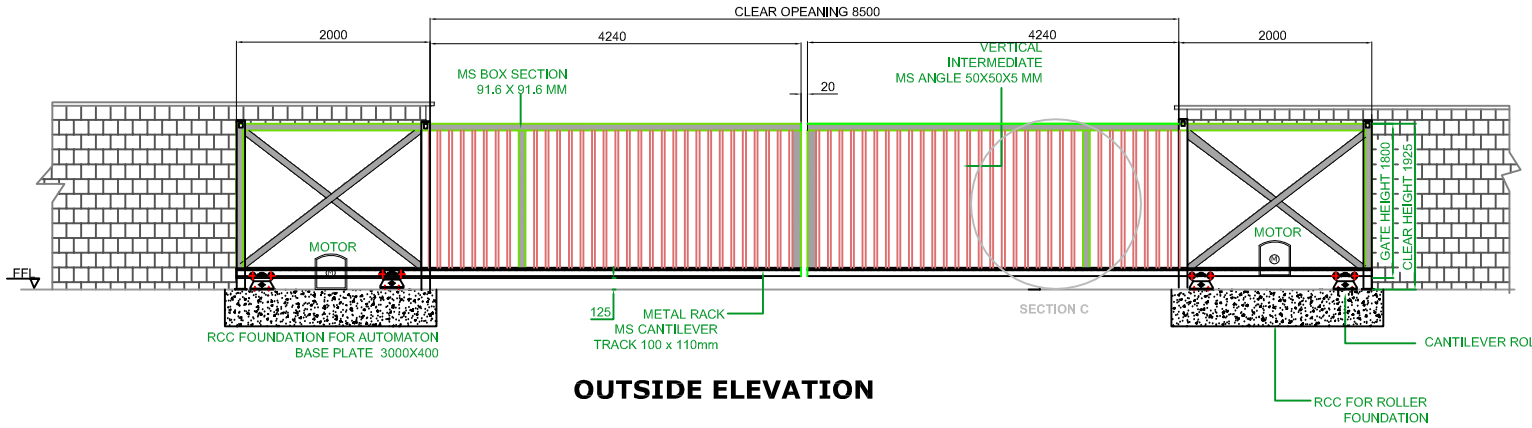


OUTSIDE ELEVATION

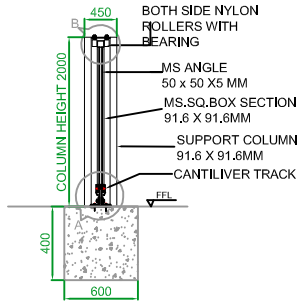


SIDEVIEW

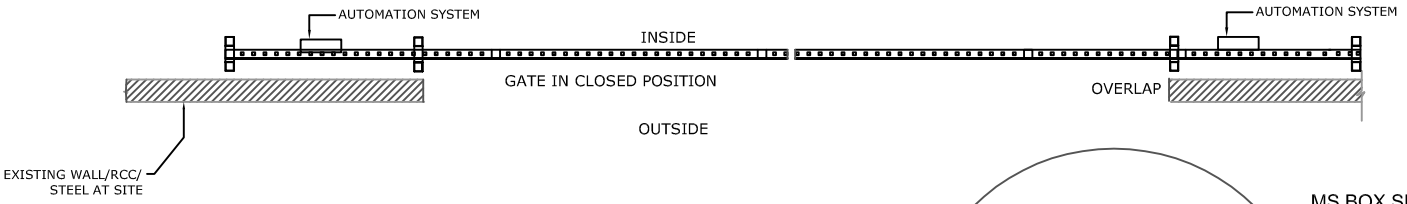


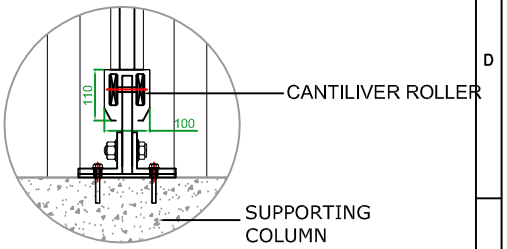


DETAILS OF A

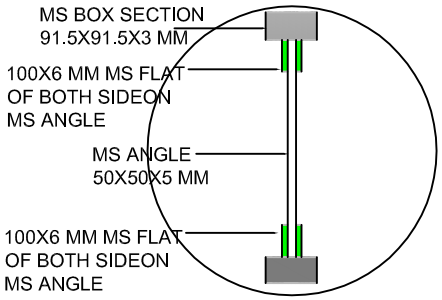

SIDE VIEW OF SECTION C

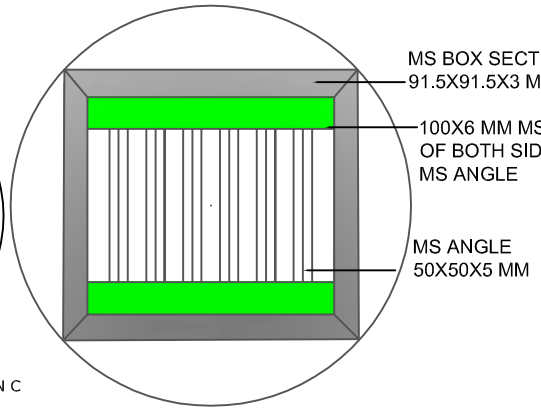

DETAILS OF C

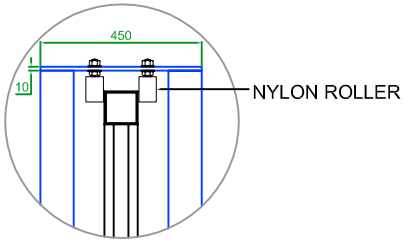

DETAILS OF B

SIZE OF GATE BIPARTING :- 8.5M(W) X 1.8M(H)

QTY:- 1 NOS

Note :-As per discussion we will Provide Hot dip galvanised gate structure; for that Price will be extra as applicable

TITLE: CANTILEVER SLIDING GATE -BIPARTING		SIGN	DATE
CLIENTS APPROVEL:–	DRAWN		
	CHECK		
	ENG		
	APPRD.		
ALL DIMENSION ARE IN M.M.	PROD		
If any queries CONTACT: projects@nihva.com	MFG		
	Ref. No.		

NIHVA TECHNOLOGIES PVT. LTD.

NIHVA TECHNOLOGY PVT. LTD. PUNE
Tel : 020 66304033
Email:- info@nihva.com
Website:- www.nihva.com

CLIENT:	SCON PROJECTS
PROJECT :	KERAKOLL- VADODRA
SITE :	VADODRA - GUJRAT
PRODUCT NAME:	CANTILEVER SLIDING GATE
DWG. NO.:	NVA/SCON/KERAKOLL/14-15/001
SCALE:	WT: SHEET: 1 OF 1