

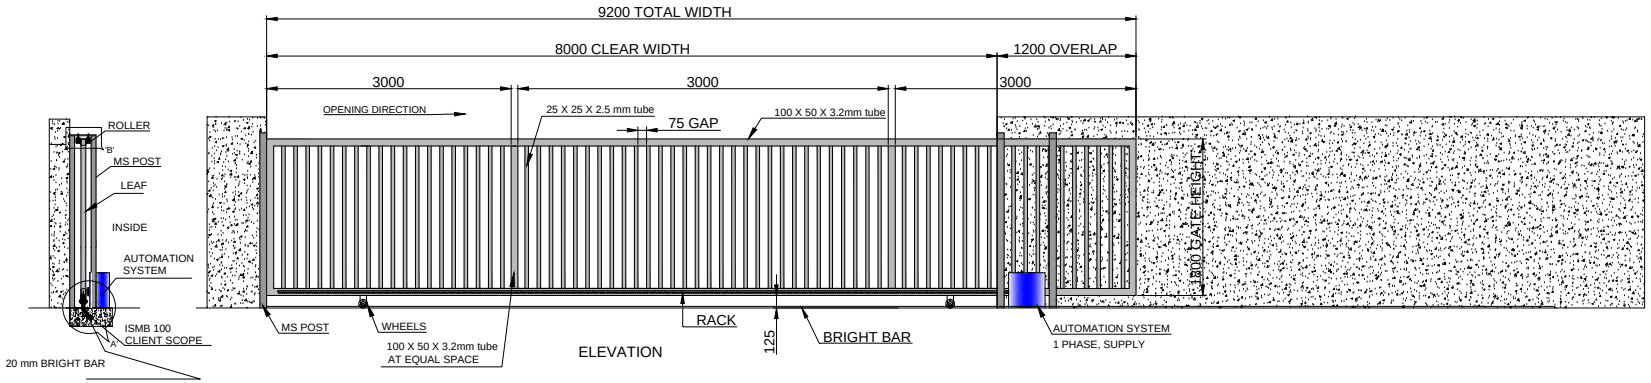



ELEVATION

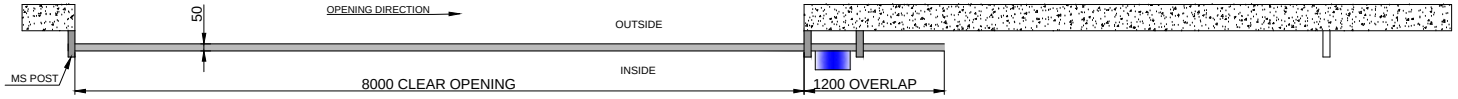


CLOSE POSITION PLAN VIEW

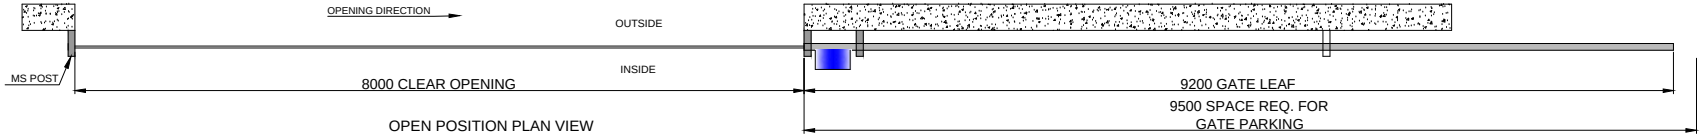

OPEN POSITION PLAN VIEW

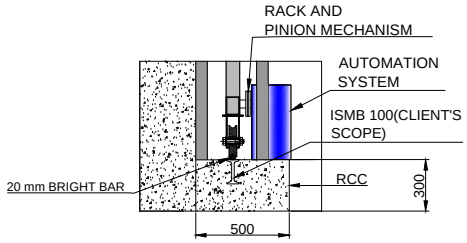

DETAIL VIEW OF A

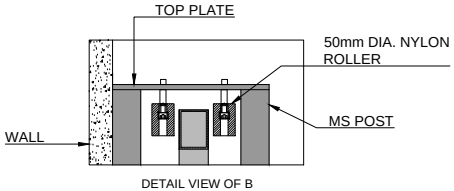

DETAIL VIEW OF B

NOTE-
1. ALL REQUIRED CIVIL WORK WILL BE IN CLIENTS SCOPE.
2. TWO COATS OF PRIMER AND TWO COATS OF SYNTHETIC ENAMEL PAINT OF APPROVE SHADE.
3. SAFETY ACCESSORIES : FLASHING LIGHT, SAFETY PHOTOCELL.
4. GATE LEAF WILL BE IN TWO/THREE PARTS FOR TRANSPORTATION & WILL BE WELD TOGETHER ON SITE.

GATE QTY : 2 NOS

TOLERANCE- ±10mm

REV NO	DATE	DRAWN	REMARK
R01	08.01.2020	P.A	1. CLEAR WIDTH CHANGE

This drawing & design is the property of NIHVA TECHNOLOGIES. Not to be sold or copied to any other concern.

TITLE: AUTOMATIC SLIDING GATE

NIHVA TECHNOLOGIES PVT. LTD. PUNE
Tel : 020 66304033
Email - info@nihva.com
Website:- www.nihva.com

	NAME	SIGN	DATE
DRAWN	P.A		23.12.2019
CHECK	G.J		23.12.2019
APPRD.			

CLIENT - DESAI CONSTRUCTIONS
PROJECT -
SITE LOCATION - GUJARAT
If any queries contact : design@nihva.com
DWG. NO. : NIHVA/19-20/0181/R01
REV- R01
ALL DIMENSION ARE IN mm
SCALE: NTS
WT:
SHEET: