
Weitergabe sowie Vervielfältigung dieses Dokuments, Verwertung und Mitteilung seines Inhalts sind nur nach vorheriger ausdrücklicher schriftlicher Zustimmung von SMS Meer GmbH gestattet. Das Dokument ist vor unberechtigtem Zugriff Dritter zu schützen. Zuwiderhandlungen verpflichten zu Schadenersatz. Alle Rechte aus Patent-/Gebrauchsmuster-/Markenschutz vorbehalten.

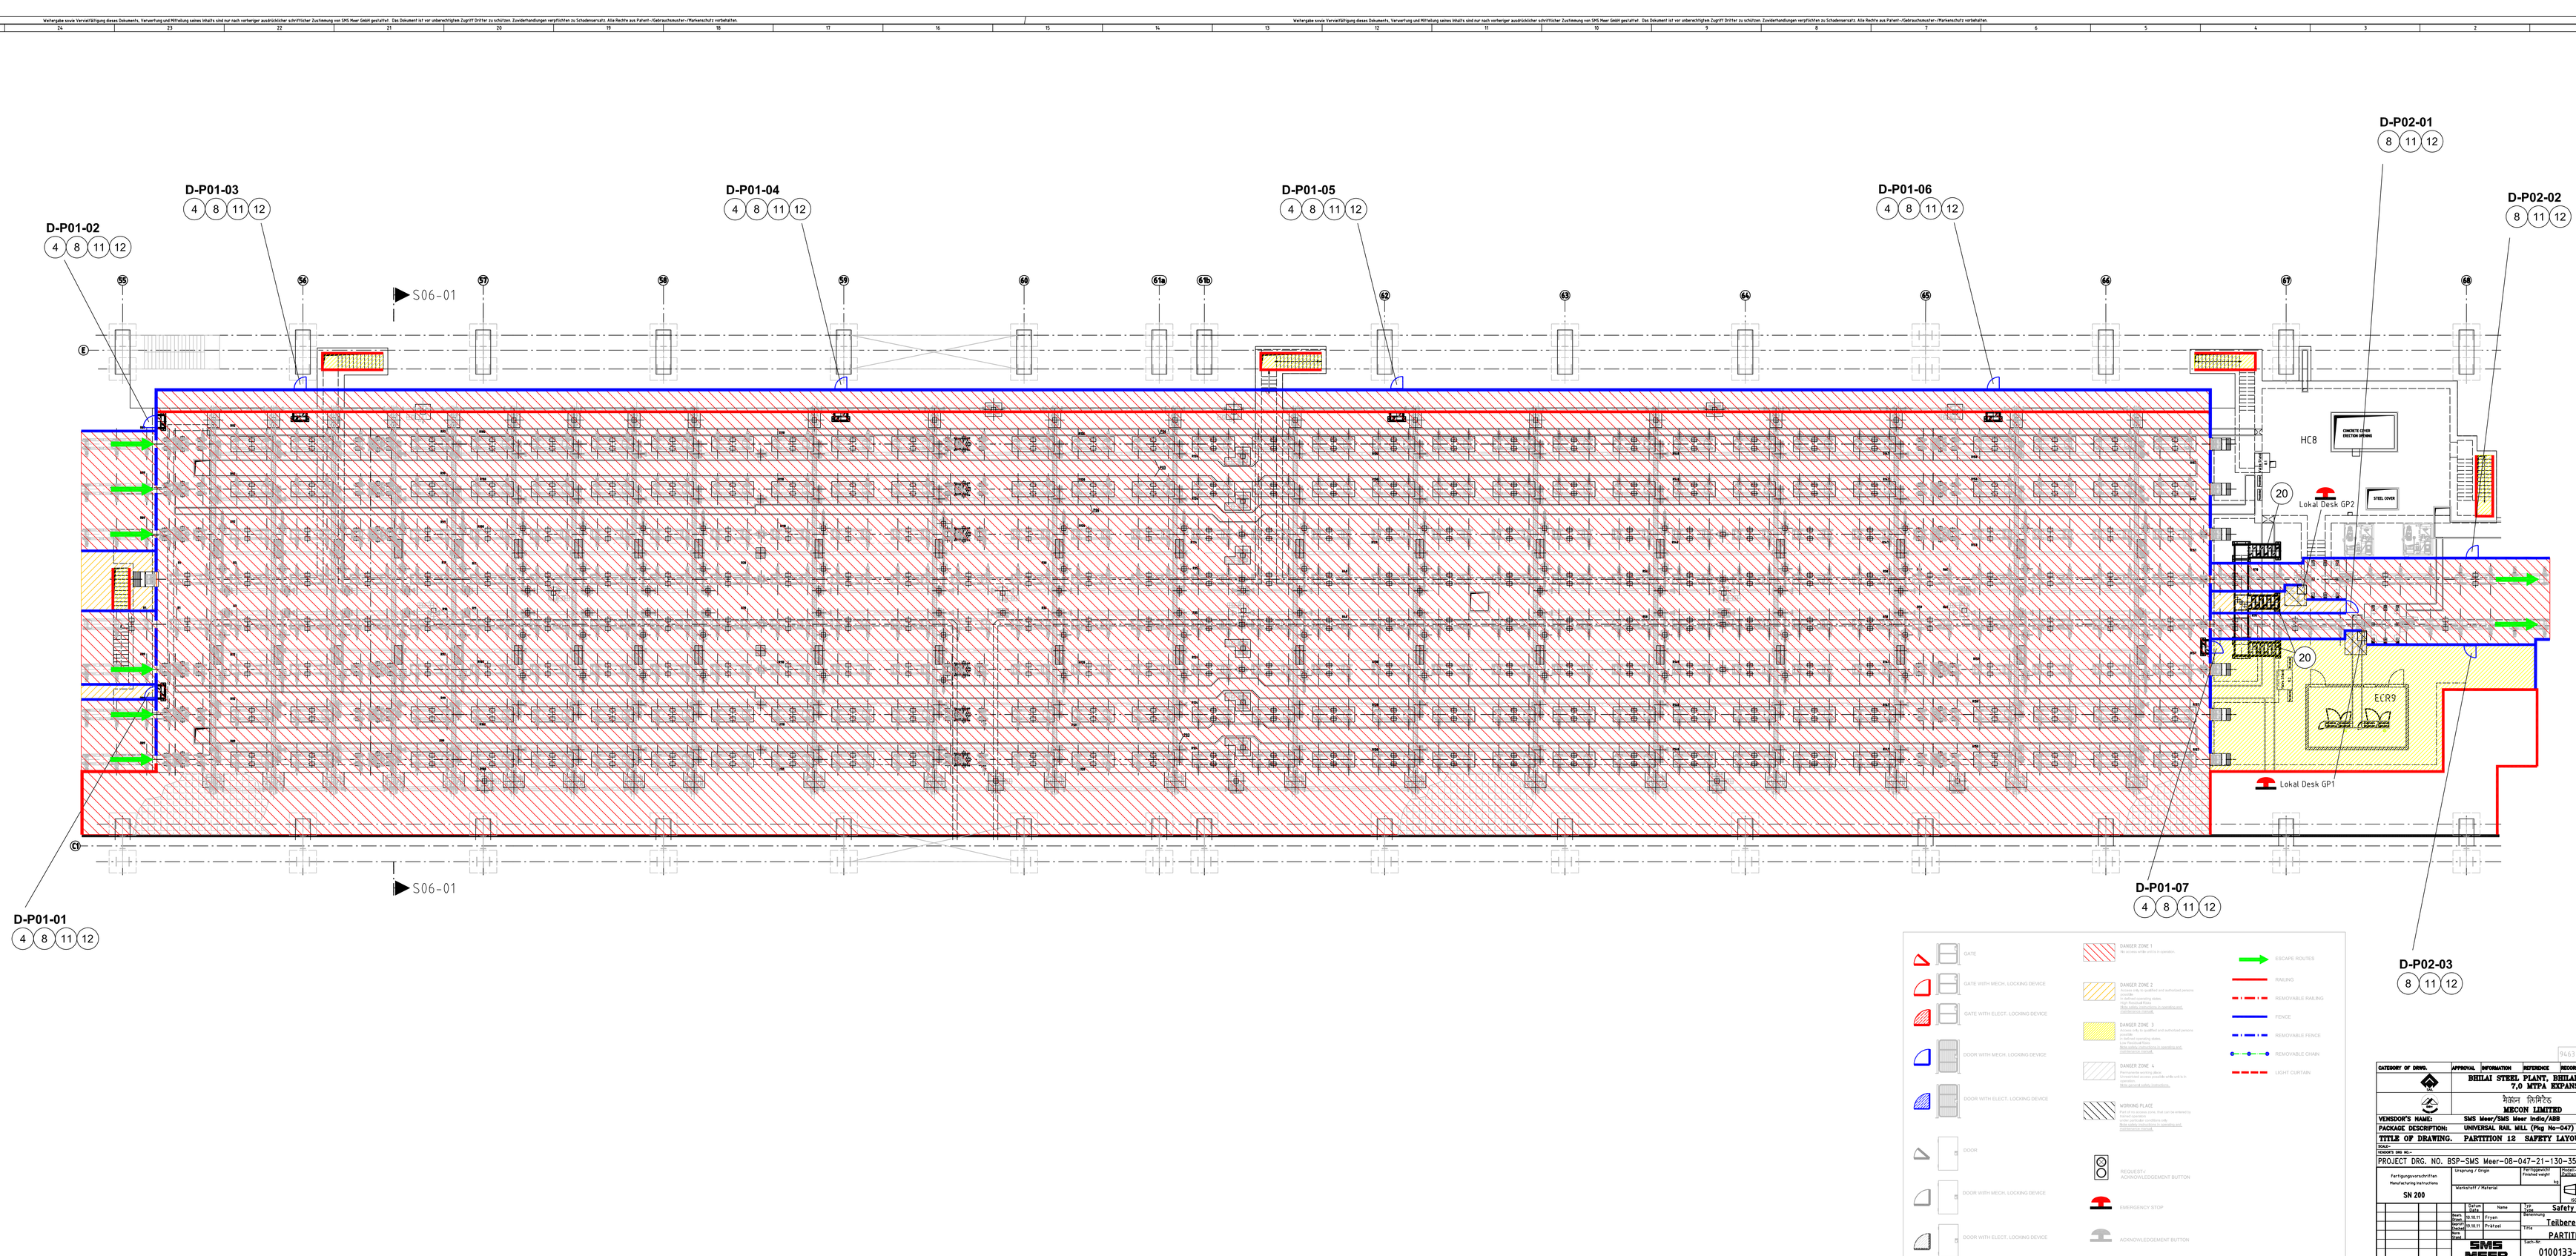

9463.0000 / RAILBHL

CATEGORY OF DRWG.	APPROVAL	INFORMATION	REFERENCE	RECORD	CONSTRUCTION

BHILAI STEEL PLANT, BHILAI, CHATTISGARH
7.0 MTPA EXPANSION

मेकॉन लिमिटेड
MECON LIMITED

VENDOR'S NAME: SMS Meer/SMS Meer India/ABB
PACKAGE DESCRIPTION: UNIVERSAL RAIL MILL (Pkg No-047)
TITLE OF DRAWING. PARTITION 12 SAFETY LAYOUT

Vendor's Drg. no.:
PROJECT DRG. NO. BSP-SMS Meer-08-047-21-130-35-BE-06659 REV. -

Fertigungsvorschriften / Manufacturing Instructions: SN 200
Umgang / Origin
Fertiggewicht / Finished weight: kg
Werkstoff / Material: S235
Projektionsmethode 1 / First angle projection method

			Datum / Date	Name	Zust. / Abteilung
			Bearb. / Drawn	16.10.15	Aryan
			Gepr. / Chkd.	16.10.15	Prahlad
			Norm.		
			Freig. / Appd.		

Safety Layout
Teilbereich, 12
PARTITION 12
Auftrag-Nr. / Order No.: 0100133-00.659
Zeichnung-Nr. / Drawing No.:
Maßst. / Scale: 1:100
Blatt / Sheet: 1
Format: A1

SMS MEER
SMS group

Änderung / Revision | Datum / Date | Name
Ersatz für / Supersedes
Ersetzt durch / Superseded by

Weitergabe sowie Vervielfältigung dieses Dokuments, Verwertung und Mitteilung seines Inhalts sind nur nach vorheriger ausdrücklicher schriftlicher Zustimmung von SMS Meer GmbH gestattet. Das Dokument ist vor unberechtigtem Zugriff Dritter zu schützen. Zuwiderhandlungen verpflichten zu Schadenersatz. Alle Rechte aus Patent-/Gebrauchsmuster-/Markenschutz vorbehalten.
This drawing and all information and data contained herein is the property of SMS Meer GmbH. Any unauthorized use, reproduction or disclosure is prohibited. The offender is liable for damages. All rights reserved in the event of the grant of a patent, utility model or design registration.
Diese Zeichnung und alle darauf enthaltenen Informationen sind vertraulich. This drawing and all information on it is confidential.