


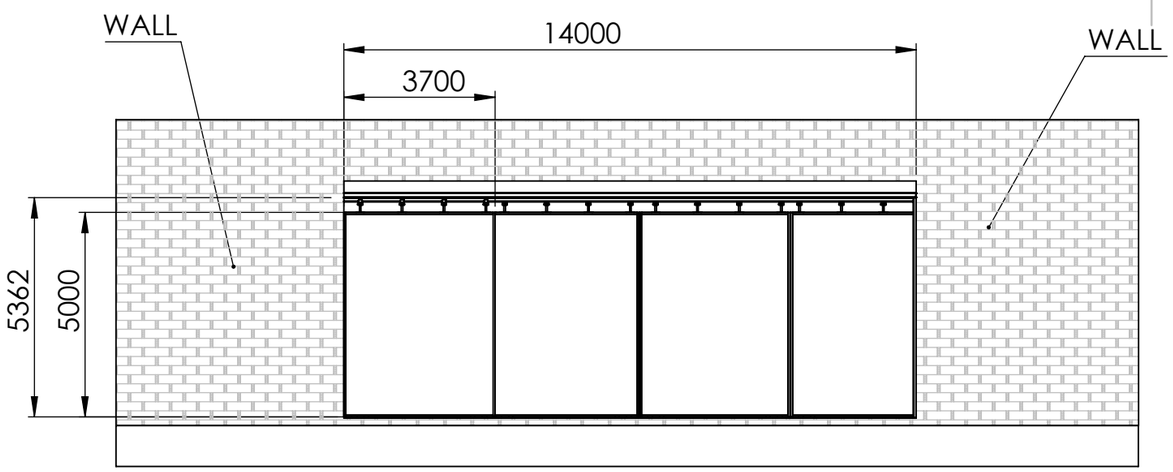


CLOSE POSITION

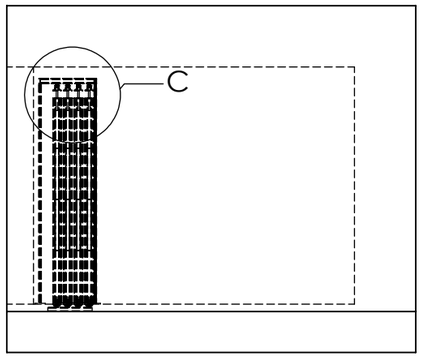


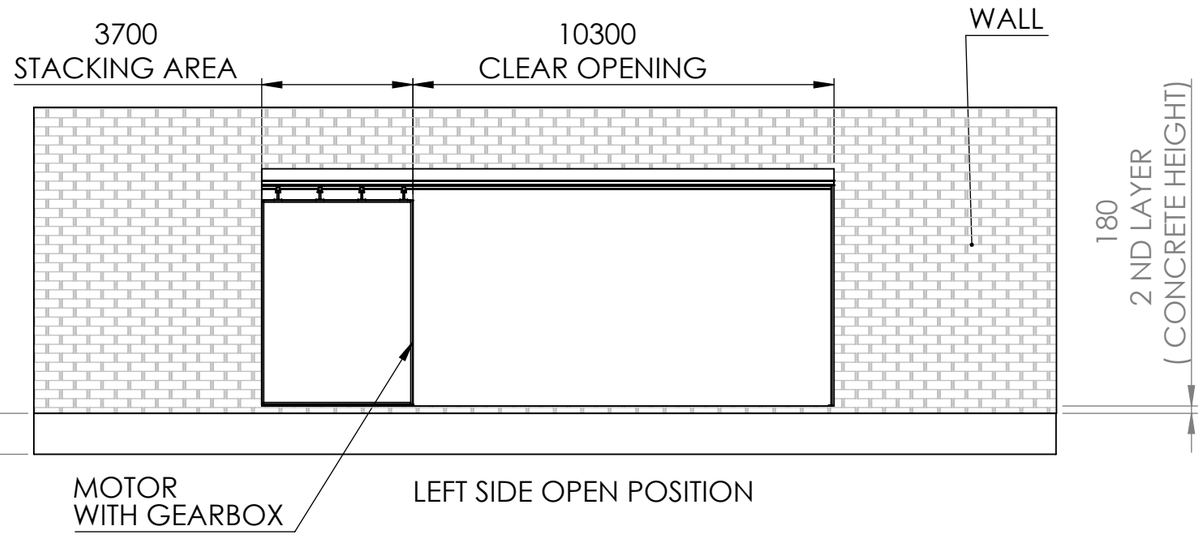

LEFT SIDE OPEN POSITION

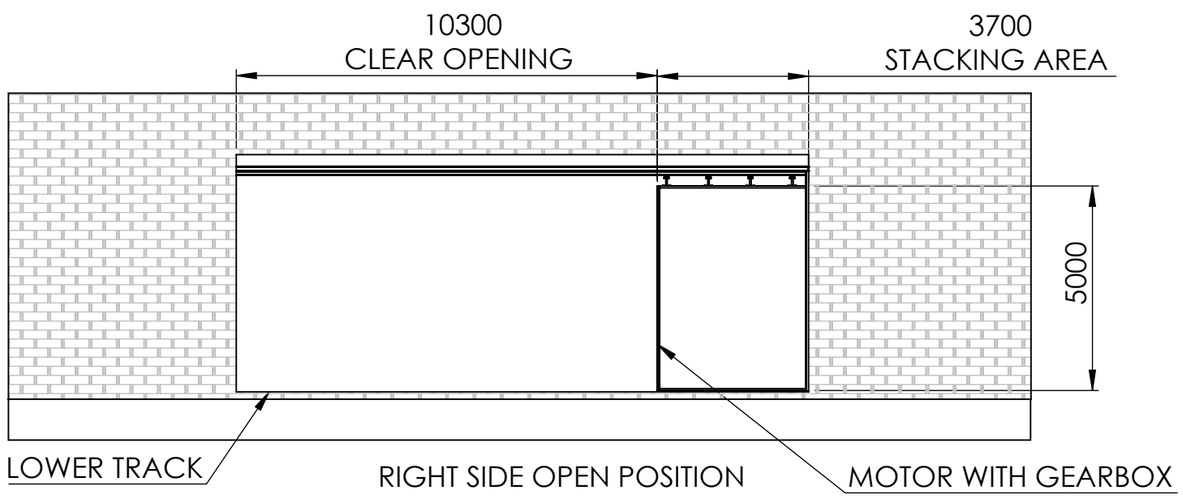

RIGHT SIDE OPEN POSITION

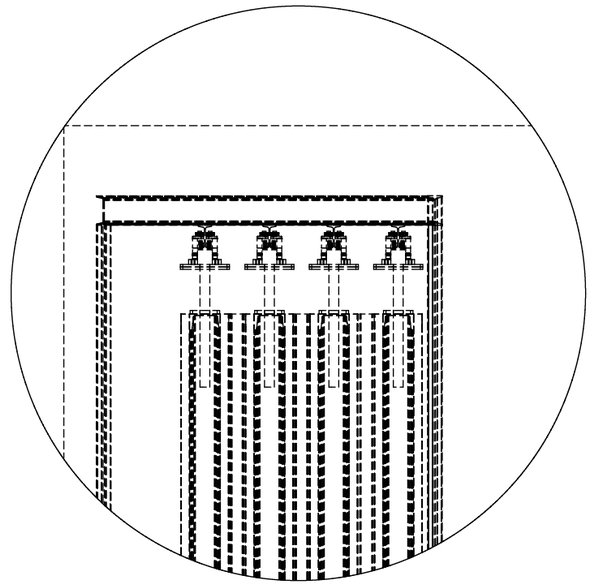

DETAIL C
SCALE 1 : 25

TITLE : HANGING SLIDING DOOR			NIHVA Technologies Pvt. Ltd. — **NIHVA TECHNOLOGIES PVT LTD**
	NAME	**SIGN**	**DATE**
DRAWN	BHARATI SABALE		23-12-2024
CHK'D	SURAJ WARALE		23-12-2024
APPV'D	VIJAY T.		23-12-2024
CLIENT NAME : ISRO			
PRODUCT NAME : HANGING SLIDING DOOR			
SITE LOCATION : ALUVA, KERALA			
DWG NO. GA			A3
DIMENSIONS ARE IN MILLIMETERS			REVISION : 0
SCALE:			SHEET 1 OF 1