



TOP VIEW

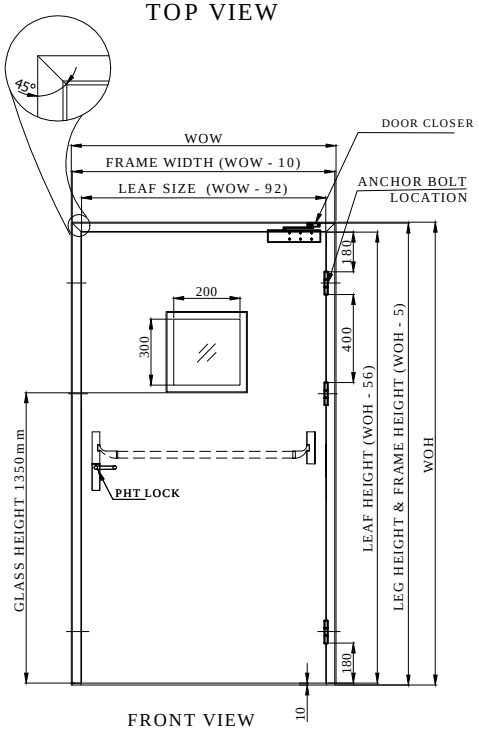


FRONT VIEW

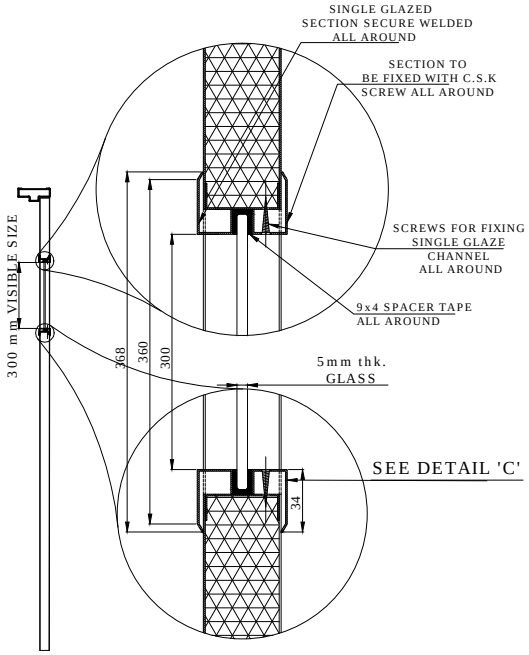

SIDE VIEW
SECTION A-A'


SINGLE GLAZE FIXING DETAIL

NOTE :
1. DOOR HINGES
2. DOOR CLOSER
3. DOOR EXTERNAL TRIM
4. DOOR PANIC BAR

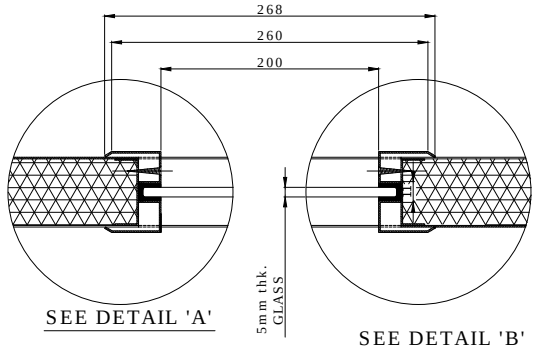



SEE DETAIL 'A'

SEE DETAIL 'B'

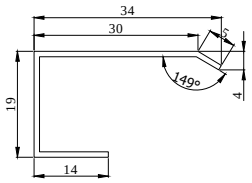


SEE DETAIL 'C'

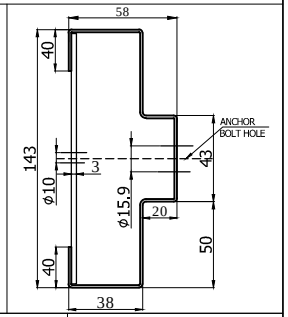

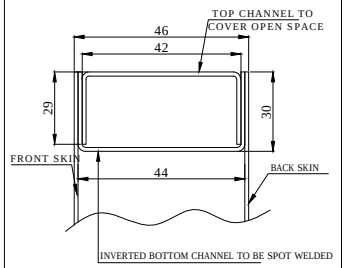

DOOR TOP SECTION DETAIL

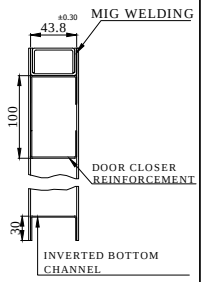

DOOR BOTTOM & TOP DETAIL

01	1000	2200	02	3020
SR. NO	WALL OPENING WIDTH	WALL OPENING HEIGHT	QTY	RAL

TOLERANCE - ±05mm

This drawing & design is the property of NIHVA TECHNOLOGIES. Not to be sold or copied to any other concern.

TITLE	SINGLE LEAF STEEL FIRE DOOR			NIHVA TECHNOLOGIES PVT. LTD. PUNE Tel : 020 66304033 Email:- info@nihva.com Website:- www.nihva.com
	NAME	SIGN	DATE	
DRAWN	P.V.A		25.06.2019	CLIENT - FERRERO INDIA PVT LTD
CHECK	V.M.T		25.06.2019	PROJECT -
APPRD.				SITE LOCATION - BARAMATI
If any queries contact : design@nihva.com				DWG. NO. : NIHVA/19-20/0039 REV- R00
ALL DIMENSION ARE IN mm				SCALE: NTS WT: SHEET: 01 OF 01