


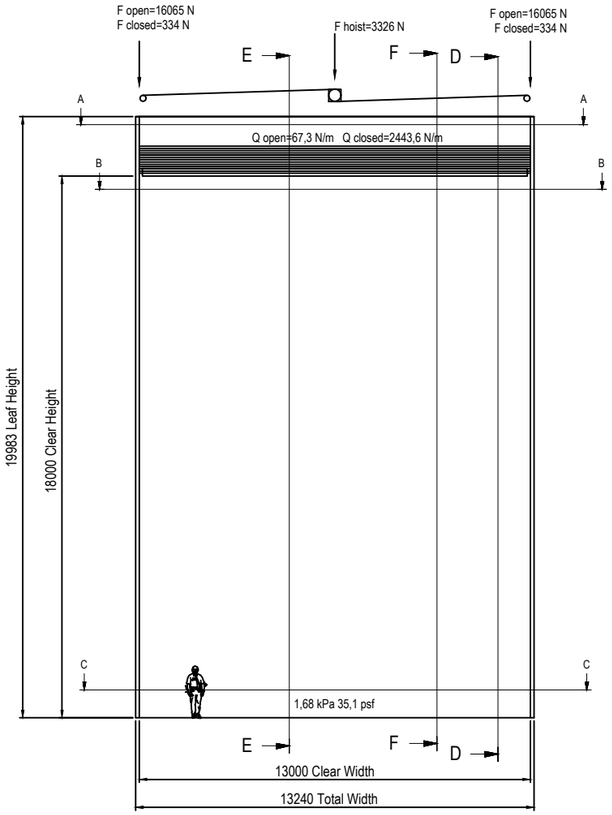


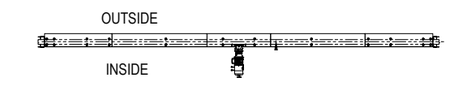


SECTION A-A

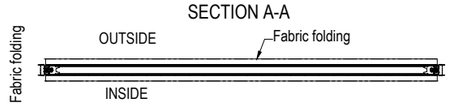


SECTION B-B

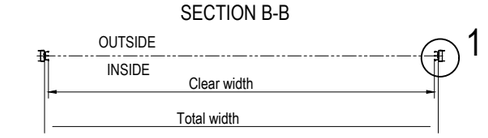


SECTION C-C

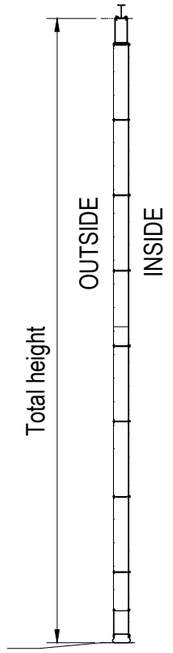


SECTION D-D

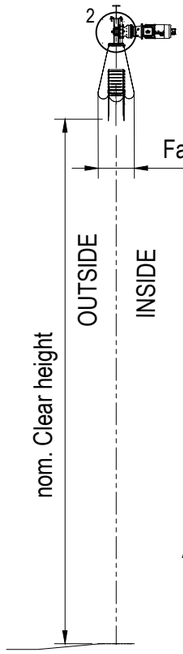


SECTION E-E

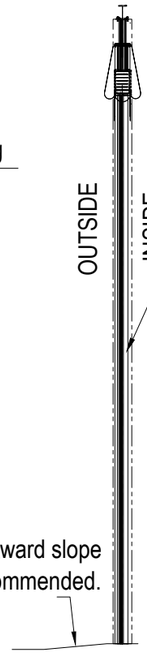

SECTION F-F

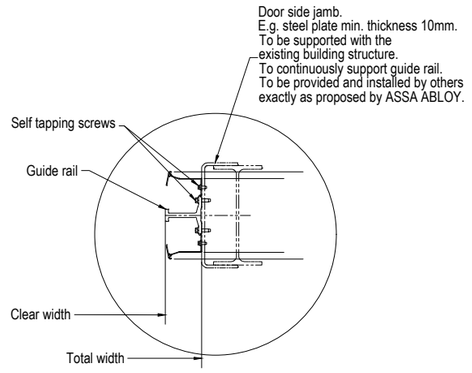

DETAIL 1

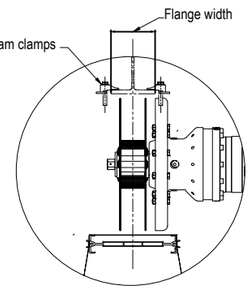

DETAIL 2

ASSA ABLOY	SALES REP. Ashish Nair	DATE ISSUED 2023-02-03
	SALES No. 223033	DATE DRAWN 2023-02-03
	SCALE N.T.S.	
	DRAWING No. 223033	REVISION

SBC Vizag
Vizag
India

Load diagram

Contact Information

Ashish Nair
Sales Manager - Middle East
MEGADOOR/
ASSA ABLOY Entrance Systems
P.O. Box 80983
Dubai, United Arab Amirates
Visiting address: Dubai Investment Park 1
Phone: +971 (0)4 88 52888
Mobile: +971 (0)50 632 04 95
E-mail: ashish.achuthan@assaabloy.com
www.assaabloyentrance.ae

Quotation only. Do not use for design.
Nominal static vertical loads are indicated.
A dynamic surload factor of 1.25 should be added to door leaf loads in open position.
Includes items provided by ASSA ABLOY Entrance Systems only.
Total weight: 4180 kg
Total static weight: 3709 kg
Total motor power: 7,7 kW
Total rated current: 18,6 A
Total peak current: 107,9 A
Power supply: 400V/50Hz/3ph
(max. allowed voltage drop at start: 5%)
Control system: 24V
Mains power to control panel supplied by others than ASSA ABLOY Entrance Systems.