

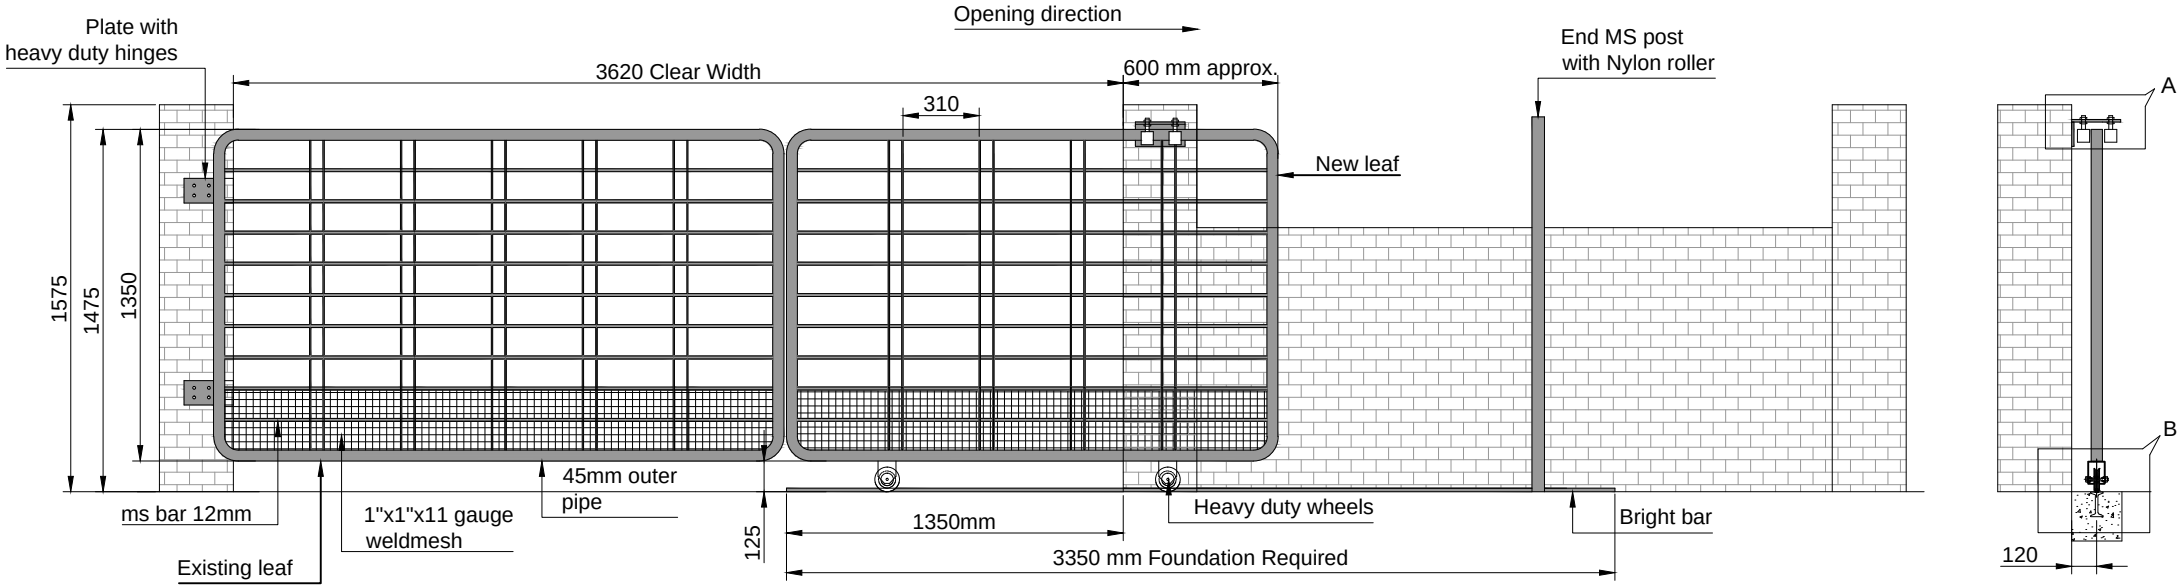


Inside Elevation


SIDE VIEW

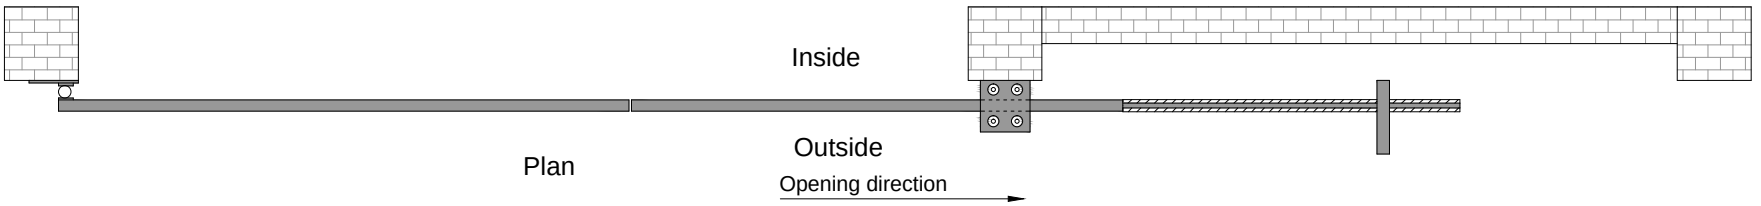

Plan

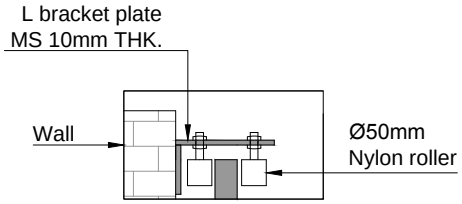

Detailed view of A

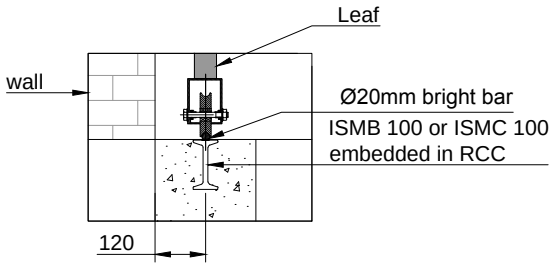

Detailed view of B

GATE SIZE- 1500(W) X 1350(H) mm

This drawing & designing is the property of NIHVA TECHNOLOGIES. Not to be sold or copied to any other concern.

TITLE: MANUAL SLIDING GATE		
	SIGN	DATE
DRAWN	OMKAR	27/02/17
CHECK	SAGAR P.	27/02/17
REV.		
APPROVAL	R.K.	27/02/17
If any queries contact : projects@nihva.com		
ALL DIMENSION ARE IN mm		

NIHVA TECHNOLOGIES PVT. LTD.
NIHVA TECHNOLOGIES PVT. LTD. PUNE
Tel : 020 66304033
Email:- info@nihva.com
Website:- www.nihva.com

CLIENT - RBCC	
PROJECT - RESIDENCE PROJECT	
SITE - AUNDH,PUNE	
DWG. NO. : NIHVA/16-17/151	
SCALE: NTS	WT: / SHEET: 01 OF 01