

PRODUCED BY AN AUTODESK EDUCATIONAL PRODUCT

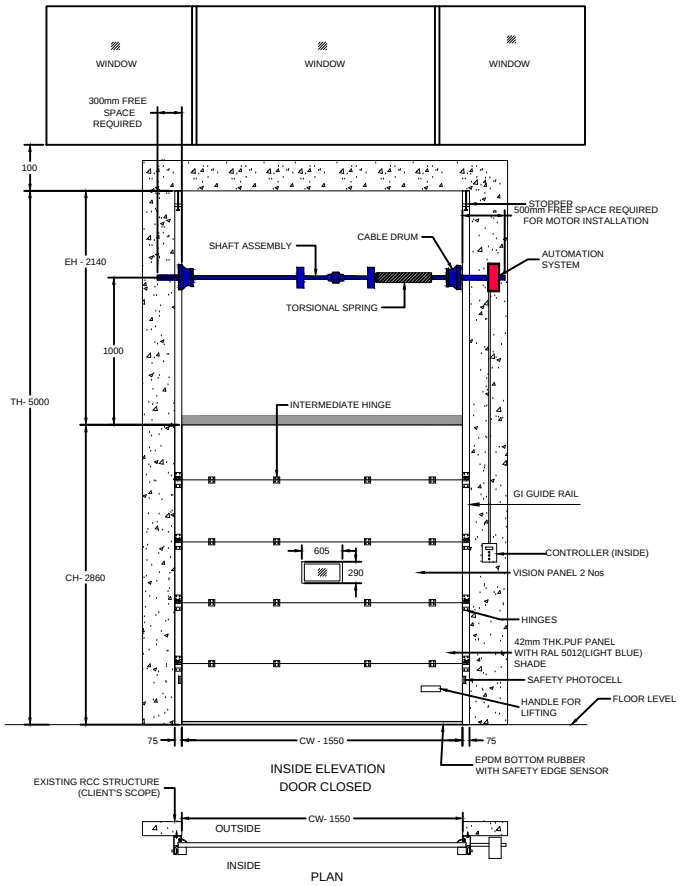


INSIDE ELEVATION
DOOR CLOSED

PLAN

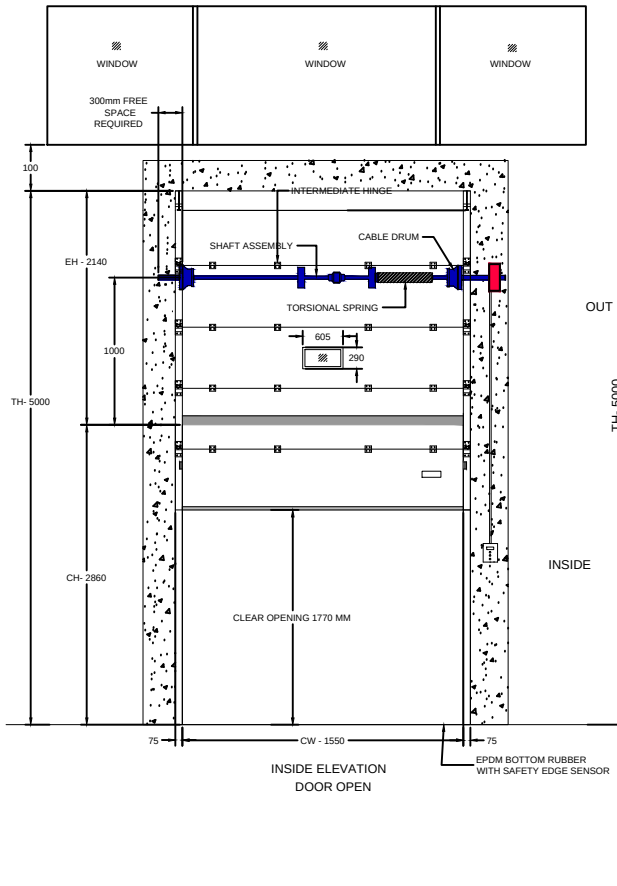

INSIDE ELEVATION
DOOR OPEN

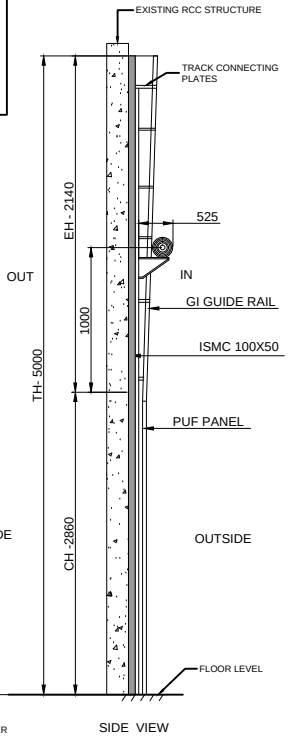

SIDE VIEW


DIMENSION :		
CLEAR WIDTH	CLEAR OPEN HEIGHT	QUANTITY
1550 mm	1770 mm	1

TECHNICAL DATA :

COMPONENTS	MATERIALS	SPECIFICATIONS
DOOR PANELS	GI & PUF	42mm CFC- FREE POLYURETHANE WITH 0.5mm THK, GI PRECOATED PANELS.
DOOR HINGE	——	HEAVY DUTY HINGES FOR INTERLOCKING OF PANELS
SHAFT ASSEMBLY	STD.	TORSIONAL SPRING WITH SHAFT & BEARING PLATES
FINISH		ENAMEL PAINT WITH APPROVED SHADE RAL 5012 LIGHT BLUE

IMPORTANT NOTES:

1. SINGLE PHASE POWER SUPPLY REQUIRED AT DOOR LOCATION.
3.ALL CIVIL WORK SHALL BE CLIENT'S SCOPE.

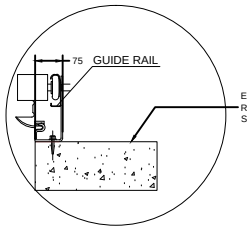

TRACK DETAILS

REV NO	DATE	DRAWN	REMARK
R03	17.03.20	P.A	1. CLEAR OPENING CHANGE
R02	16.03.20	P.A	1. CLEAR OPENING CHANGE
R01	11.02.20	P.A	1. CLEAR HEIGHT CHANGE

TOLERANCE: ± 10mm

SR NO	CLEAR WIDTH	CLEAR OPEN HEIGHT	QTY	TH	EH
01	1550 mm	1770mm	1	5000	2140

This drawing & design is the property of NIHVA TECHNOLOGIES. Not to be sold or copied to any other concern.

TITLE: SECTIONAL DOOR (VERTICAL LIFTING)

NIHVA TECHNOLOGIES PVT. LTD. PUNE
Tel : 020 66304033
Website:- www.nihva.com Email:- info@nihva.com

	NAME	SIGN	DATE
DRAWN	P.A		10.02.20
CHECK	G.J		10.02.20
APPROVAL			

CLIENT - CREATIVE CARVE PVT.LTD.
PROJECT -
SITE - PUNE
If any queries contact : design@nihva.com
DWG. NO. : NIHVA/19-20/0208/R02 REV: R02
ALL DIMENSION ARE IN mm
SCALE: NTS WT: SHEET: 01 OF 01

PRODUCED BY AN AUTODESK EDUCATIONAL PRODUCT

PRODUCED BY AN AUTODESK EDUCATIONAL PRODUCT