


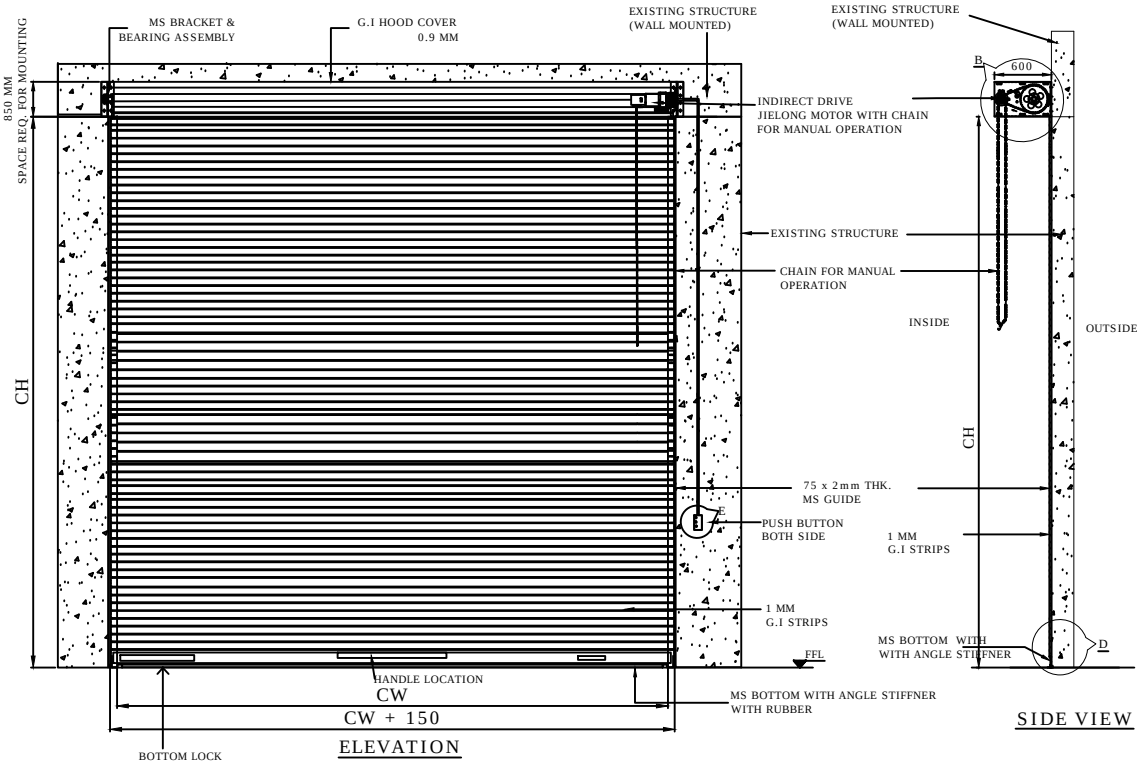


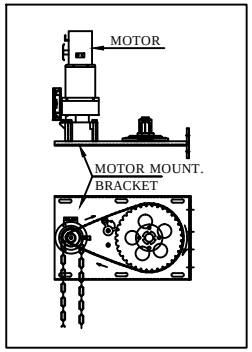


DETAILS : A & B

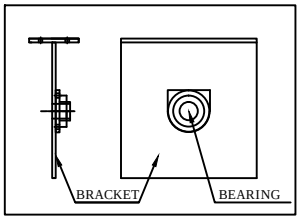


DETAILS : C

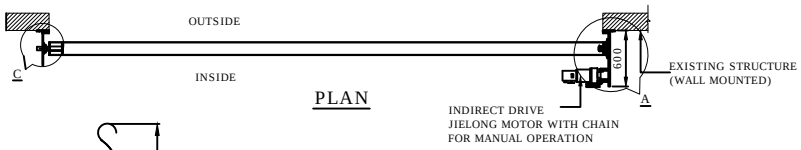

PLAN

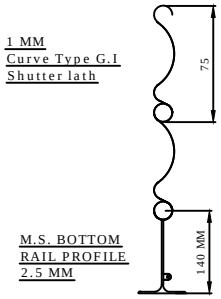

DETAILS : D

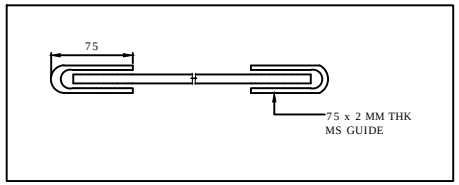

3100	3110	1	RAL -
CLEAR WIDTH (CW)	CLEAR HEIGHT (CH)	QUANTITY	RAL COLOR

(NOTE: REQUIRED TECHNICAL M.S STRUCTURE FOR SHUTTER SHOULD BE IN CLIENT SCOPE)

This drawing & design is the property of NIHVA TECHNOLOGIES. Not to be sold or copied to any other concern.

TITLE: MOTORIZED ROLLING SHUTTER

NIHVA TECHNOLOGIES PVT. LTD.

NIHVA TECHNOLOGIES PVT. LTD. PUNE
Tel : 020 66304033
Email:- info@nihva.com
Website:- www.nihva.com

	NAME	SIGN	DATE
DRAWN	P.A		31.07.2020
CHECK	G.J		31.07.2020
APPRD.			

CLIENT - TECHEXPERT ENGINEERING PVT LTD.

PROJECT -

SITE LOCATION - PUNE

If any queries contact : design@nihva.com

DWG. NO. : NIHVA/20-21/0038 REV- R00

ALL DIMENSION ARE IN mm

SCALE: NTS WT: SHEET: