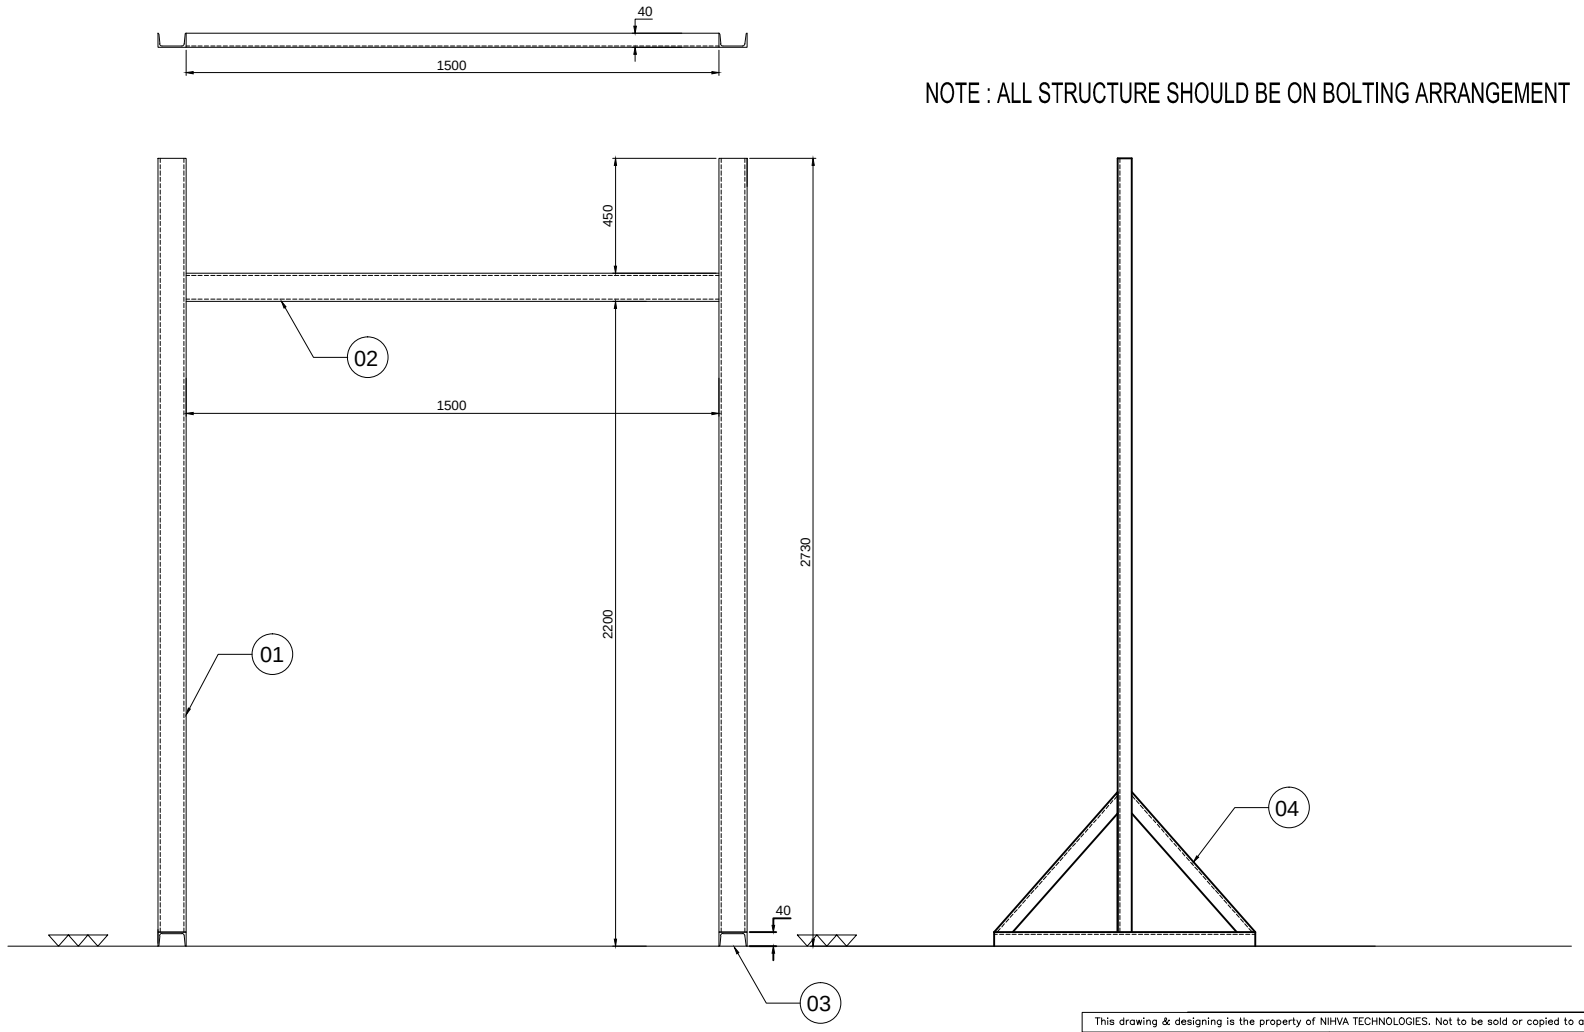

SR.NO	DESCRIPTION	SPECIFICATION	QTY
04	ISMC	75 X 40 X 800L	4 NOS
03	ISMC	75 X 40 X 1000L	2 NOS
02	ISMC	75 X 40 X 1500L	1 NO
01	ISMC	75 X 40 X 2690L	2 NOS

This drawing & designing is the property of NIHVA TECHNOLOGIES. Not to be sold or copied to any other concern.

TITLE
HIGH SPEED DOOR
HS9020GAT STRUCTURE.

	NAME	SIGN	DATE
DRAWN	P.V.A		28.05.19
CHECK	V.M.T		28.05.19
APPROVAL			

If any queries contact : design@nihva.com

ALL DIMENSION ARE IN mm

NIHVA
NIHVA TECHNOLOGIES PVT. LTD.
Website:- www.nihva.com

NIHVA TECHNOLOGIES
PVT. LTD. PUNE
Tel : 020 66304033
Email:- info@nihva.com

CLIENT -

PROJECT -

SITE -

DWG. NO. : NIHVA/19-20/VDR/049 | REV- 00

SCALE: NTS | WT: | SHEET: 01 OF 01