| SR NO | DESCRIPTION | SPECIFICATION | QTY |
|---|---|---|---|
| 1 | PROFILE | 655 X 30 THK X 1050L | 1 NO |
| 2 | ISMC | 75 X 40 X 645L | 20 NOS |
| 3 | PROFILE | 655 X 16 THK X 1050L | 1 NO |

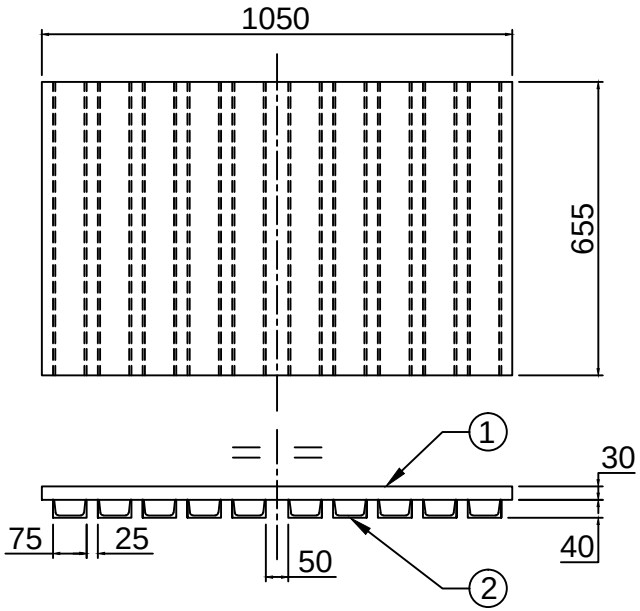


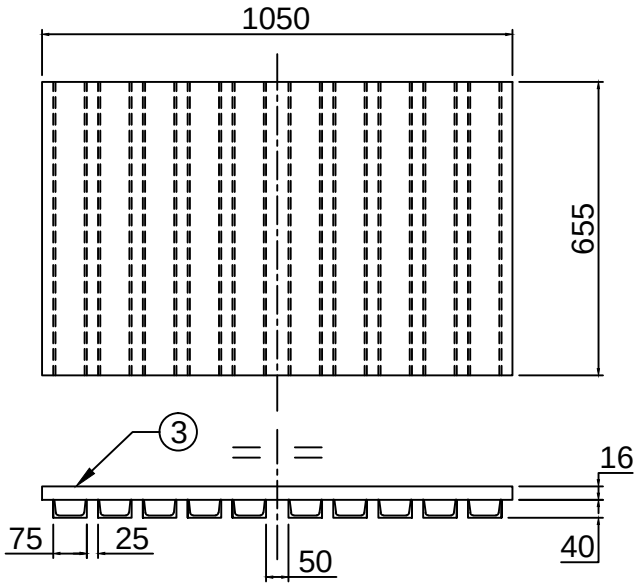


This drawing & design is the property of NIHVA TECHNOLOGIES. Not to be sold or copied to any other concern.

| TITLE: PRESSING BED | | | | NIHVA TECHNOLOGIES PVT. LTD. PUNE<br>Tel : 020 66304033<br>Email:- info@nihva.com<br>Website:- www.nihva.com | |
|---|---|---|---|---|---|
| | NAME | SIGN | DATE | | |
| DRAWN | P.A | | 22.10.2019 | CLIENT - | |
| CHECK | G.J | | 22.10.2019 | PROJECT - | |
| APPRD. | | | | SITE LOCATION - | |
| If any queries contact : design@nihva.com | | | | DWG. NO. :NIHVA/19-20/VDR/193 | REV- R00 |
| ALL DIMENSION ARE IN mm | | | | SCALE: NTS | WT: / SHEET: 01 OF 01 |