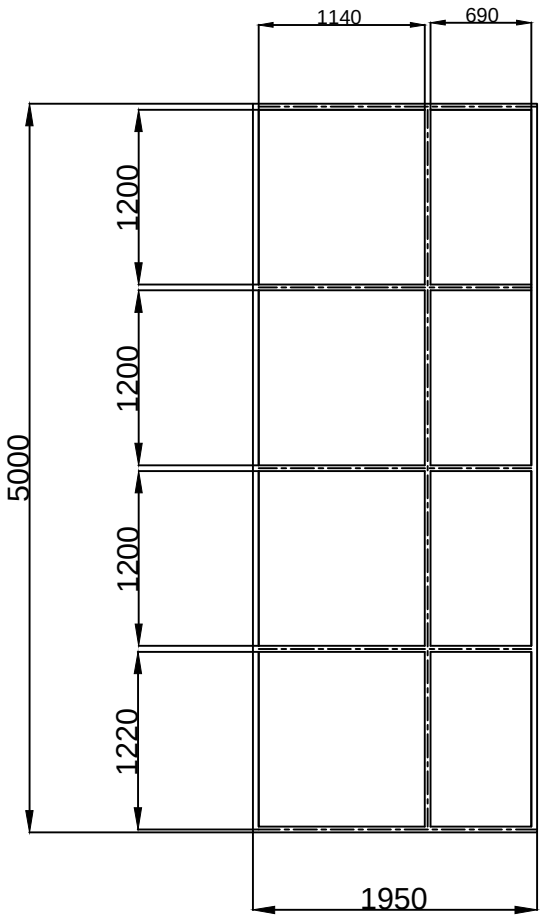

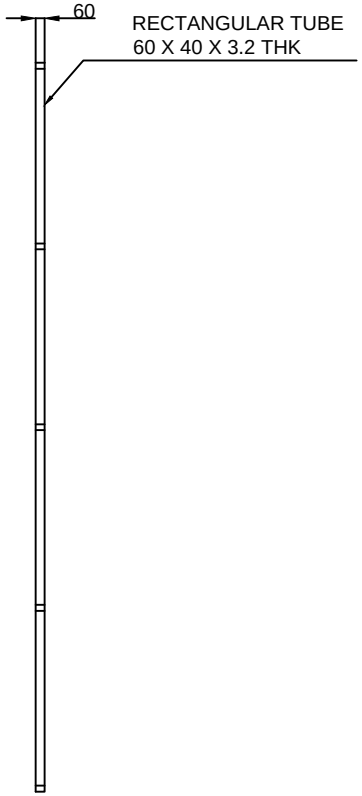

QTY=04 NOS

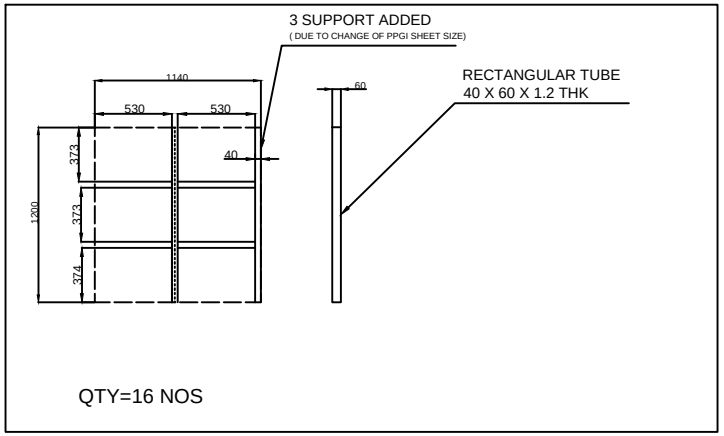

QTY=16 NOS

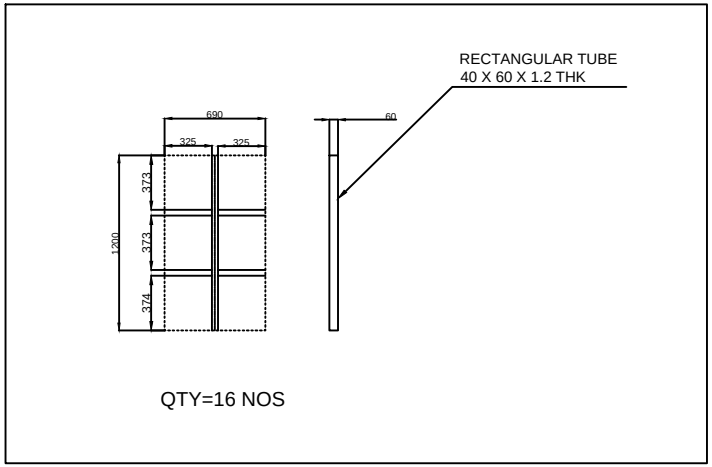

QTY=16 NOS

CRM DOOR 10

This drawing & design is the property of NIHVA TECHNOLOGIES. Not to be sold or copied to any other concern.

TITLE:- 4 LEAF BOTH SIDE CRM DOOR 10			
	NAME	DATE	SIGN
DRAWN	KISHAN	03/05/2022	
CHECK	M.SUTAR	03/05/2022	
APPRD.			
If any queries contact : design@nihva.com			
ALL DIMENSION ARE IN mm			

NIHVA TECHNOLOGIES PVT. LTD.
NIHVA TECHNOLOGIES PVT. LTD. PUNE
Tel : 020 66304033
Email:- info@nihva.com
Website:- www.nihva.com

CLIENT - LESTECH			
LOCATION - POSCO MANGAON			
PRODUCT - SLIDING DOOR			
DWG NO:-NIHVA/22-23/MFG/0018			REV- 0
SCALE: NTS	SCALE:-- 1:1	SHEET: 01 OF 01	

	Date	Revised By