


PRODUCED BY AN AUTODESK EDUCATIONAL PRODUCT

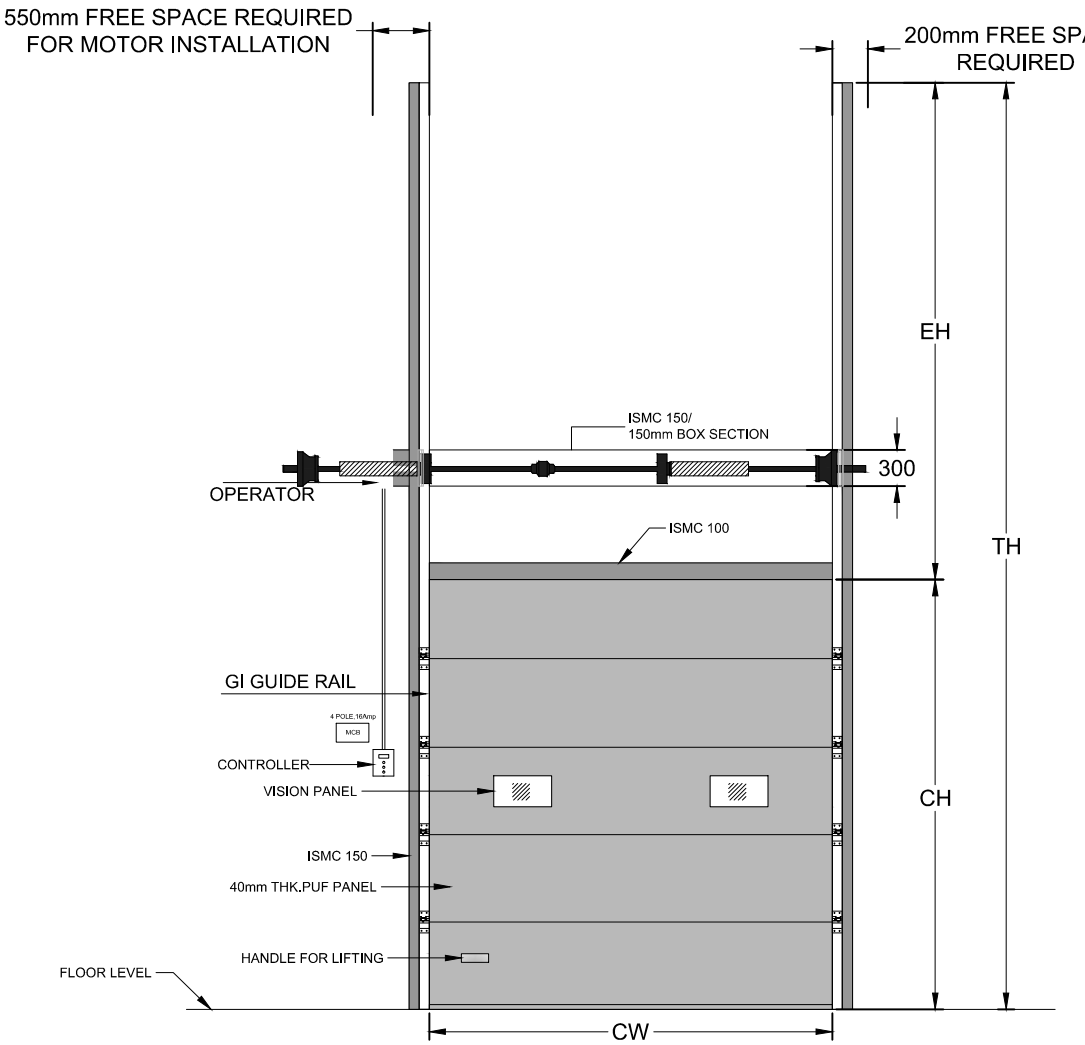

INSIDE VIEW

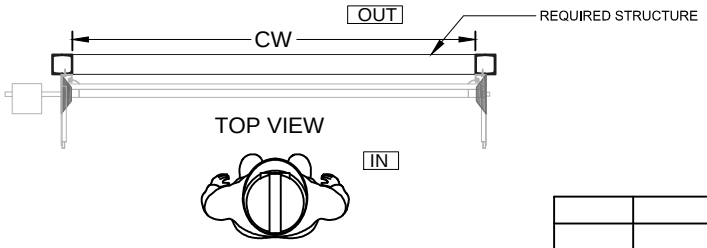

TOP VIEW

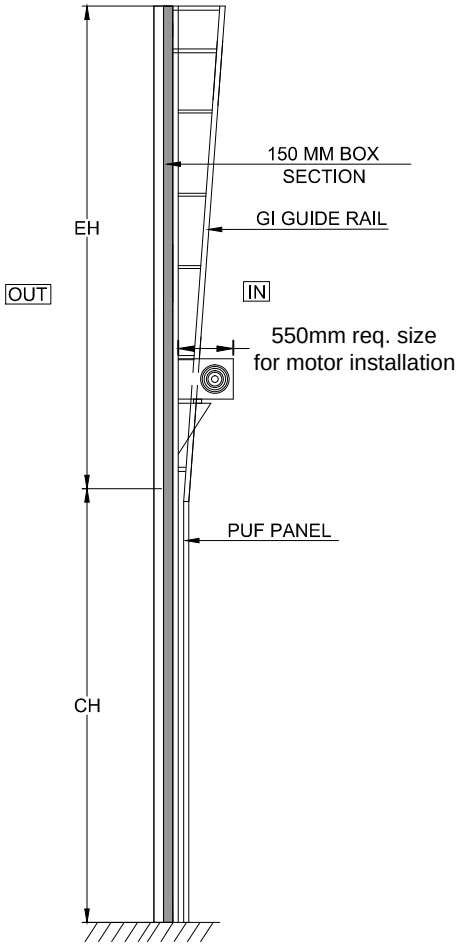

SIDE VIEW

SR NO	CLEAR WIDTH	CLEAR HEIGHT	QTY	TH	EH
01	4000mm	4000mm	1	8300	4300
02	3000mm	3000mm	1	6300	3300

R02	AKASH		1).TOTAL HEIGHT UPDATED.
R01	SURAJ		1).HEIGHT CHANGED. 2).GUIDE DETAIL ADDED.
REV NO	DRAWN	SIGN	DESCRIPTION

TOLERANCE: ±10mm

This drawing & design is the property of NIHVA TECHNOLOGIES. Not to be sold or copied to any other concern.

TITLE: SECTIONAL DOOR (VL)

NIHVA TECHNOLOGIES PVT. LTD. PUNE
Tel : 020 66304033
Email:- info@nihva.com
Website:- www.nihva.com

	NAME	SIGN	DATE
DRAWN	SURAJ		16/07/17
CHECK	VIKRANT		16/07/17
APPROVAL	R.D		16/07/17

CLIENT -PROJECTSPOOL ENGG. SERVICE PVT. LTD.

PROJECT -

SITE -

If any queries contact : design@nihva.com

DWG. NO. : NIHVA/18-19/0088/R02 REV: 2

ALL DIMENSION ARE IN mm

SCALE: NTS WT: SHEET: 01 OF 01

PRODUCED BY AN AUTODESK EDUCATIONAL PRODUCT