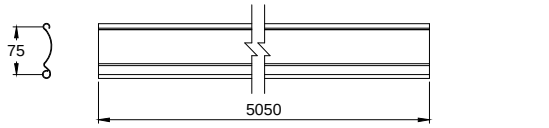

Curved slat

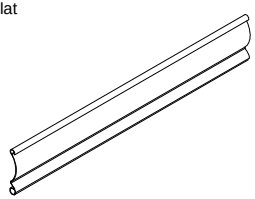

Slat profile- curved type.
Material- GI
Thickness - 1mm
Length of slats - 5050mm
Total no of slat - 95

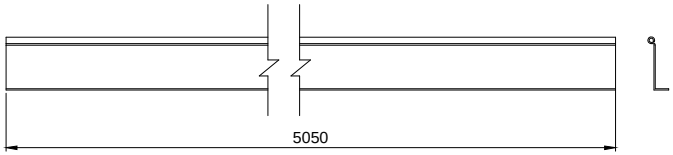

Material- MS
Thickness - 2.5mm
Length of bottom profile - 5050mm
Quantity- 1 Nos.

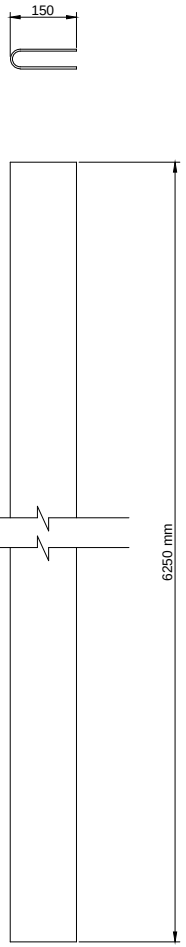

Material- MS
Thickness - 3mm
Length of guide - 6250mm
Quantity- 2 Nos.

This drawing & design is the property of NIHVA TECHNOLOGIES. Not to be sold or copied to any other concern.

TITLE

SLAT GUIDE & BOTTOM

NIHVA TECHNOLOGIES PVT. LTD. PUNE
Tel : 020 66304033
Email:- info@nihva.com
Website:- www.nihva.com

	SIGN	DATE
DRAWN	OMKAR	1/04/17
CHECK	SAGAR P.	1/04/17
REV.		
APPROVAL		

CLIENT -

PROJECT -

SITE -

DWG. NO. : NIHVA/17-18/VDR/001

If any queries contact : projects@nihva.com

SCALE: NTS | WT: | SHEET: 01 OF 01

ALL DIMENSION ARE IN mm