
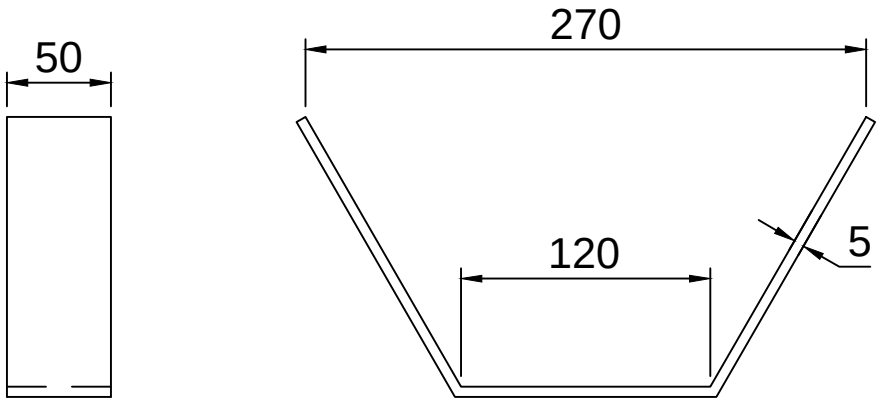


1. FLAT 50 X 5 X 450L = 1 NO

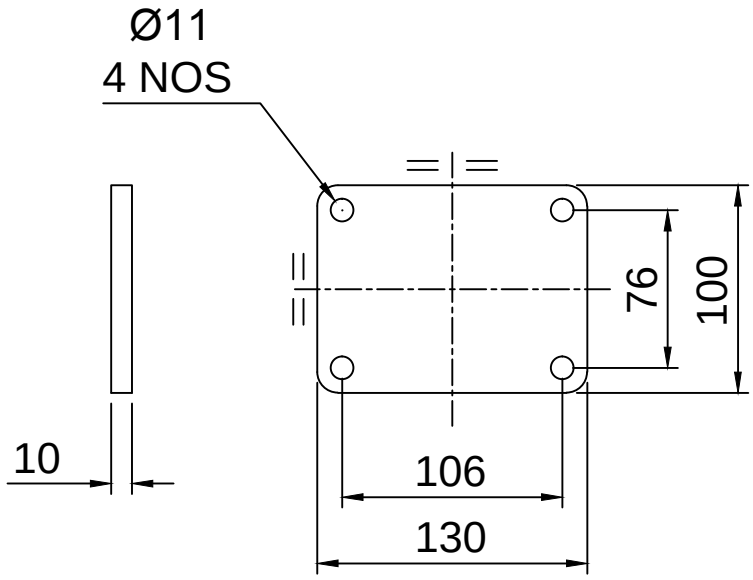

2. FLAT 100 X 10 X 130L = 1 NO
3. ANCHOR BOLT M10 X 100L = 4 NOS

NOTE : GROUTING PLATE WILL BE NOT WELD
SEND IT FREE WITH STAND.

This drawing & design is the property of NIHVA TECHNOLOGIES. Not to be sold or copied to any other concern.

TITLE: BEND FLAT & MOUNTING PLATE			NIHVA TECHNOLOGIES PVT. LTD. PUNE Tel : 020 66304033 Email:- info@nihva.com Website:- www.nihva.com		
	NAME	SIGN	DATE		
DRAWN	P.A		14.08.2018	CLIENT -	
CHECK	P.A		14.08.2018	PROJECT -	
APPRD.	S.L		14.08.2018	SITE LOCATION -	
If any queries contact : design@nihva.com				DWG. NO. : NIHVA/18-19/VDR/092	
ALL DIMENSION ARE IN mm				SCALE: NTS	WT: REV- 00