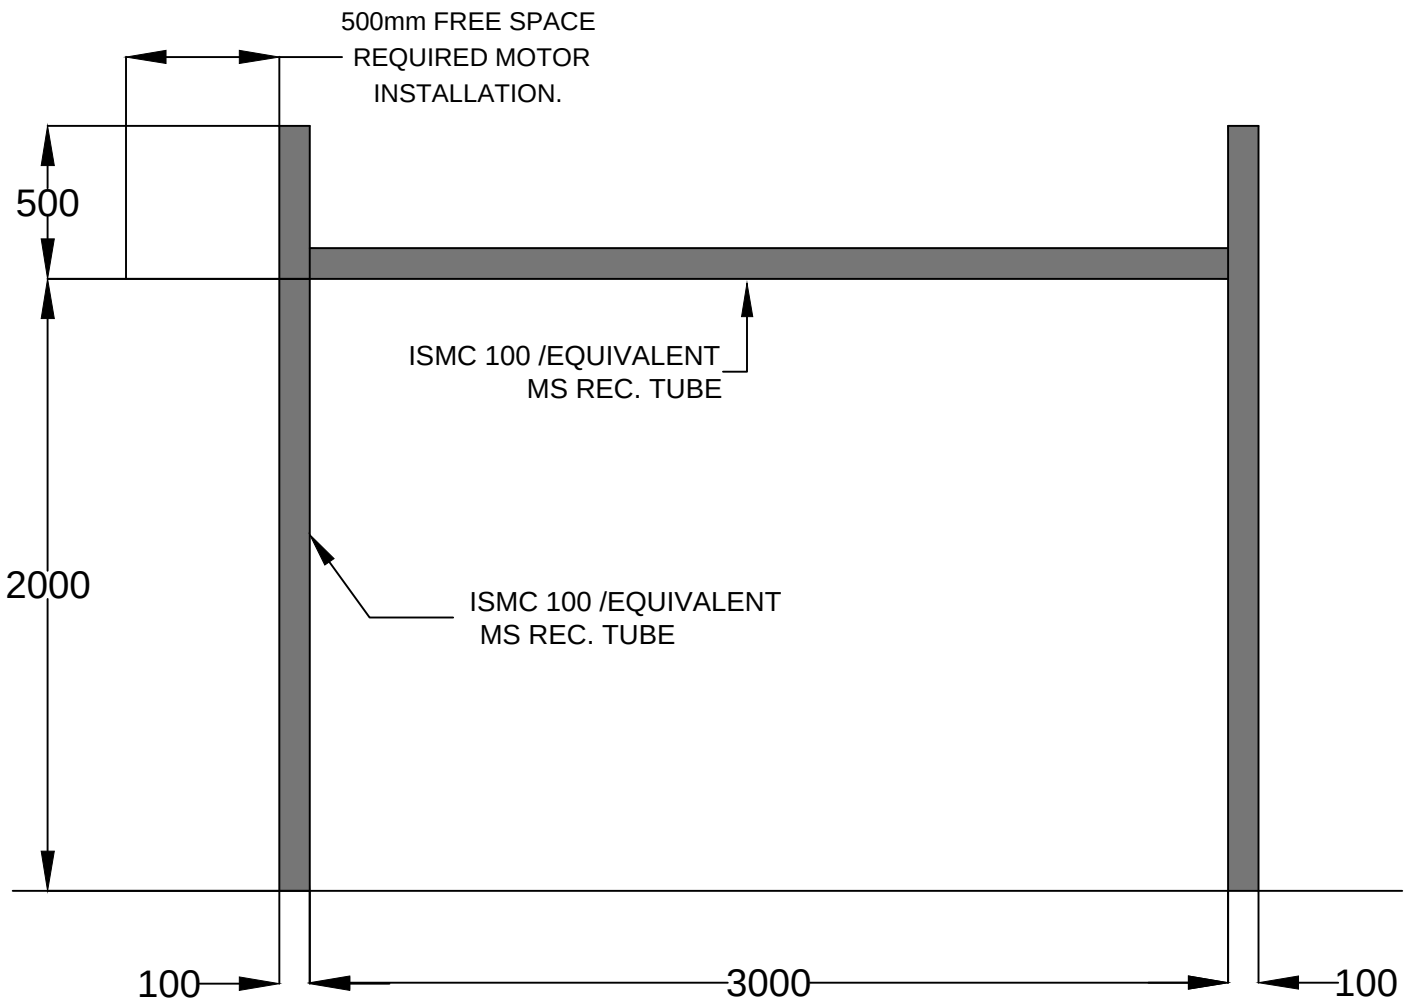

DIMENSION :		
CLEAR WIDTH	CLEAR HEIGHT	QUANTITY
3000	2000	1

MATERIAL :

THICKNESS :

NIHVA TECHNOLOGIES PVT. LTD.

NIHVA TECHNOLOGIES
PVT. LTD. PUNE
Email:- info@nihva.com
Website:- www.nihva.com

TITLE:

STRUCTURE HSD
RR 300 S

CLIENT'S APPROVAL :

CLIENT- GESTAMP AUTOMOTIVE INDIA PVT. LTD

PROJECT -

SITE LOCATION -CHAKAN, PUNE

DWG. NO. : NIHVA/17-18/0227/R01

SCALE: NTS	WT:	SHEET:1 OF 1

DRAWN BY: SURAJ	DATE: 11-10-2017
CHECK BY: SHEKHAR	DATE: 11-10-2017
APPROVED BY : SHEKHAR	DATE: 11-10-2017

If any queries contact : projects@nihva.com

NOTE: ALL DIMENSIONS ARE IN mm

CLEAR WIDTH	CLEAR HEIGHT	QUANTITY
3000	2000	1

REV: 01.STRUCTURE SIZES REVISED AS PER REVISED DOOR DIMENSION.

THIS DRAWING & DESIGNING IS THE PROPERTY OF NIHVA TECHNOLOGIES. NOT TO BE SOLD OR COPIED TO ANY OTHER CONCERN.