


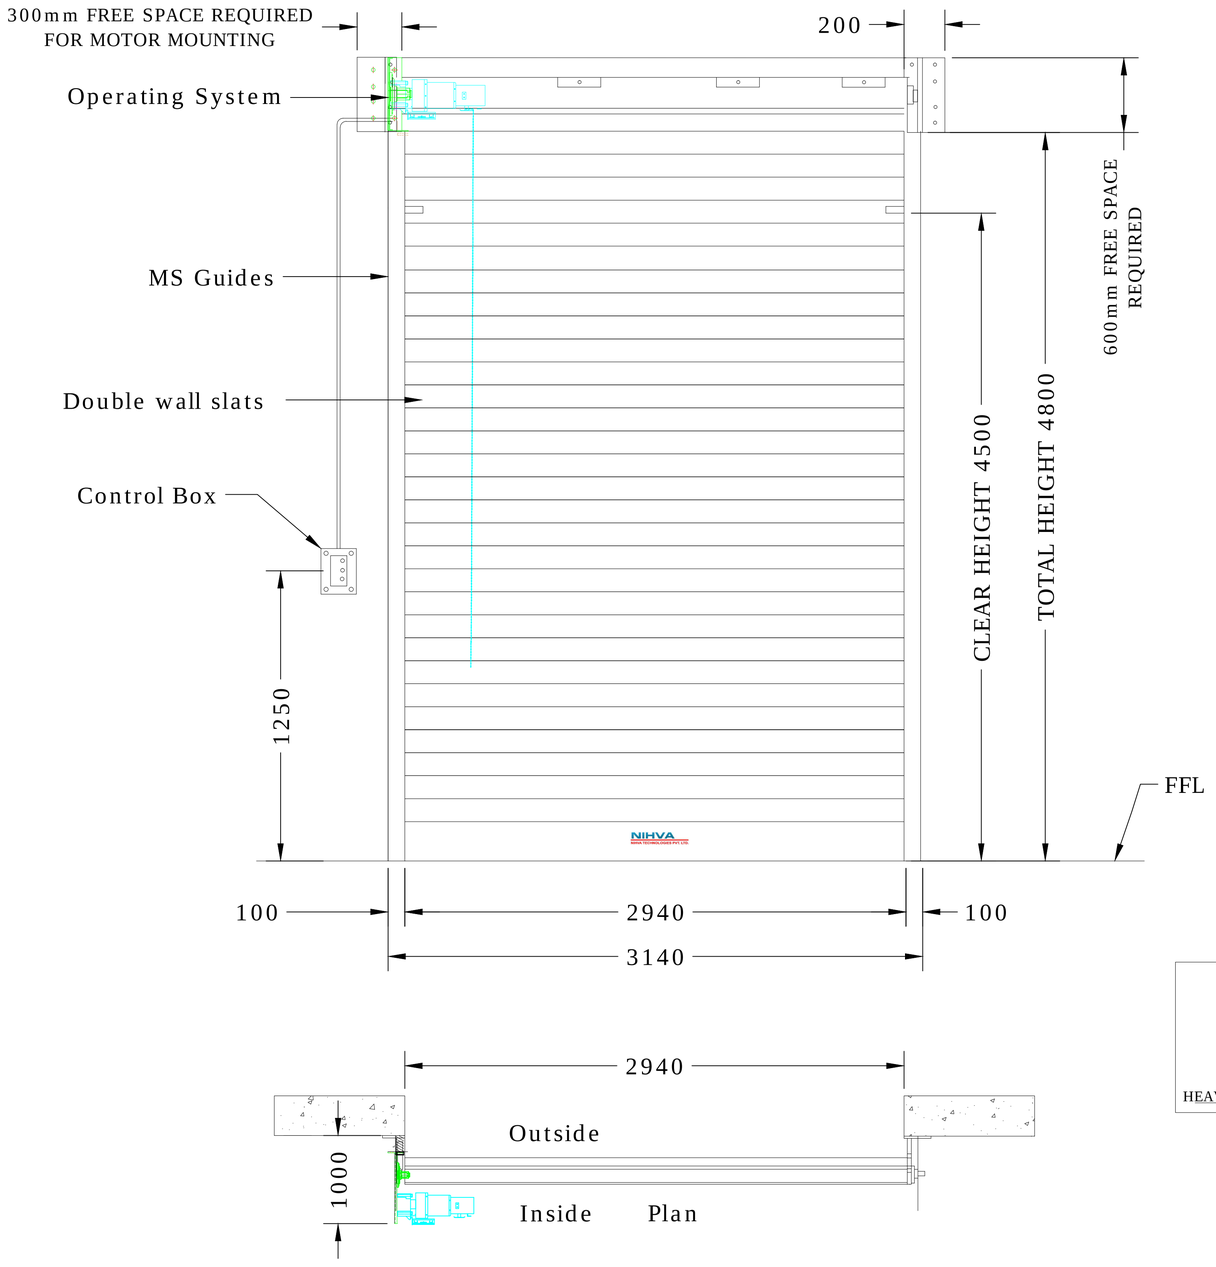


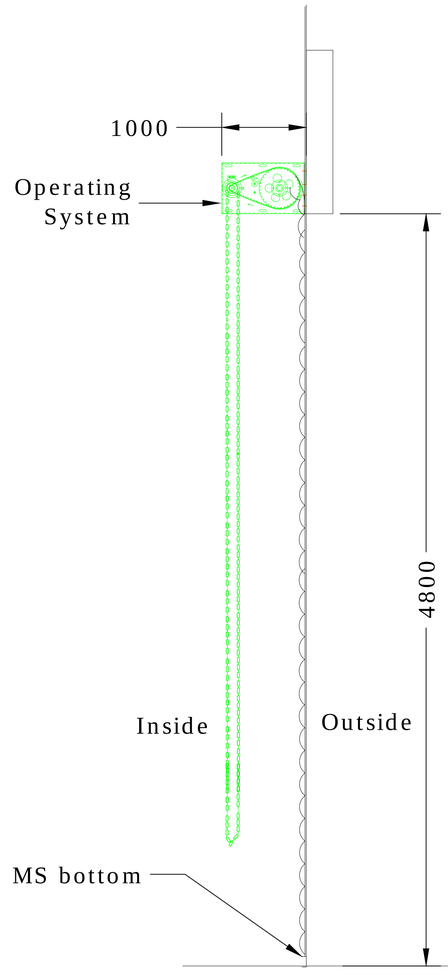

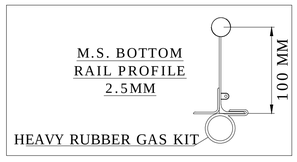

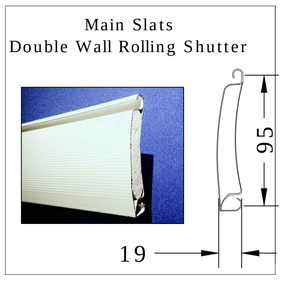

SHUTTER LOCATION- SHUTTER 5 STARTS FROM NORTH SIDE.

CLEAR WIDTH (CW)	CLEAR HEIGHT (CH)	TOTAL HEIGHT (TH)	MOTOR POSITION
2940mm	4500mm	4800mm	LEFT

NOTE: 1.COLOUR OF THE SHUTTER WILL BE OFF WHITE.
2.SHUTTER WILL ROLL UPTO 4500mm HEIGHT ONLY.

REVISION 2- SIZE OF SHUTTER REVISED AS PER SITE CONDITIONS.

DIMENSION :

CLEAR WIDTH	CLEAR HEIGHT	TOTAL HEIGHT
2940mm	4500mm	4800mm

MATERIAL :

THICKNESS :

NOTE-
01.REQUIERD STRUCTURE FOR ROLLING SHUTTER WILL BE IN CLIENT'S SCOPE.
02.SINGLE PHASE SUPPLY IS REQUIRED.

NIHVA TECHNOLOGIES PVT. LTD.
NIHVA TECHNOLOGIES PVT. LTD. PUNE
Email:- info@nihva.com
Website:- www.nihva.com

TITLE:

DOUBLE WALL ROLLING SHUTTER 5

CLIENT'S APPROVAL :

CLIENT - LUPIN

PROJECT - LUPIN

SITE LOCATION -NAGPUR.

DWG. NO. : NIHVA/17-18/0030/R02/5

SCALE: NTS	WT:	SHEET:1 OF 1
DRAWN BY: OMKAR		DATE: 29-05-2017
CHECK BY: SAGAR P.		DATE: 29-05-2017
APPROVED BY : S.S		DATE: 29-05-2017

If any queries contact : projects@nihva.com

NOTE: ALL DIMENSIONS ARE IN mm

THIS DRAWING & DESIGN IS THE PROPERTY OF NIHVA TECHNOLOGIES. NOT TO BE SOLD OR COPIED TO ANY OTHER CONCERN.